
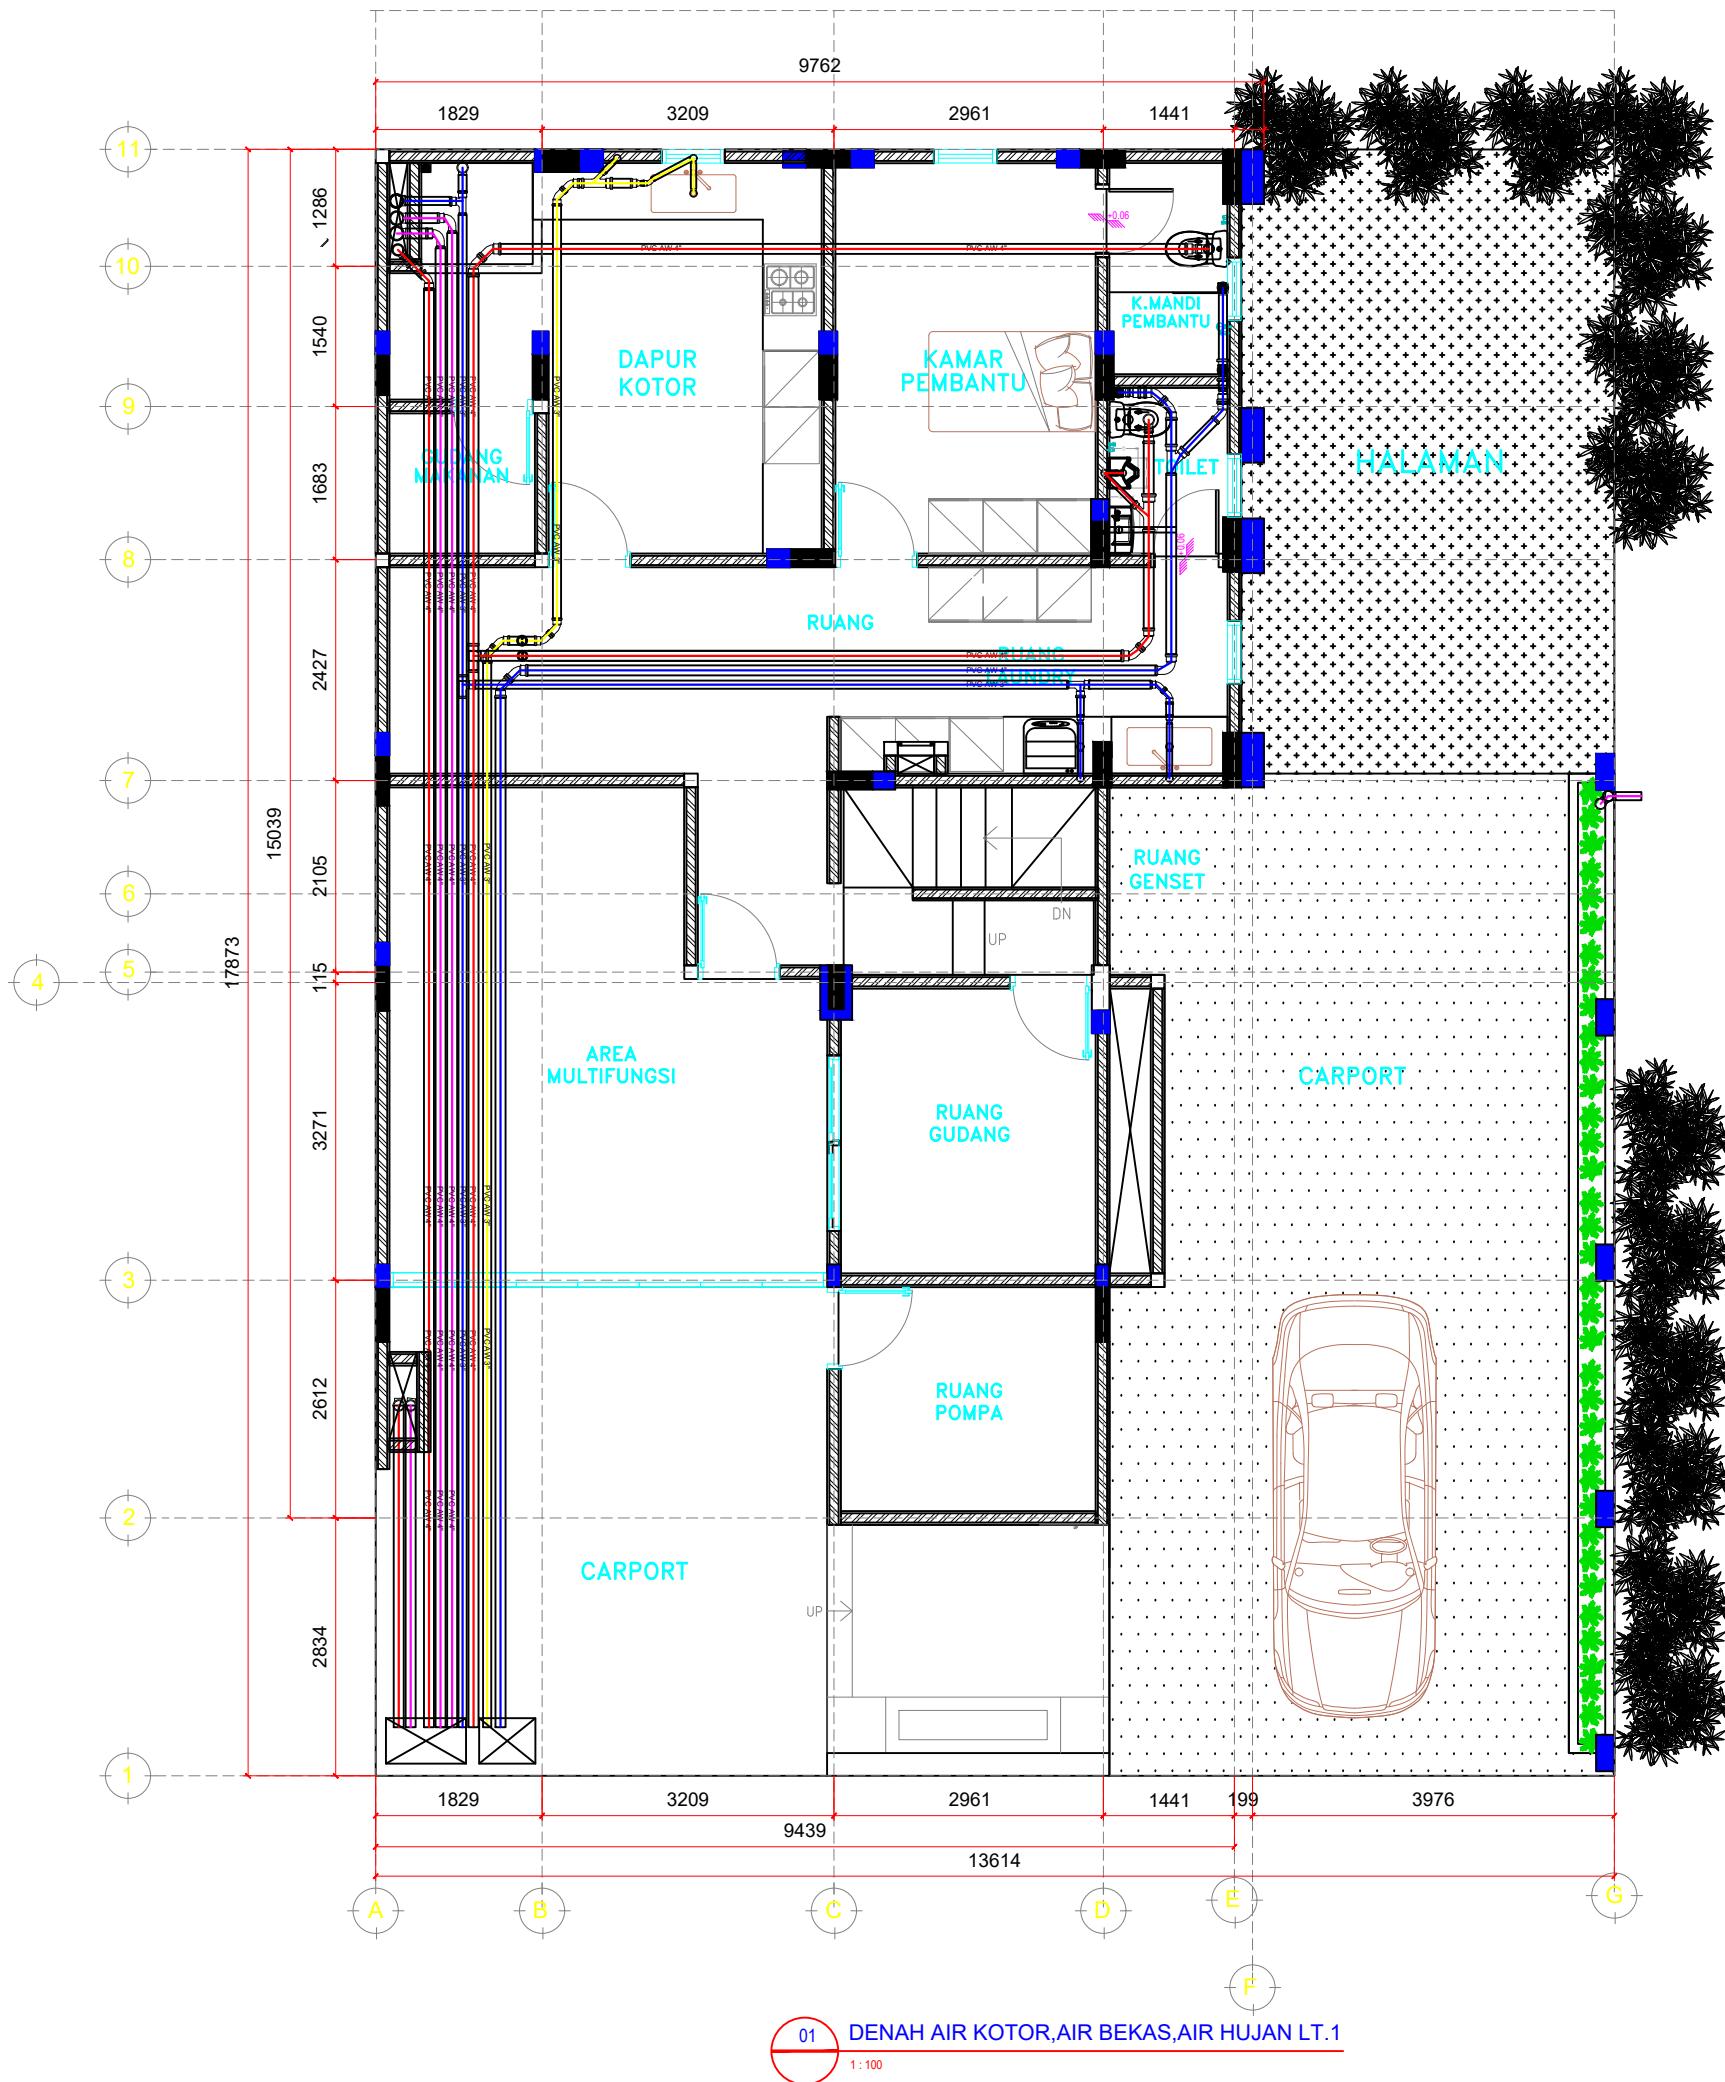


REVISI	TGL

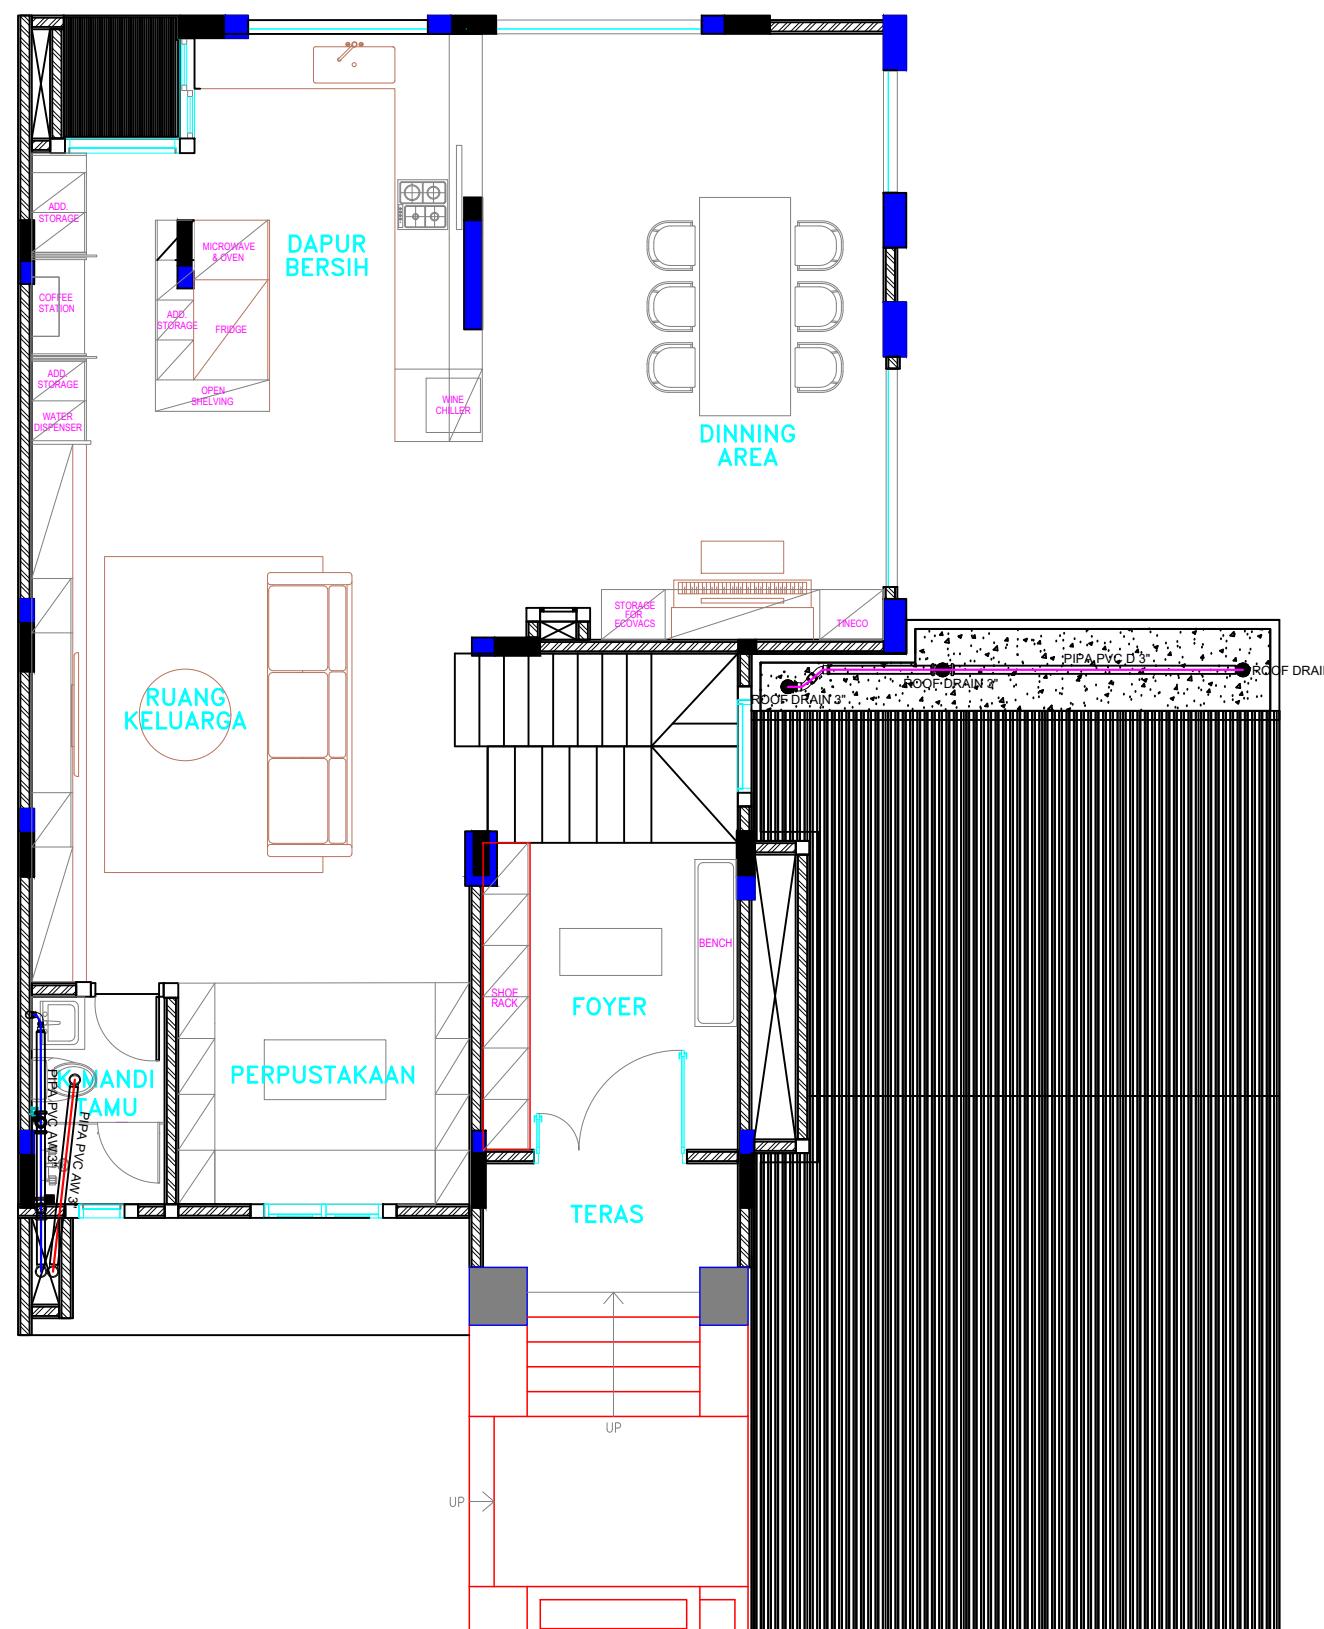

01 DENAH AIR KOTOR,AIR BEKAS,AIR HUJAN LT.2
1:100

KETERANGAN			
—	AIR KOTOR		
—	AIR BEKAS		
—	AIR AIR HUJAN		
—	AIR BEKAS ZINK		

CATATAN :

PEMBERI TUGAS :

ARSITEK :

DRAFTING :

REVISI :

JUDUL GAMBAR :

SKALA :

DIGAMBAR :

TGL.:

DIPERIKSA :

TGL.:

DISETUJUI :

TGL. -


DIKELUARKAN UNTUK :

NO. PROYEK :

NO. GAMBAR :

KODE GAMBAR :

REVISI :

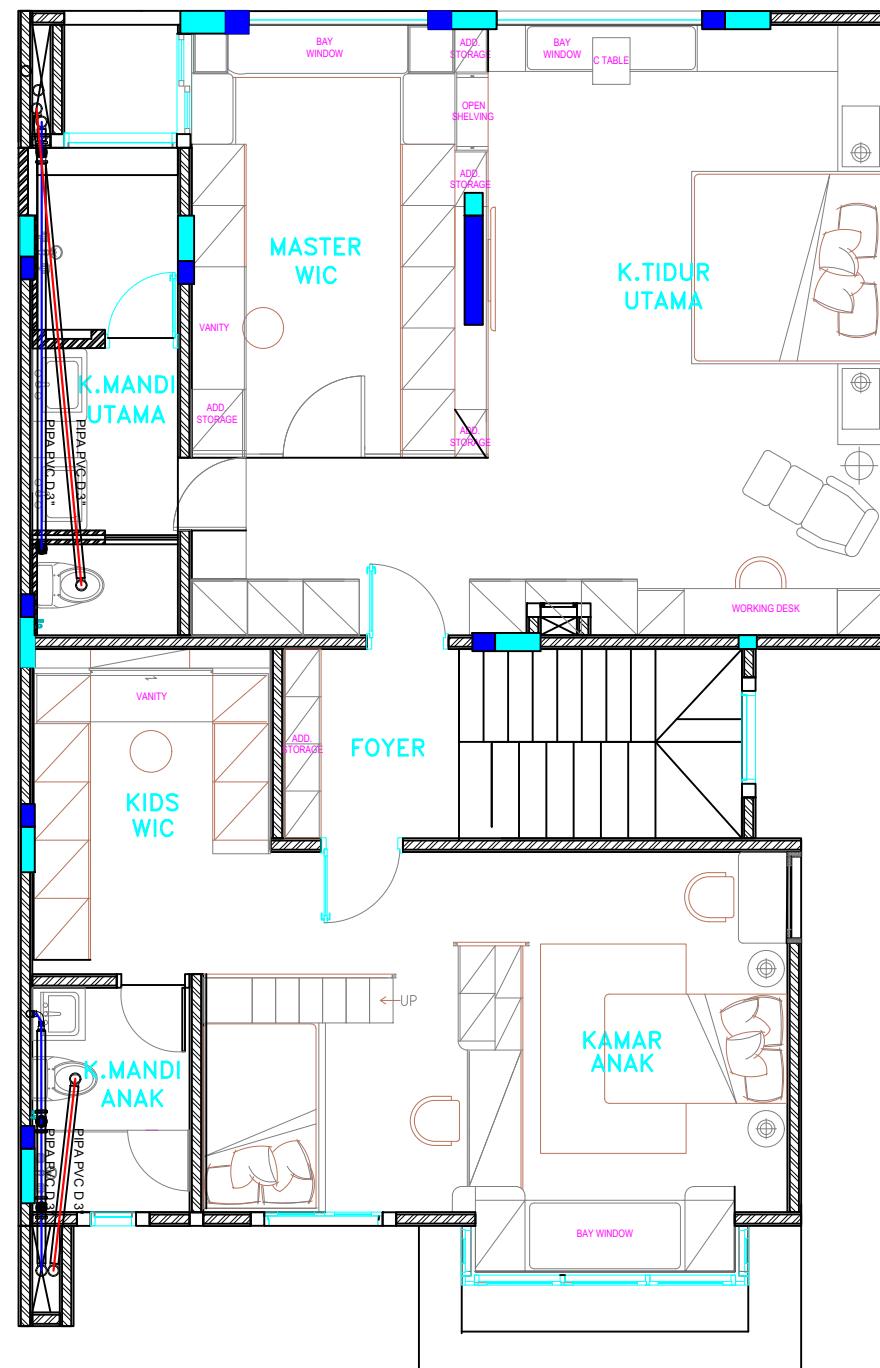


01 DENAH AIR KOTOR, AIR BEKAS, AIR HUJAN LT.3
1:100

KETERANGAN


—	AIR KOTOR
—	AIR BEKAS
—	AIR AIR HUJAN
—	AIR BEKAS ZINK
—	
—	
—	

CATATAN :

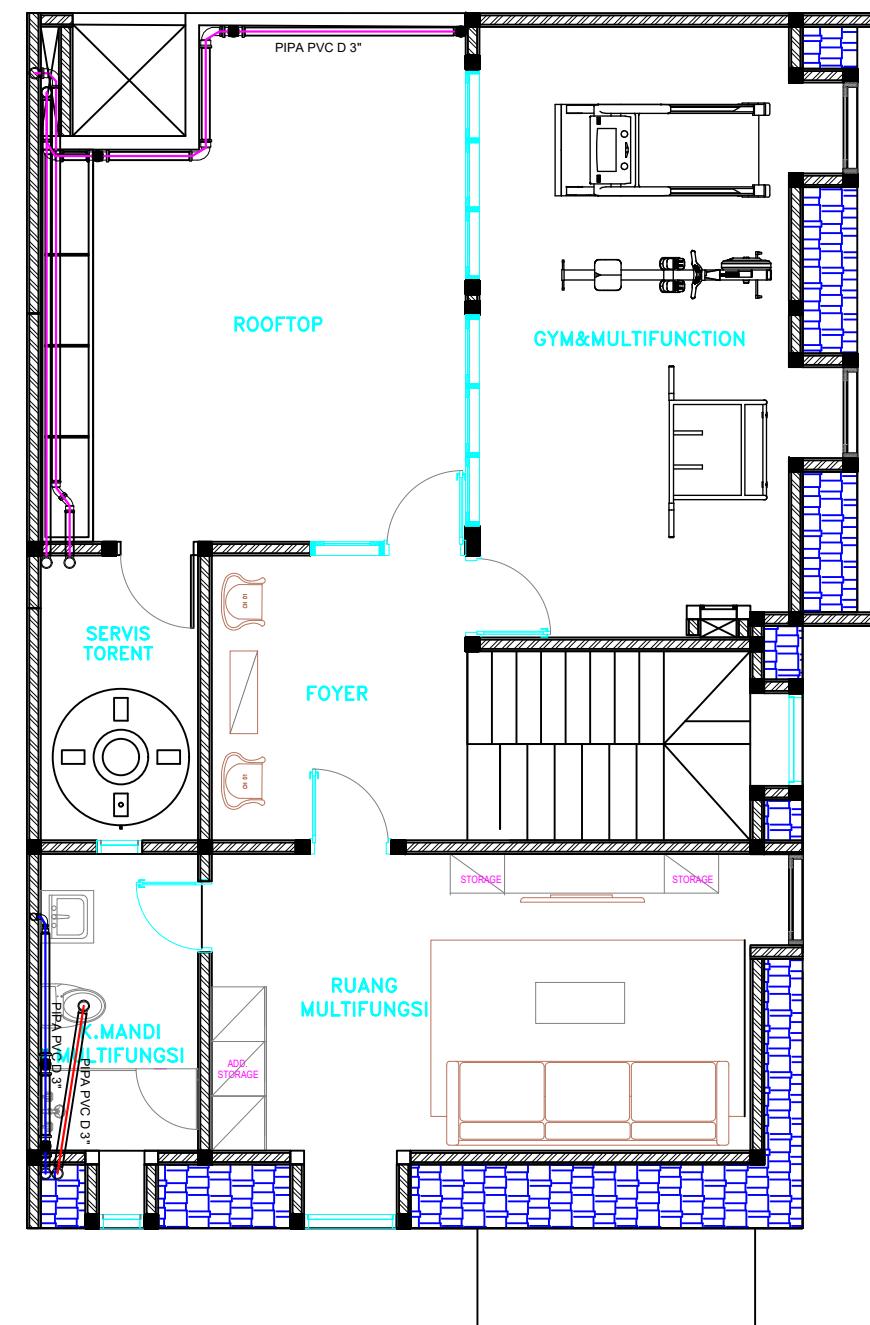

01 DENAH AIR KOTOR,AIR BEKAS,AIR HUJAN LT.4
1 : 100

KETERANGAN	
—	AIR KOTOR
—	AIR BEKAS
—	AIR AIR HUJAN
—	AIR BEKAS ZINK

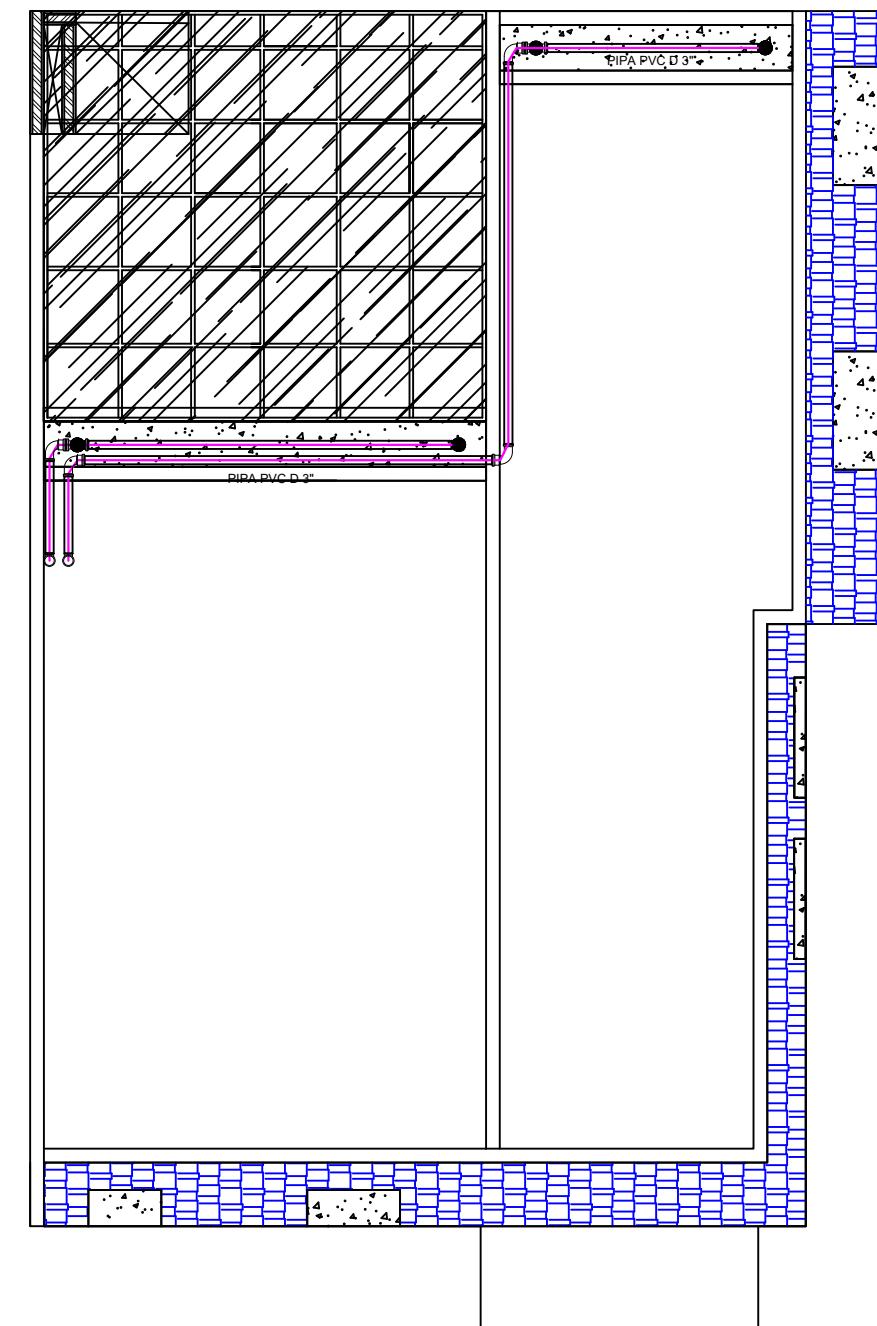

01 DENAH AIR KOTOR, AIR BEKAS, AIR HUJAN ATAP
1:100

KETERANGAN			
—	AIR KOTOR		
—	AIR BEKAS		
—	AIR AIR HUJAN		
—	AIR BEKAS ZINK		