



NAMA PROYEK	RESIDENTIAL HOUSE AKASIA 2 / 59		
CATATAN :	<p>Semua garis, retangan dan lingkaran semi lingkaran pada gambar ini dibungkus dan diperbaiki tanpa [In] terfull. Kontraktor berwenang untuk memaksa dimensi terhadap keadaan lapangan dan apabila ada ketidakcocokan harus diturunkan disukai.</p> <p>Gambar berdimensi tidak diperkenankan diskusi.</p> <p>Sebelum pekerjaan dilaksanakan, kontraktor berwenang untuk meminta persetujuan gambar kerja dan contoh bahan dari Arsitek.</p>		
PEMBERI TUGAS			
ARSITEK	ERIC HANDAYA, S.T I.A.I		
DRAFTING			
REVISI			
TGL			
ON			
JUDUL GAMBAR :	LAYOUT FRONT PARSIAL FACADE 1ST FLOOR LAYOUT RIGHT PARTIAL FACADE 1ST FLOOR		
SKALA :	DIGAMBAR	TGL.	
1:50	DIPERIKSA	TGL.	
	DISETUJUI	TGL.	
DISETUVUI PEMB. TUGAS		TGL.	-
DIKELUARKAN UNTUK :	FOR DESIGN DEVELOPMENT		
NO. PROYEK	NO. GAMBAR :	KODE GAMBAR :	REVISI :
	44	AR-44	

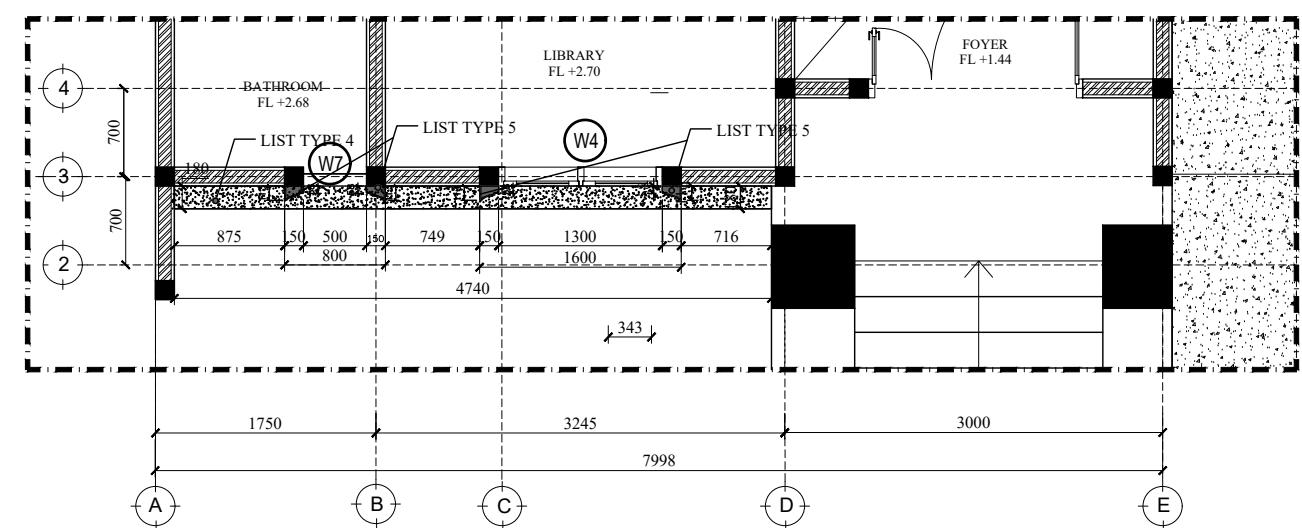

01 LAYOUT FRONT PARSIAL FACADE 1ST FLOOR  
1:50

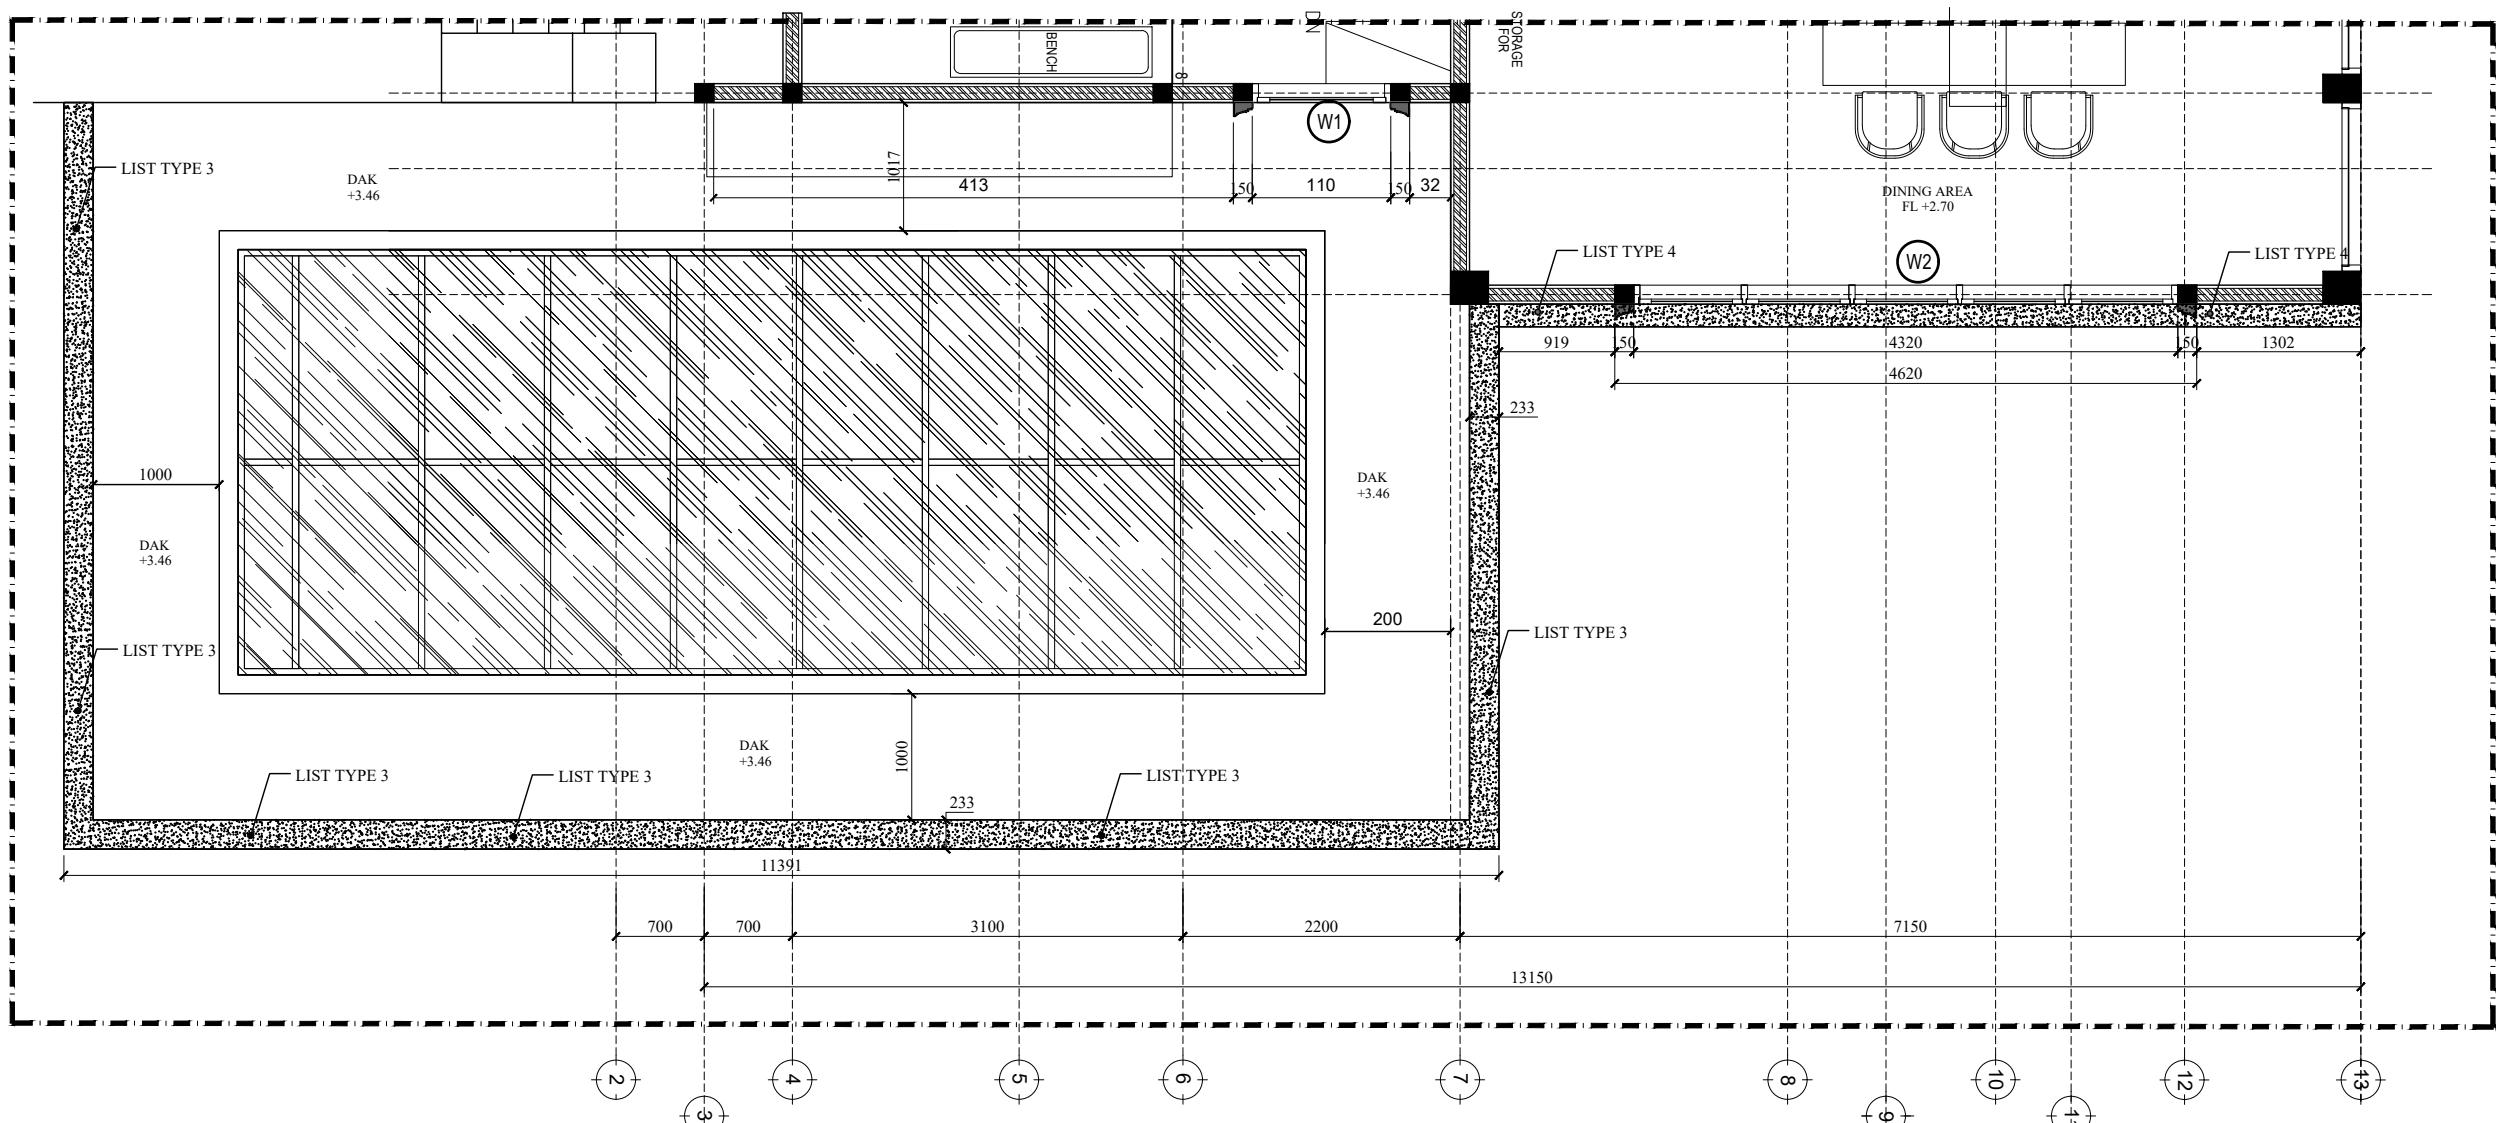

01 LAYOUT RIGHT PARTIAL FACADE 1ST FLOOR  
1:50