



NAMA PROYEK	RESIDENTIAL HOUSE AKASIA 2 / 59					
CATATAN :						
Semua detail, rencangan dan karya seni yang tertera pada gambar ini dibuat oleh Undang-undang Huk. Cipta, serta hanya boleh untuk yang telah ditentukan dan tidak boleh diperbaiki tanpa ijin tertulis. Kontak berikut untuk mengetahui dimensi terhadap keadaan lapangan dan apabila ada kelakuan yang harus disampaikan kepada Arsitek. Gambar berdimensi tidak diperkenankan diambil. Sebelum pekerjaan dilaksanakan, kontraktor berkewajiban untuk meminta persetujuan gambar kerja dan contoh bukti dari Arsitek.						
PEMBERI TUGAS						
ARSITEK						
ERIC HANDAYA, S.T I.A.I						
DRAFTING						
REVISI : _____						
NO. _____						
JUDUL GAMBAR :						
FOUNDATION DETAILS TYPE F1 FOUNDATION DETAILS TYPE F2						
SKALA : 1:100	DIGAMBAR	TGL.				
DIPERIKSA		TGL.				
DISETUJUI		TGL.				
DISETUJUI PEMB. TUGAS		TGL.	-			
DIKELUARKAN UNTUK : FOR DESIGN DEVELOPMENT						
NO. PROYEK	NO. GAMBAR :	KODE GAMBAR :	REVISI :			
	70	STR-03				

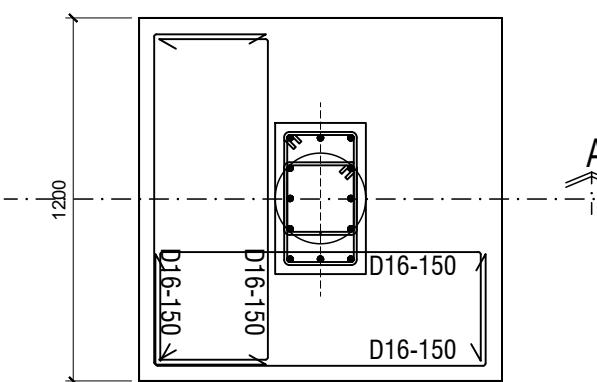


FOUNDATION DETAILS TYPE F1

SCALE 1:25

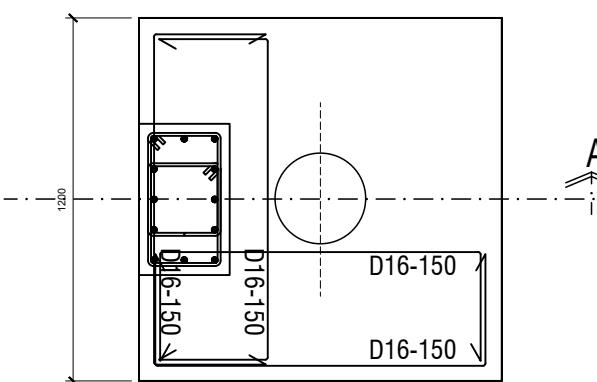

FOUNDATION DETAILS TYPE F2

SCALE 1:25

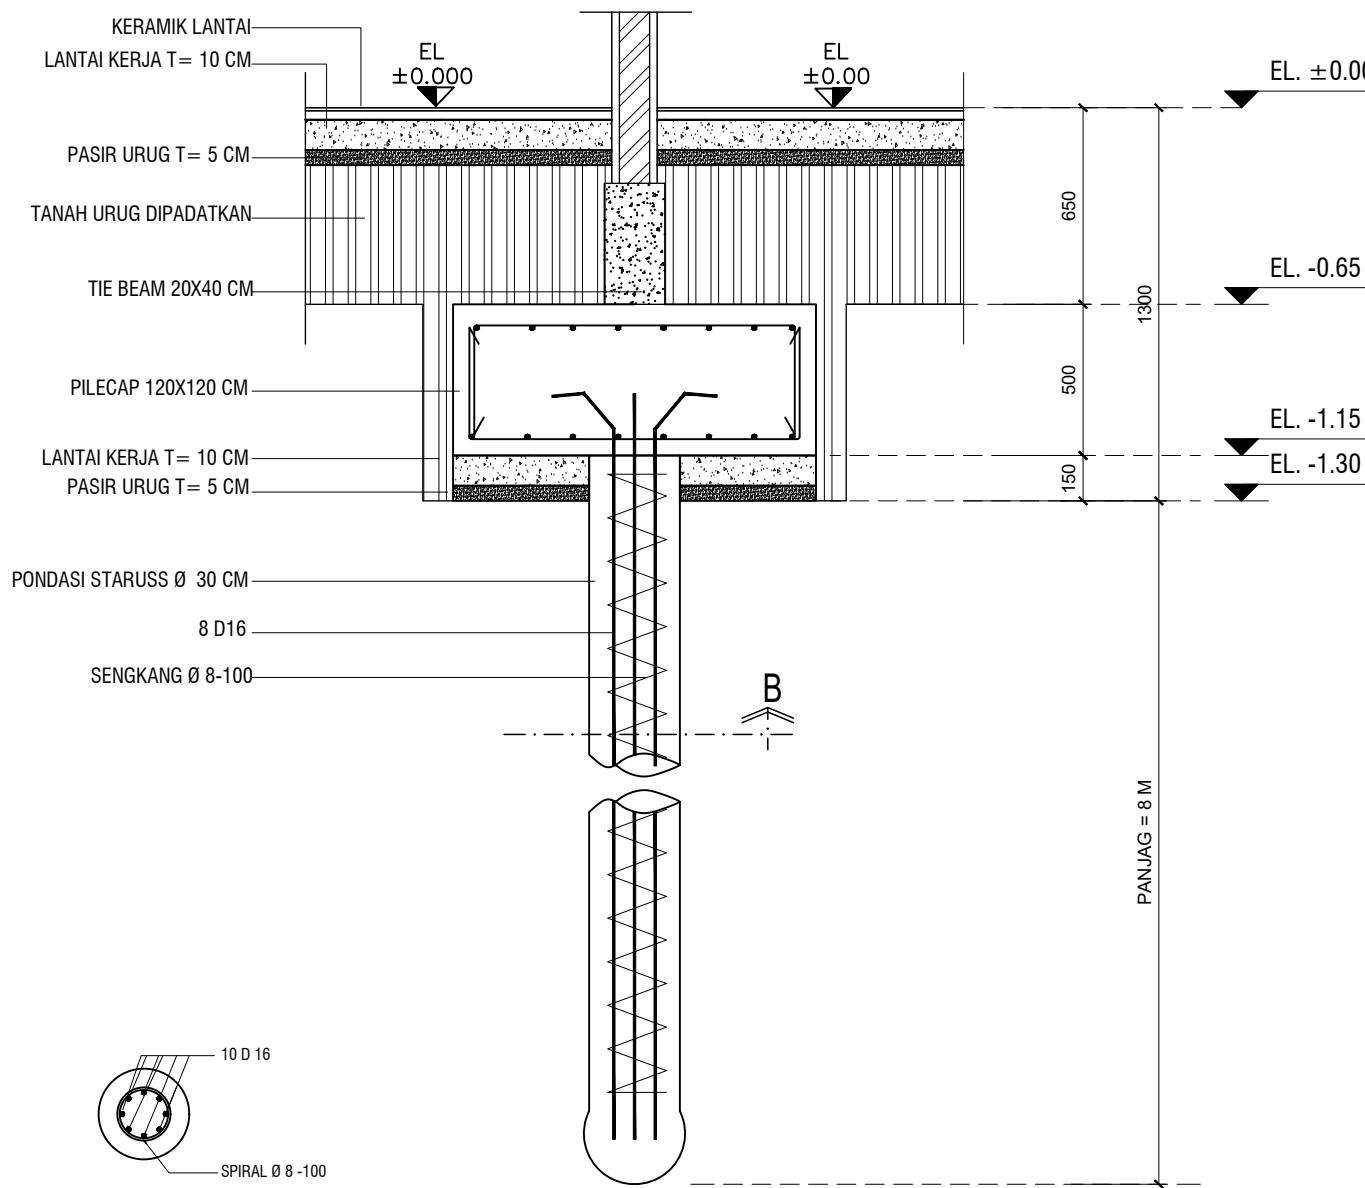


SECTION A

SCALE 1:25

SECTION A

SCALE 1:25

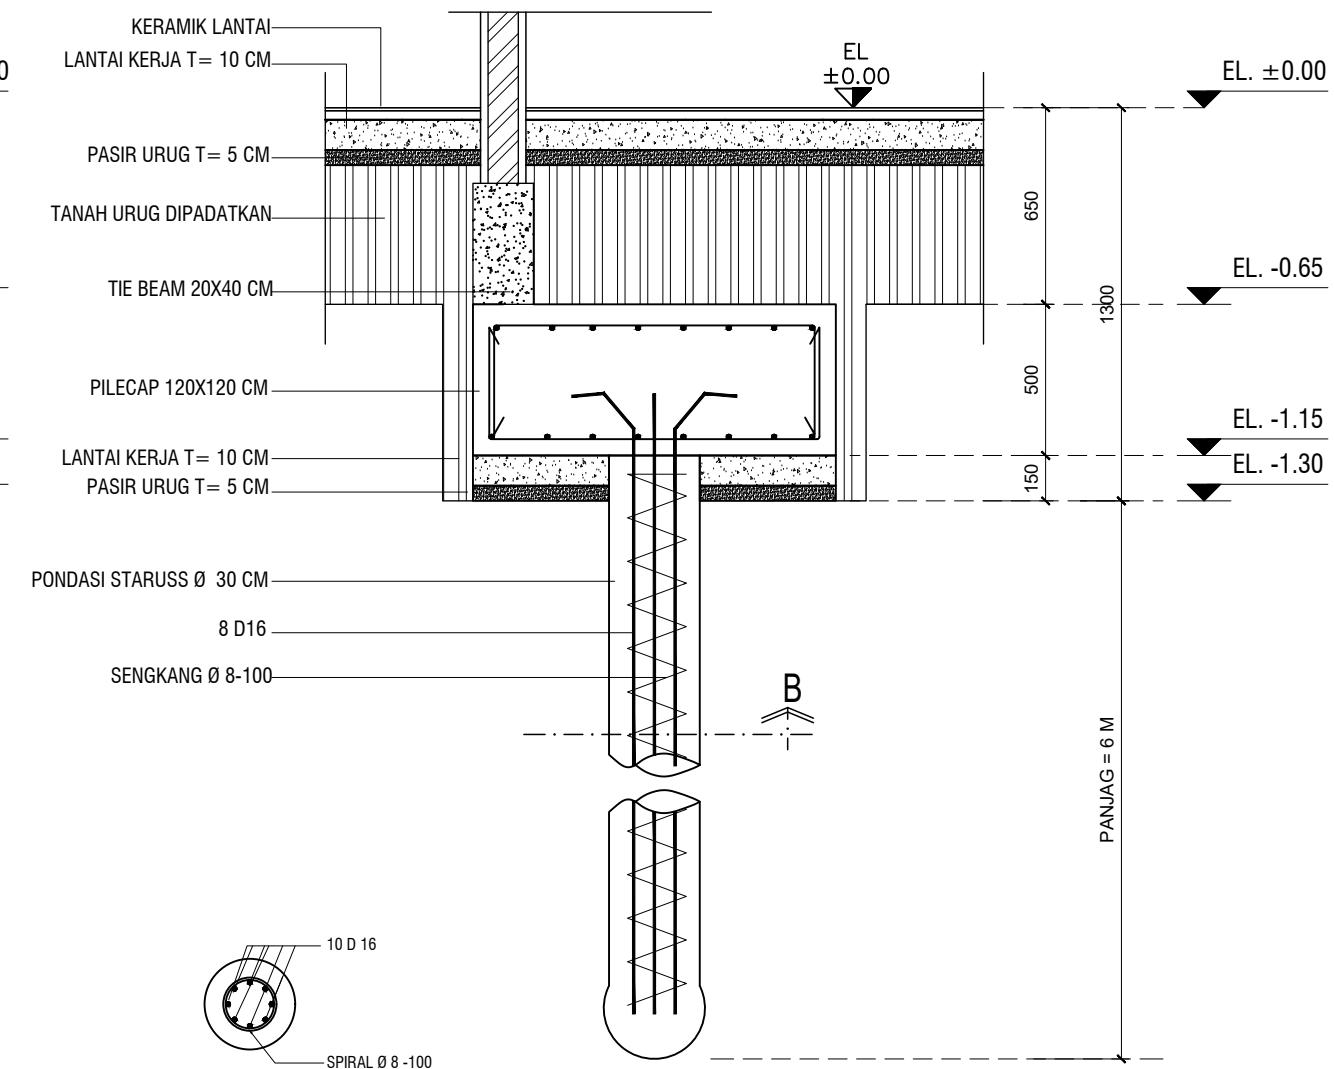

SECTION B

SCALE 1:25

SECTION A

SCALE 1:25