



Semen dahur, rancangan dan karya seni yang tertera pada gambar ini diilustrasi oleh Undang-undang Hak Cipta, serta hanya dapat untuk yang telah ditentukan dan tidak boleh diperbaiki dengan cara lain untuk memperoleh dimensi terhadap keadaan lapangan dan apabila ada kelakideckeran harus dilaporkan kepada Asetrik.
Gambar berdimensi tidak diperkenankan diskota.
Sebelum pekerjaan dilaksanakan, kontraktor berkewajiban untuk meminta persetujuan gambar kerja dan contoh bahan dari Asetrik.

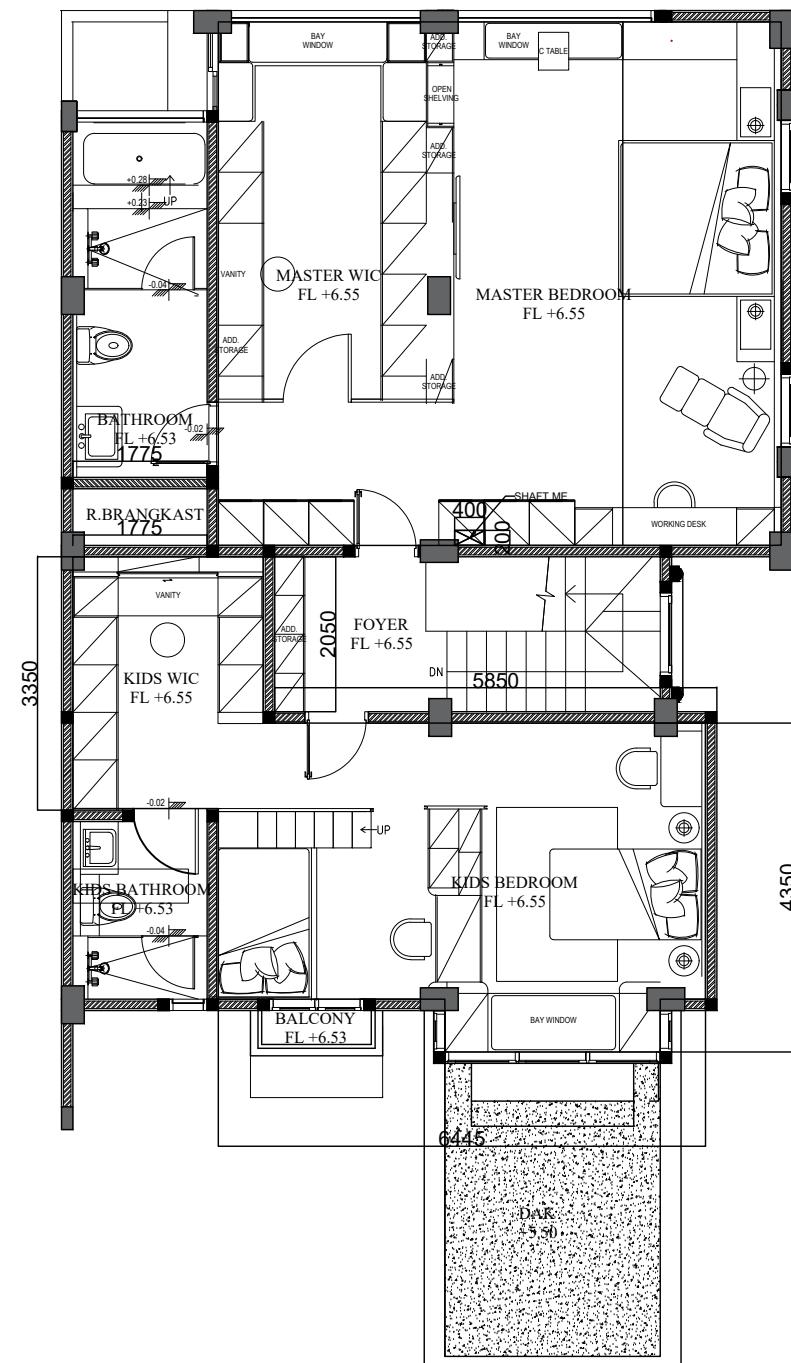

KIDS BEDROOM, KIDS WIC	33.23 M2
MASTER BEDROOM. MASTER WIC	51.55 M2

01 2ND FLOOR PLAN
1 : 100

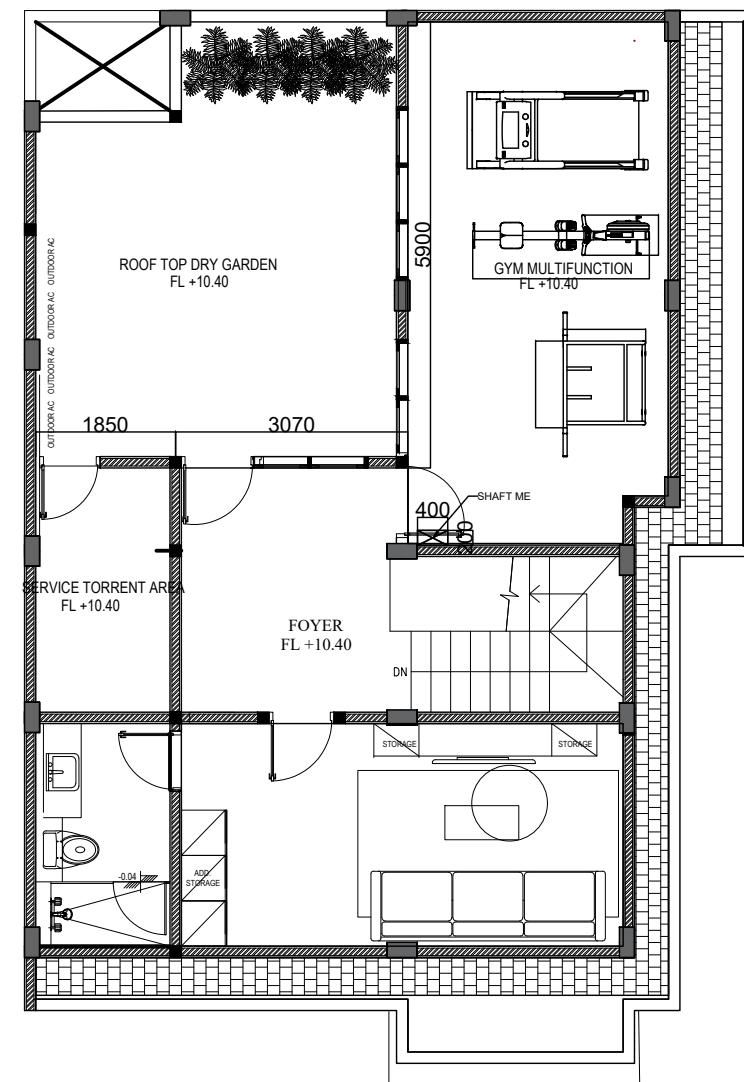

STUDIO	17.21 M2
MASTER BEDROOM. MASTER WIC	23.38 M2

01 3RD FLOOR PLAN
1 : 100

2nd AC PLAN
3rd AC PLAN

SKALA : 1:100	DIGAMBAR		TGL.
	DIPERIKSA		TGL.
	DISETUJUI		TGL.
DISETUJUI PEMB. TUGAS		TGL.	-
DIKELUARKAN UNTUK : FOR DESIGN DEVELOPMENT			
NO. PROYEK	NO. GAMBAR :	KODE GAMBAR :	REVISI :
	67	MEP-14	