


NAMA PROYEK		RESIDENTIAL HOUSE AKASIA 2 / 59			
CATATAN :		<p>Sama dengan rencana dan karya seni yang tertulis pada gambar ini dilindungi oleh Undang-undang Hukum Cipta, serta hanya diperbolehkan untuk yang telah ditentukan dan tidak boleh diperbanyak tanpa ijin tertulis.</p> <p>Kontrak berlaku sejak ditandatangani dan merupakan dimensi terhadap keadaan lapangan dan apabila ada ketidakcocokan harus disampaikan kepada Arsitek.</p> <p>Gambar berdimensi tidak diperkenankan diambil.</p> <p>Sebelum pengerjaan dimulai, kontraktor berkewajiban untuk meminta persetujuan gambar kerja dan contoh teknis dari Arsitek.</p>			
PEMBERI TUGAS					
ARSITEK		ERIC HANDAYA, S.T I.A.I			
DRAFTING					
JUDUL GAMBAR :		GROUND BEAM FLOOR PLAN			
SKALA :		DIGAMBAR		TGL.	
1:100					
DIPERIKSA				TGL.	
DISETUJUI				TGL.	
DISETUJUI PEMB. TUGAS				TGL.	-
DIKELUARKAN UNTUK :		FOR DESIGN DEVELOPMENT			
NO. PROYEK	NO. GAMBAR :	KODE GAMBAR :	REVISI :		
	72	STR-05			

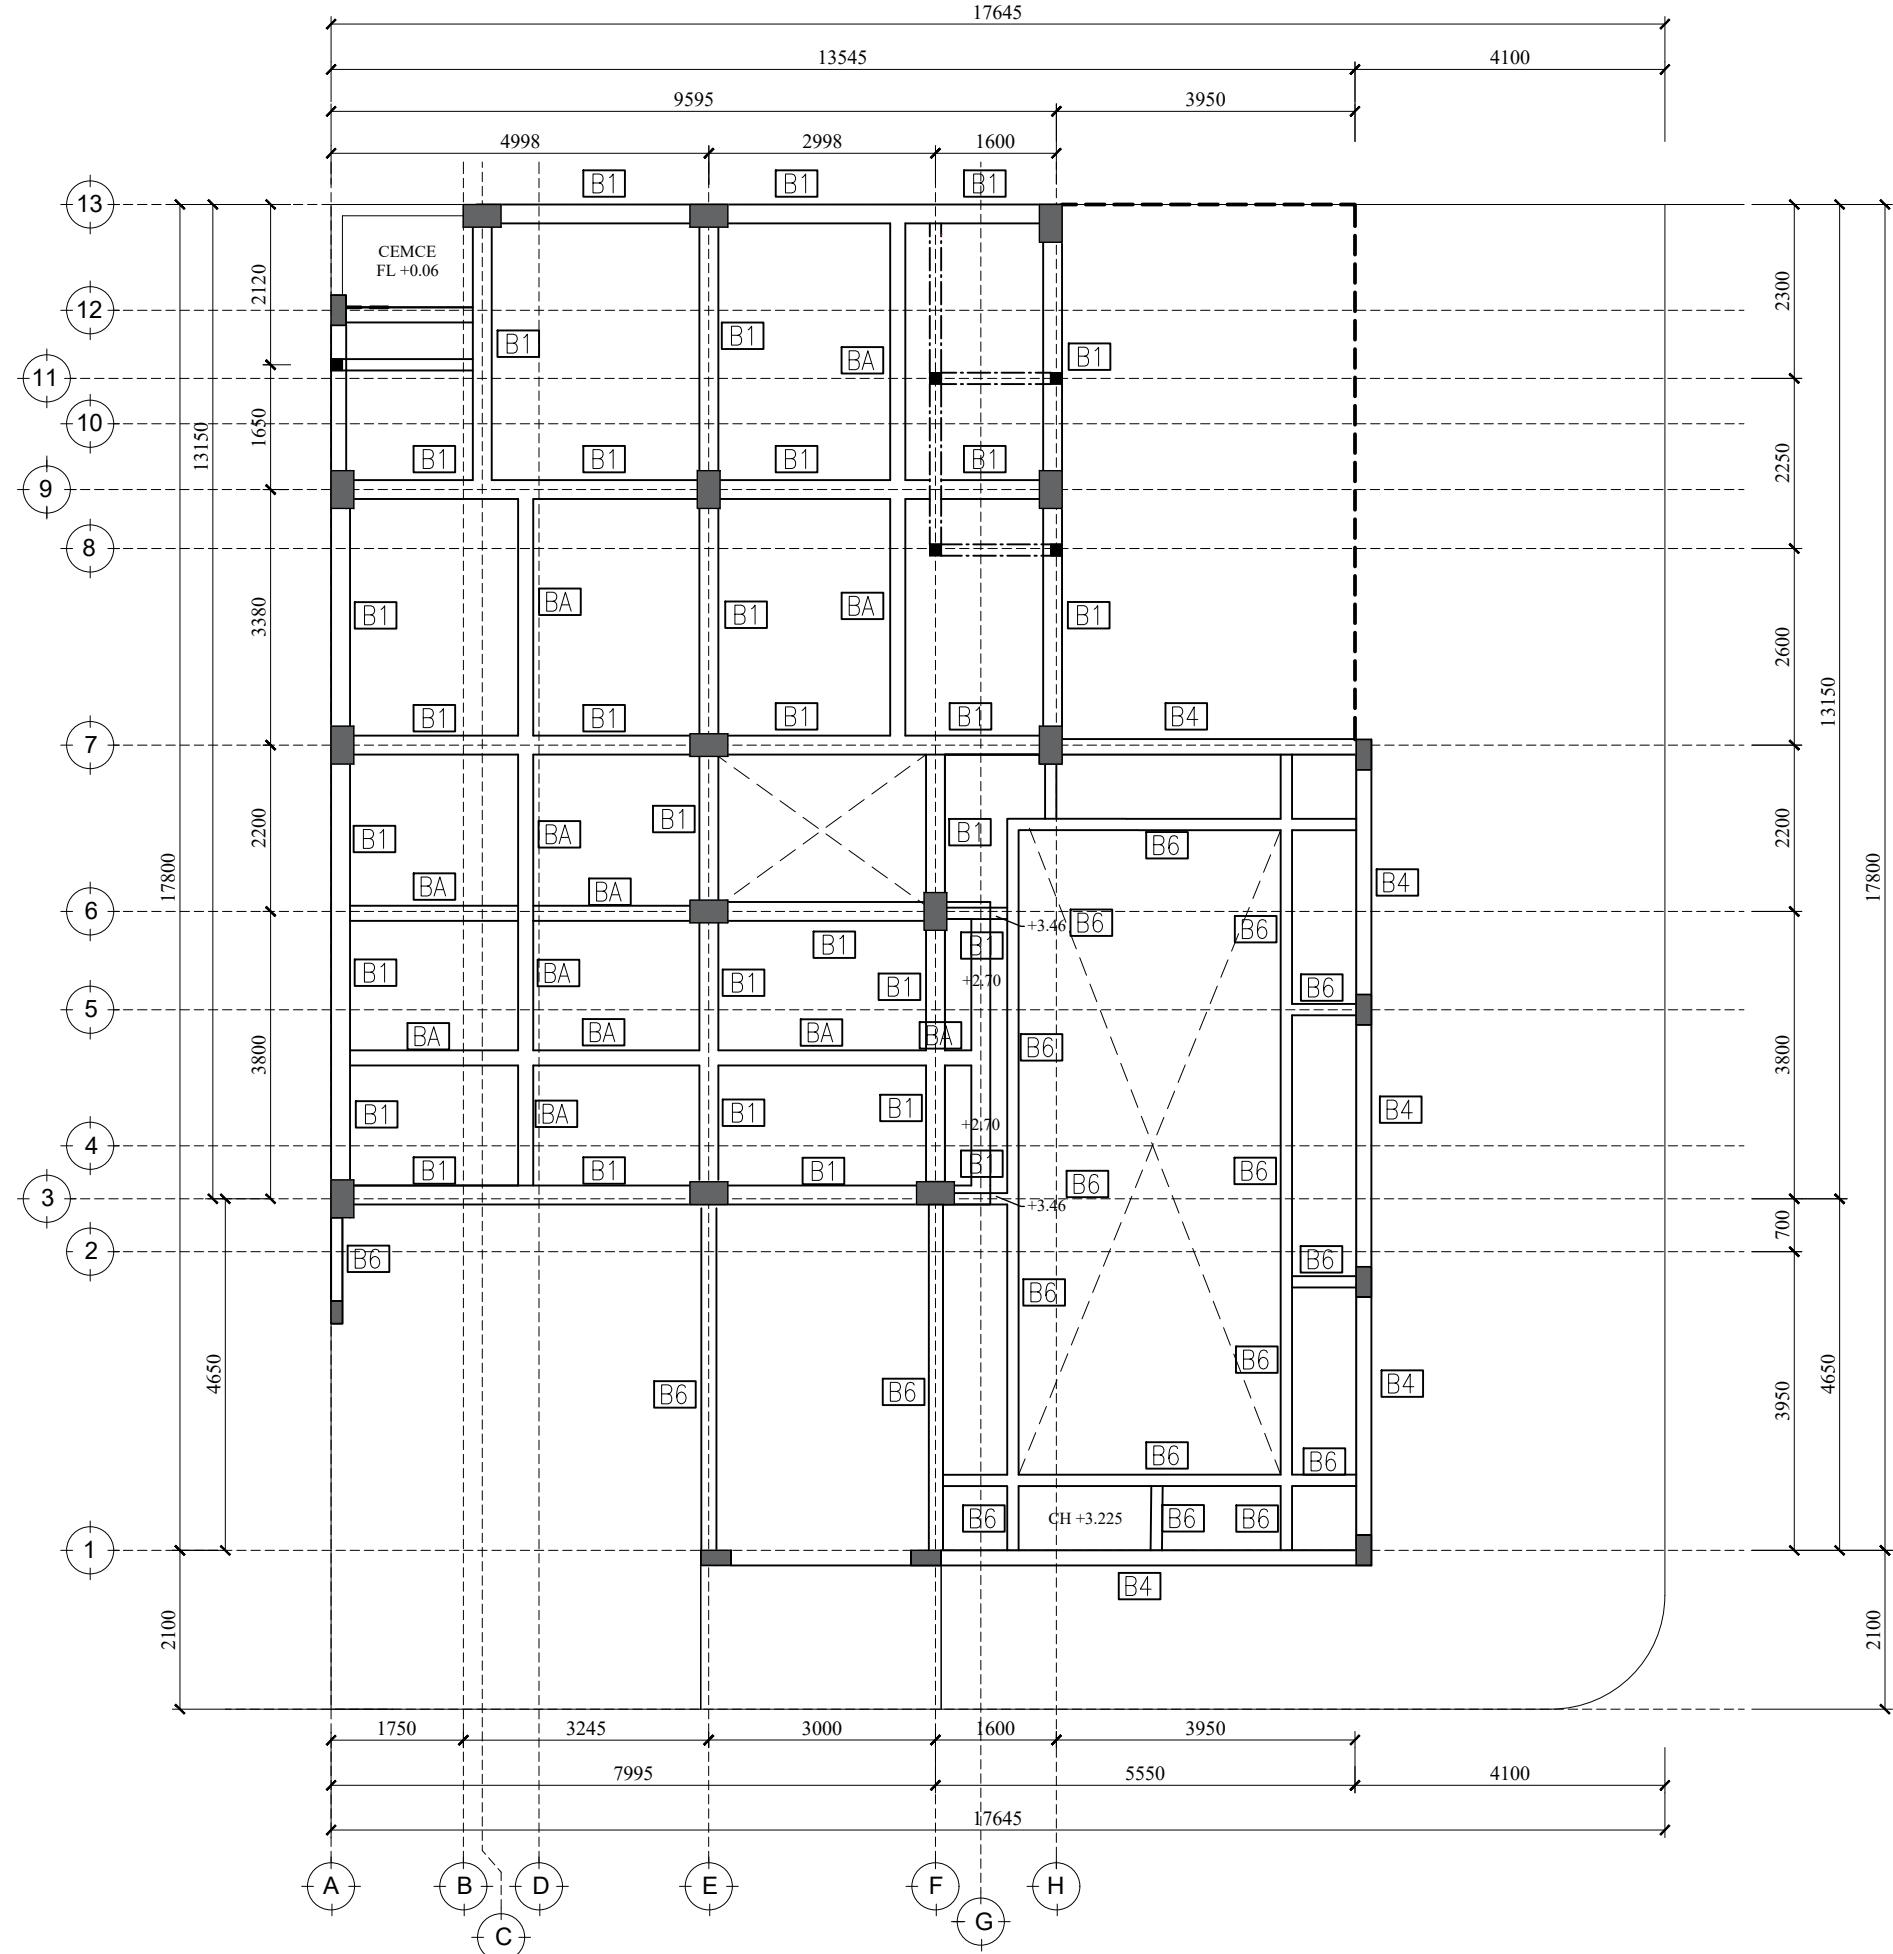

01 GROUND BEAM FLOOR PLAN  
1 : 100