
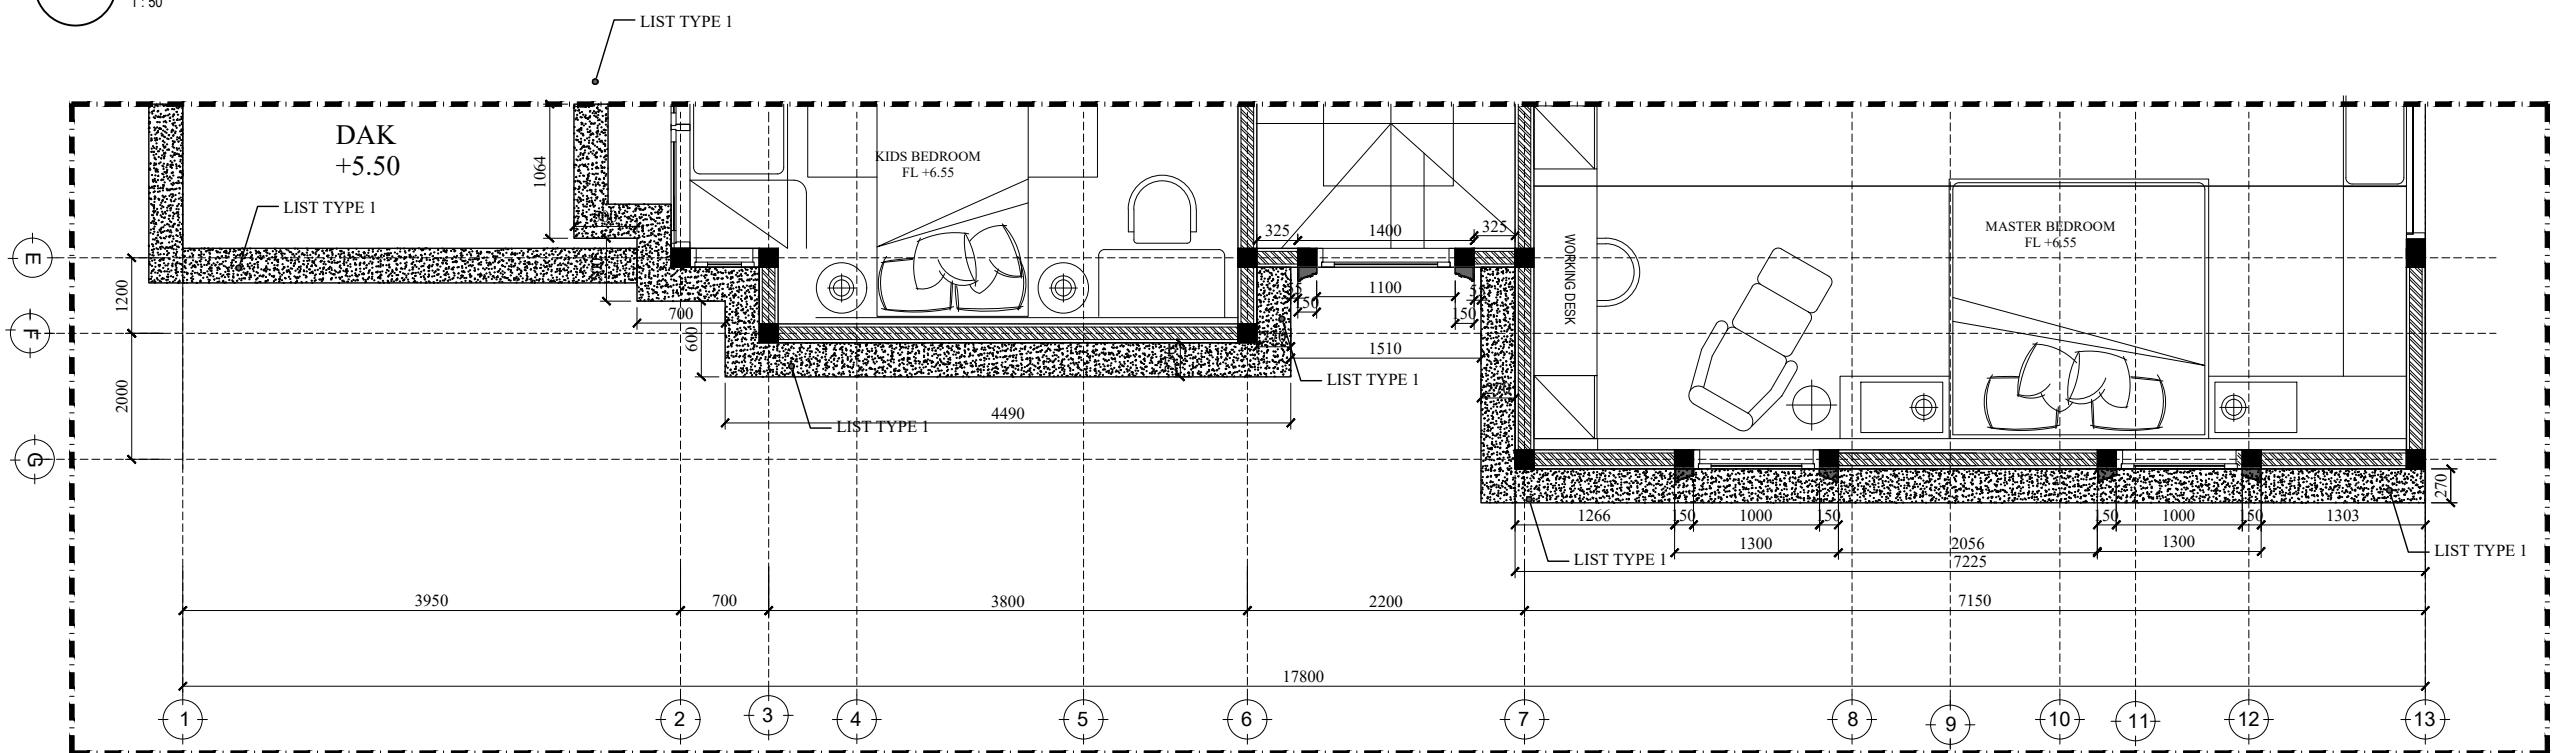


NAMA PROYEK	RESIDENTIAL HOUSE AKASIA 2 / 59					
CATATAN : Silakan dicatat, rencangan dan karya seni yang tertera pada gambar ini dibungkus dan diperbaiki tanpa [In] tertulis. Kontak kerja berjalan untuk memastikan dimensi terhadap keadaan lapangan dan apabila ada ketidakcocokan harus ditanyakan kepada Arsitek. Gambar berdimensi tidak diperkenankan diukur. Sebelum pekerjaan dilaksanakan, kontakter kerja berjalan untuk meminta persetujuan gambar kerja dan contoh bahan dari Arsitek.						
PEMBERI TUGAS						
ERIC HANDAYA, S.T I.A.I						
ARSITEK						
DRAFTING						
REVISI : _____						
TGL : _____						
NO. : _____						
JUDUL GAMBAR :						
LAYOUT FRONT PARSIAL FACADE 2ND FLOOR LAYOUT RIGHT PARTIAL FACADE 2ND FLOOR						
SKALA :	DIGAMBAR	TGL.				
1:50	DIPERIKSA	TGL.				
	DISETUJUI	TGL.				
DISETUJUI PEMB. TUGAS		TGL.	-			
DIKELUARKAN UNTUK : FOR DESIGN DEVELOPMENT						
NO. PROYEK	NO. GAMBAR :	KODE GAMBAR :	REVISI :			
	45	AR-45				

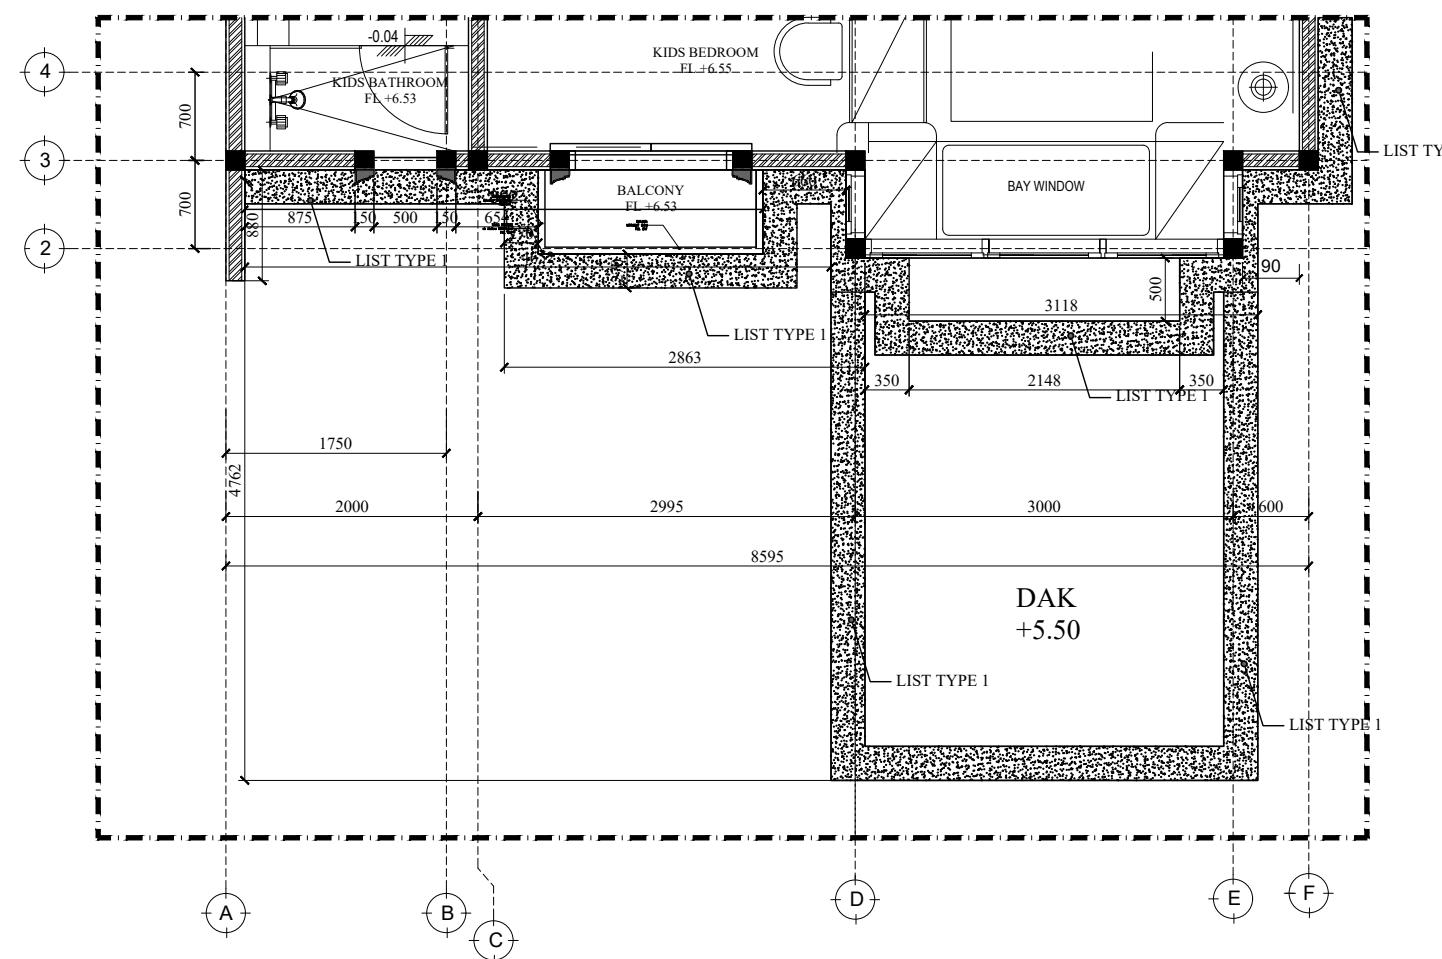

01 LAYOUT RIGHT PARTIAL FACADE 2ND FLOOR

1:50