


01 GROUND FLOOR PLAN

1 : 100

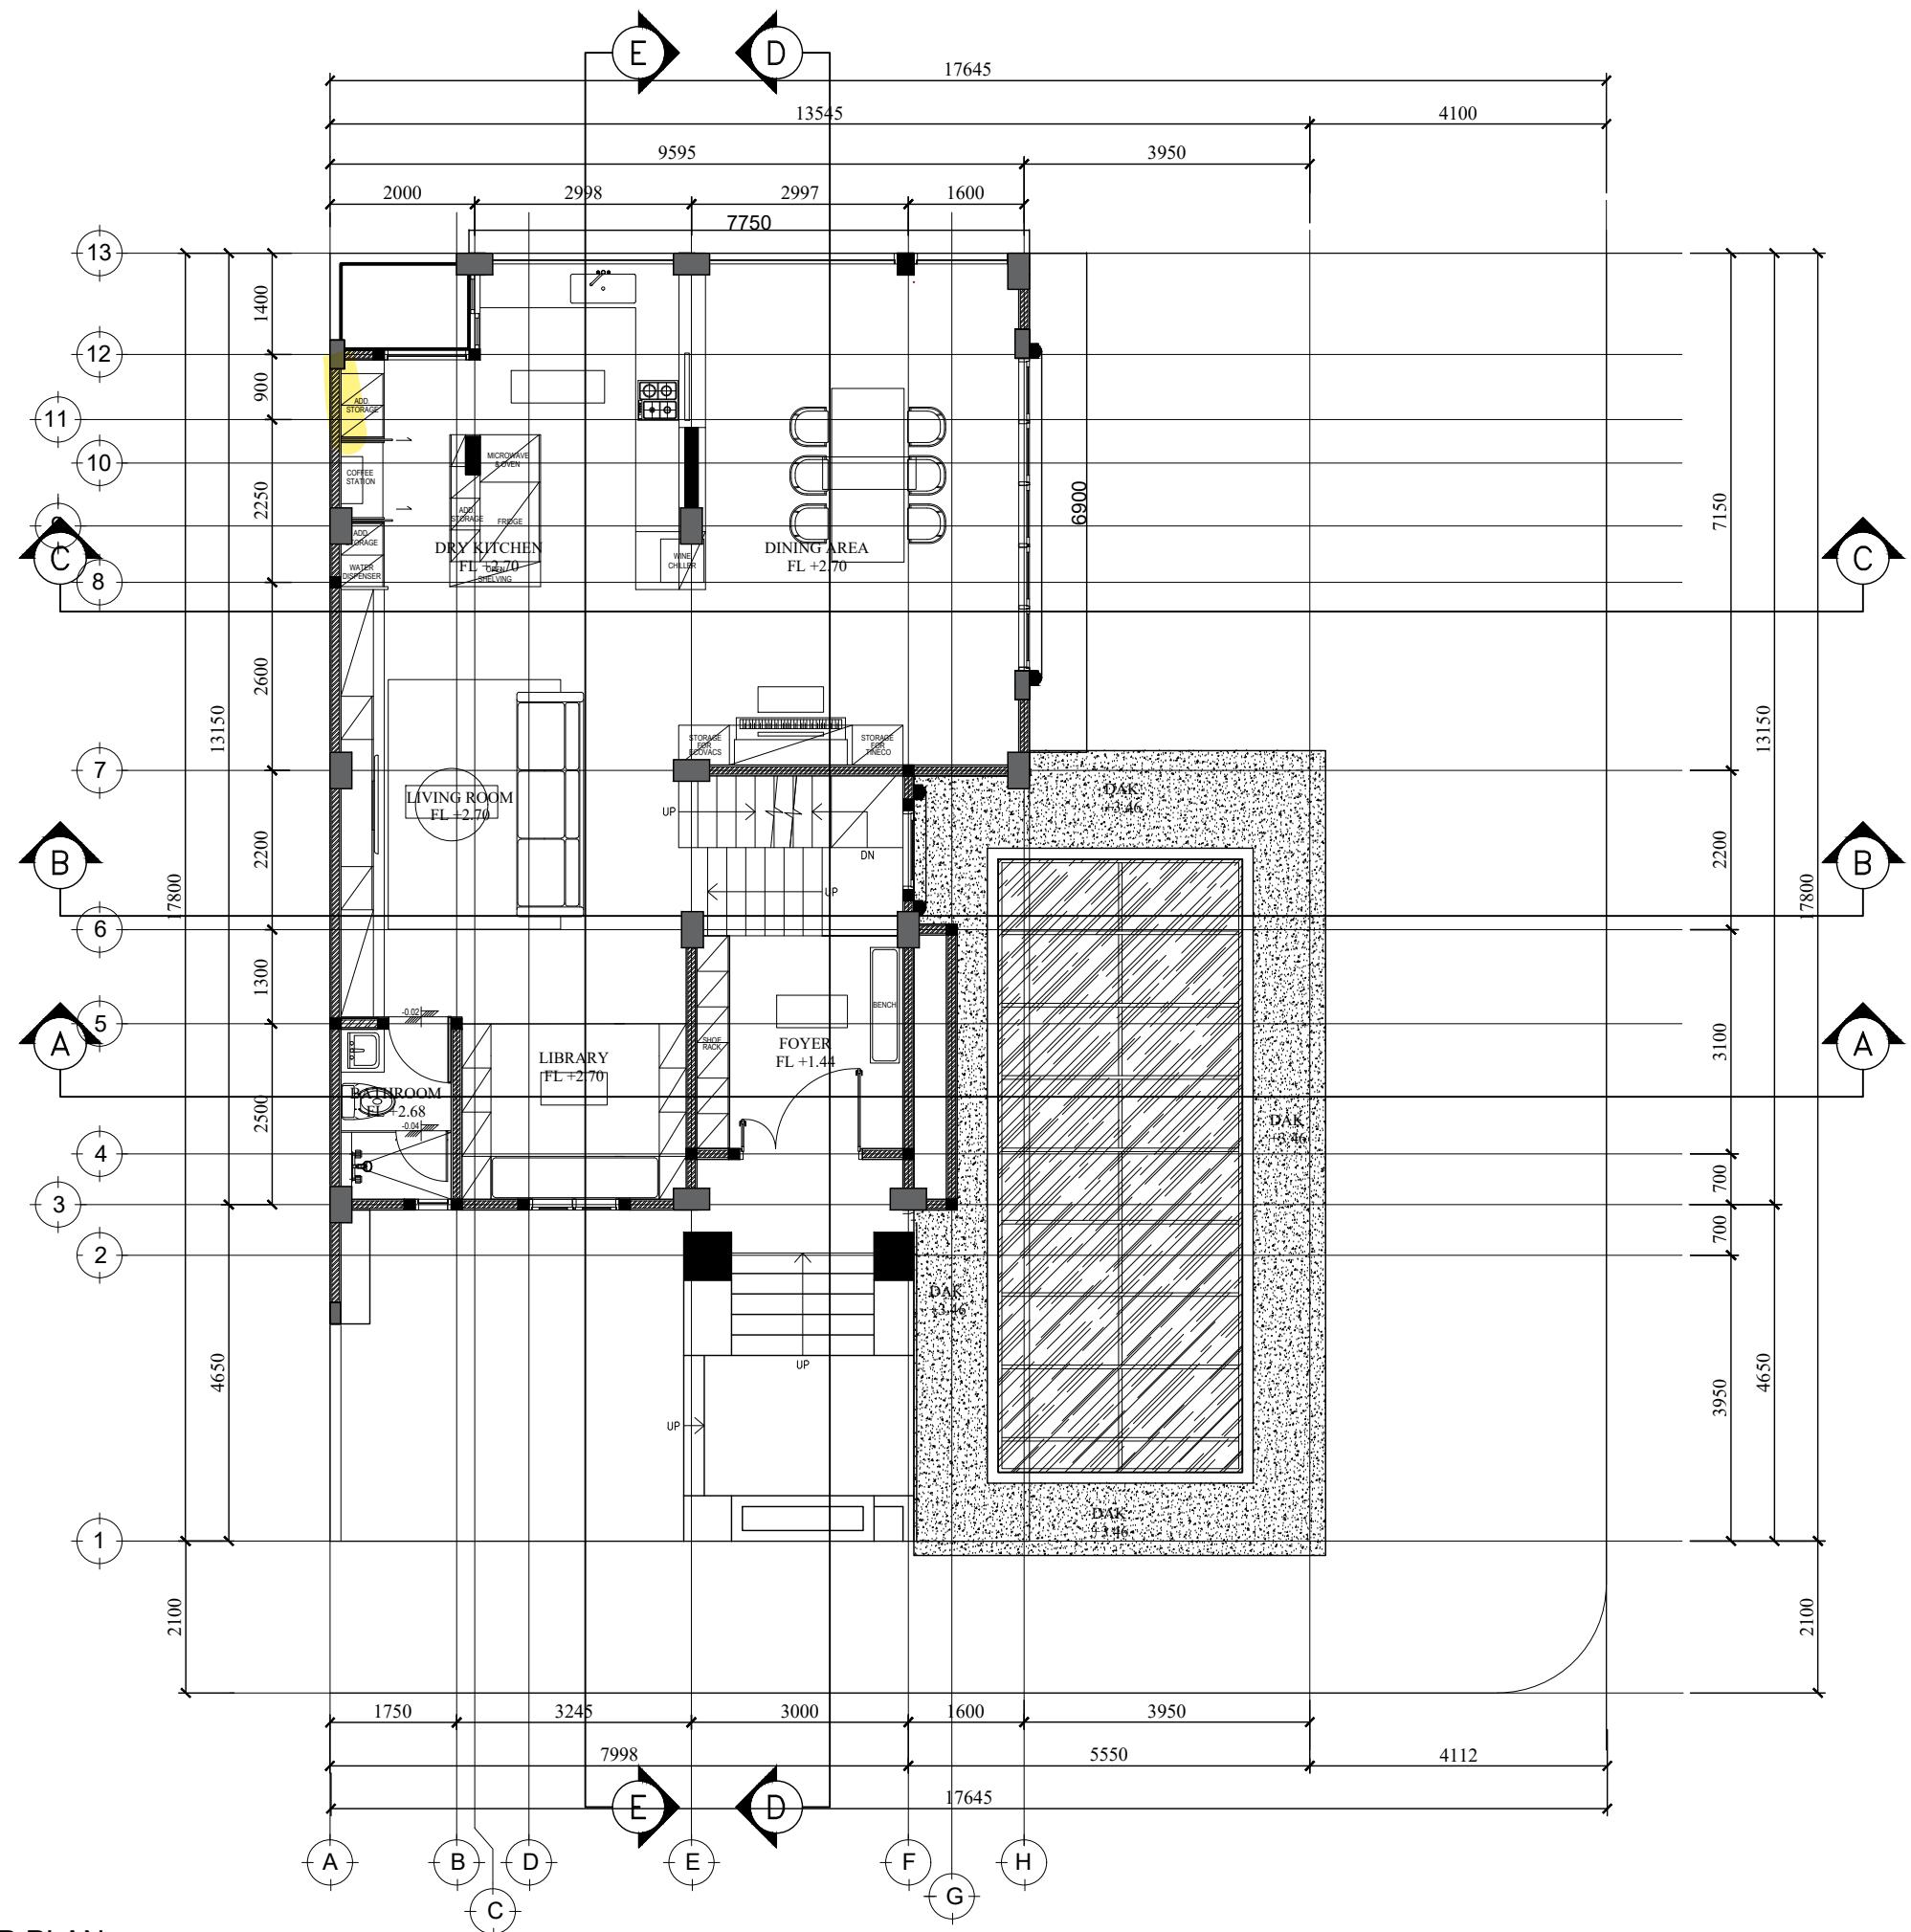

01 1ST FLOOR PLAN

1 : 100

0

NAMA PROYEK	RESIDENTIAL HOUSE AKASIA 2 / 59					
CATATAN : Semua garis, retangan dan lingkaran yang terdapat pada gambar ini dibungkus oleh Underlay yang berada di latar belakangnya. Untuk memunculkan dimensi terhadap keadaan lapangan dan apabila ada ketidaksesuaian dengan gambar ini, maka ketidaksesuaian tersebut dianggap benar. Gambar berdimensi tidak diperkenankan diskusi. Sebelum pekerjaan dilaksanakan, kontraktor berkerjasama untuk meminta persetujuan gambar kerja dan contoh bahan dari Arsitek.						
PEMBERI TUGAS						
ARSITEK						
ERIC HANDAYA, S.T I.A.I						
DRAFTING						
REVISI : _____						
NO. : _____						
JUDUL GAMBAR :						
2ND FLOOR PLAN ROOFTOP FLOOR PLAN						
SKALA : 1:100						
DIGAMBAR	TGL.					
DIPERIKSA	TGL.					
DISETUJUI	TGL.					
DISETUJUI PEMB. TUGAS	TGL.	-				
DIKELUARKAN UNTUK : FOR DESIGN DEVELOPMENT						
NO. PROYEK	NO. GAMBAR :	KODE GAMBAR :	REVISI :			
	03	AR-03				

