


NO. PROTER	NO. GRABER :	RODE GRABER :	REVISI :
	01	AR-01	

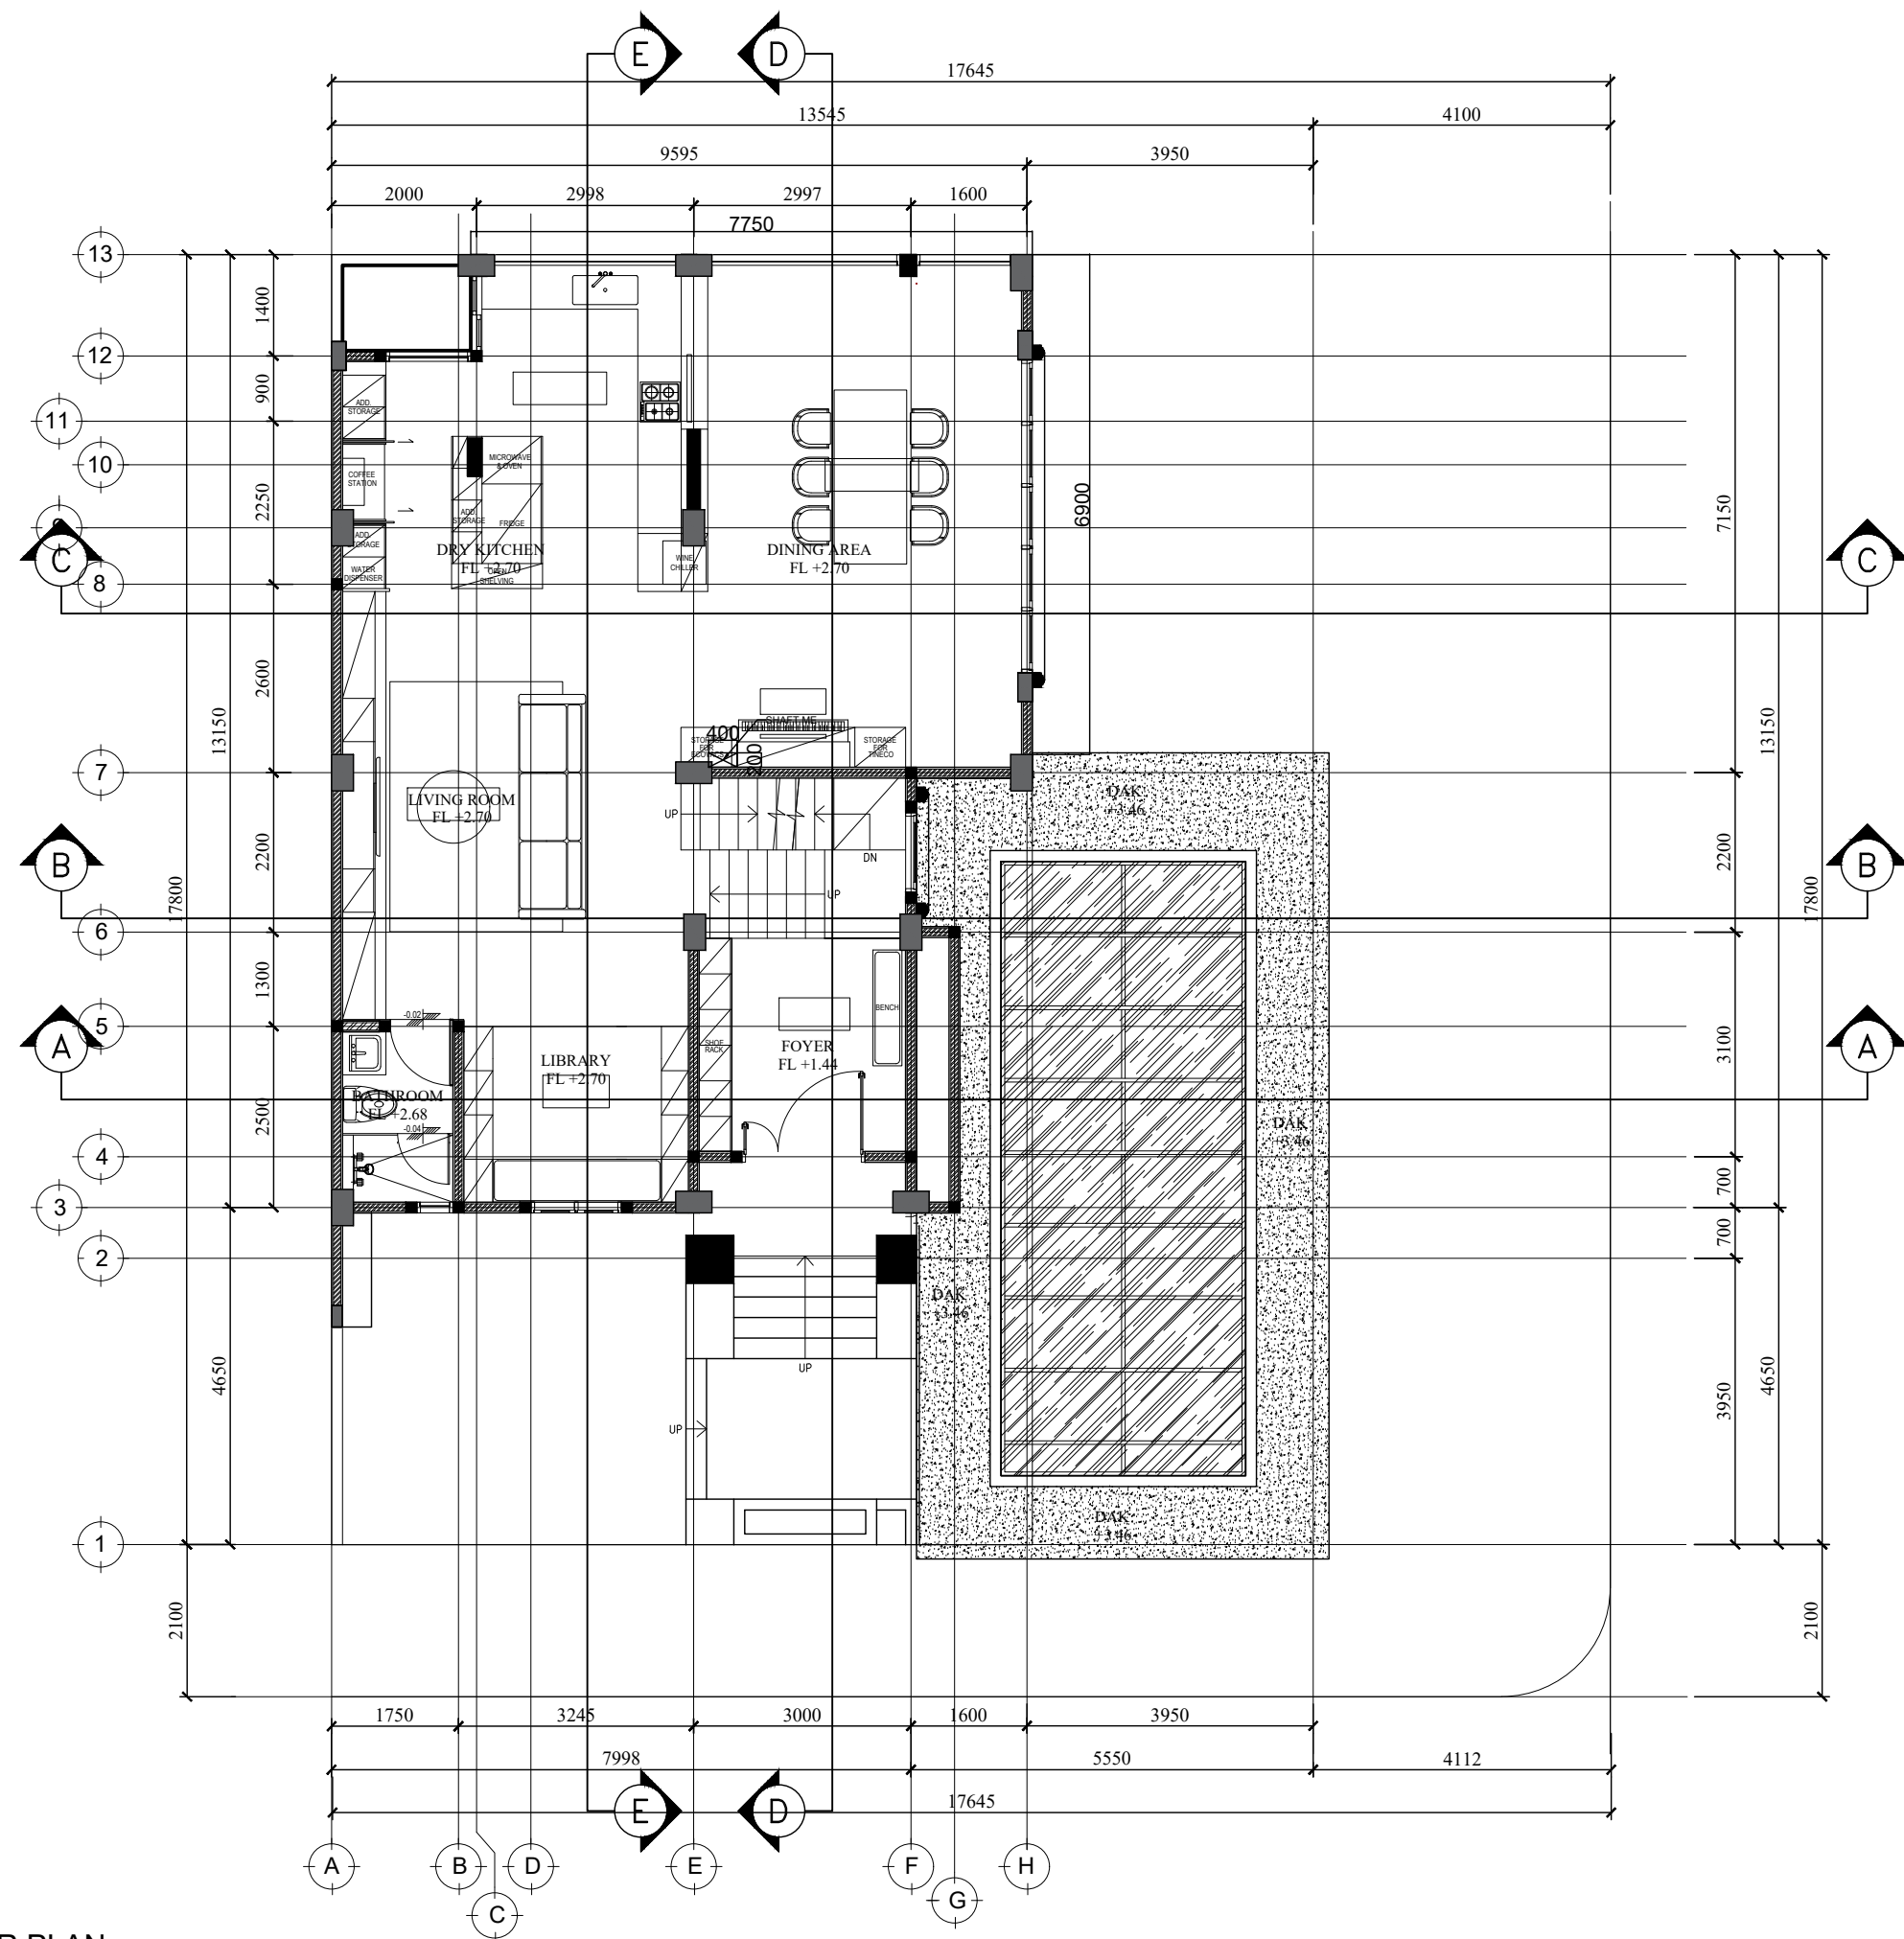

01 1ST FLOOR PLAN  
1: 100

NAMA PROYEK			
RESIDENTIAL HOUSE AKASIA 2 / 59			
CATATAN :			
Semua detail, rancangan dan karya seni yang tertera pada gambar ini dilindungi oleh Undang-undang Hak Cipta, serta hanya dipakai untuk yang telah ditentukan dan tidak boleh diperbanyak tanpa izin tertulis. Kontraktor berkewajiban untuk memeriksa dimensi terhadap keadaan lapangan dan apabila ada ketidakakuratan harus dilaporkan kepada Arsitek. Gambar berdimensi tidak diperkenankan dikopi. Sebelum pekerjaan dilaksanakan, kontraktor berkewajiban untuk meminta persetujuan gambar kerja dan contoh bahan dari Arsitek.			
PEMBERI TUGAS			
ARSITEK			
ERIC HANDAYA, S.T I.A.I			
DRAFTING			
			TDT
			R E V I S I
			TGL
			NO.
JUDUL GAMBAR :			
1ST FLOOR PLAN			
SKALA :			
1:100	DIGAMBAR		TGL.
	DIPERIKSA		TGL.
	DISETUJUI		TGL.
DISETUJUI PEMB. TUGAS			TGL. -
DIKELUARKAN UNTUK : FOR DESIGN DEVELOPMENT			
NO. PROYEK	NO. GAMBAR :	KODE GAMBAR :	REVISI :
	02	AR-02	



SKALA :  <div style="text-align: center; font-size: 2em;">1:100</div>	DIGAMBAR		TGL.	
	DIPERIKSA		TGL.	
	DISETUJUI		TGL.	
DISETUJUI PEMB. TUGAS			TGL.	—
DIKELUARKAN UNTUK :                      FOR DESIGN DEVELOPMENT				
NO. PROYEK	NO. GAMBAR :	KODE GAMBAR :	REVISI :	
	03		AR-03	