



NAMA PROYEK	RESIDENTIAL HOUSE AKASIA 2 / 59		
CATATAN :	Simpan detail, rencangan dan karya seni yang tertulis pada gambar ini di dalam dan Undang-undang Hukum Cipta, serta hanya diperbolehkan untuk yang telah ditentukan dan tidak boleh diperbaiki tanpa izin tertulis. Kompleksitas teknis dalam teknologi dimana terhadap keadaan lapangan dan apabila ada ketidakcocokan harus disampaikan kepada Arsitek. Gambar berdimensi tidak diperkenankan diakses. Sebelum pengerjaan dilaksanakan, kontraktor berkewajiban untuk meminta persetujuan gambar kerja dan contoh buah dari Arsitek.		
PEMBERI TUGAS			
ARSITEK	ERIC HANDAYA, S.T I.A.I		
DRAFTING			
TGL			
REVISI			
NO.	TOL		
JUDUL GAMBAR :			
TIE BEAM PLAN			
SKALA :	DIGAMBAR		TGL.
1:100			
DIPERIKSA		TGL.	
DISETUJUI		TGL.	
DISETUJUI PEMB. TUGAS		TGL.	-
FOR DESIGN DEVELOPMENT			
NO. PROYEK	NO. GAMBAR :	KODE GAMBAR :	REVISI :
	69	STR-02	

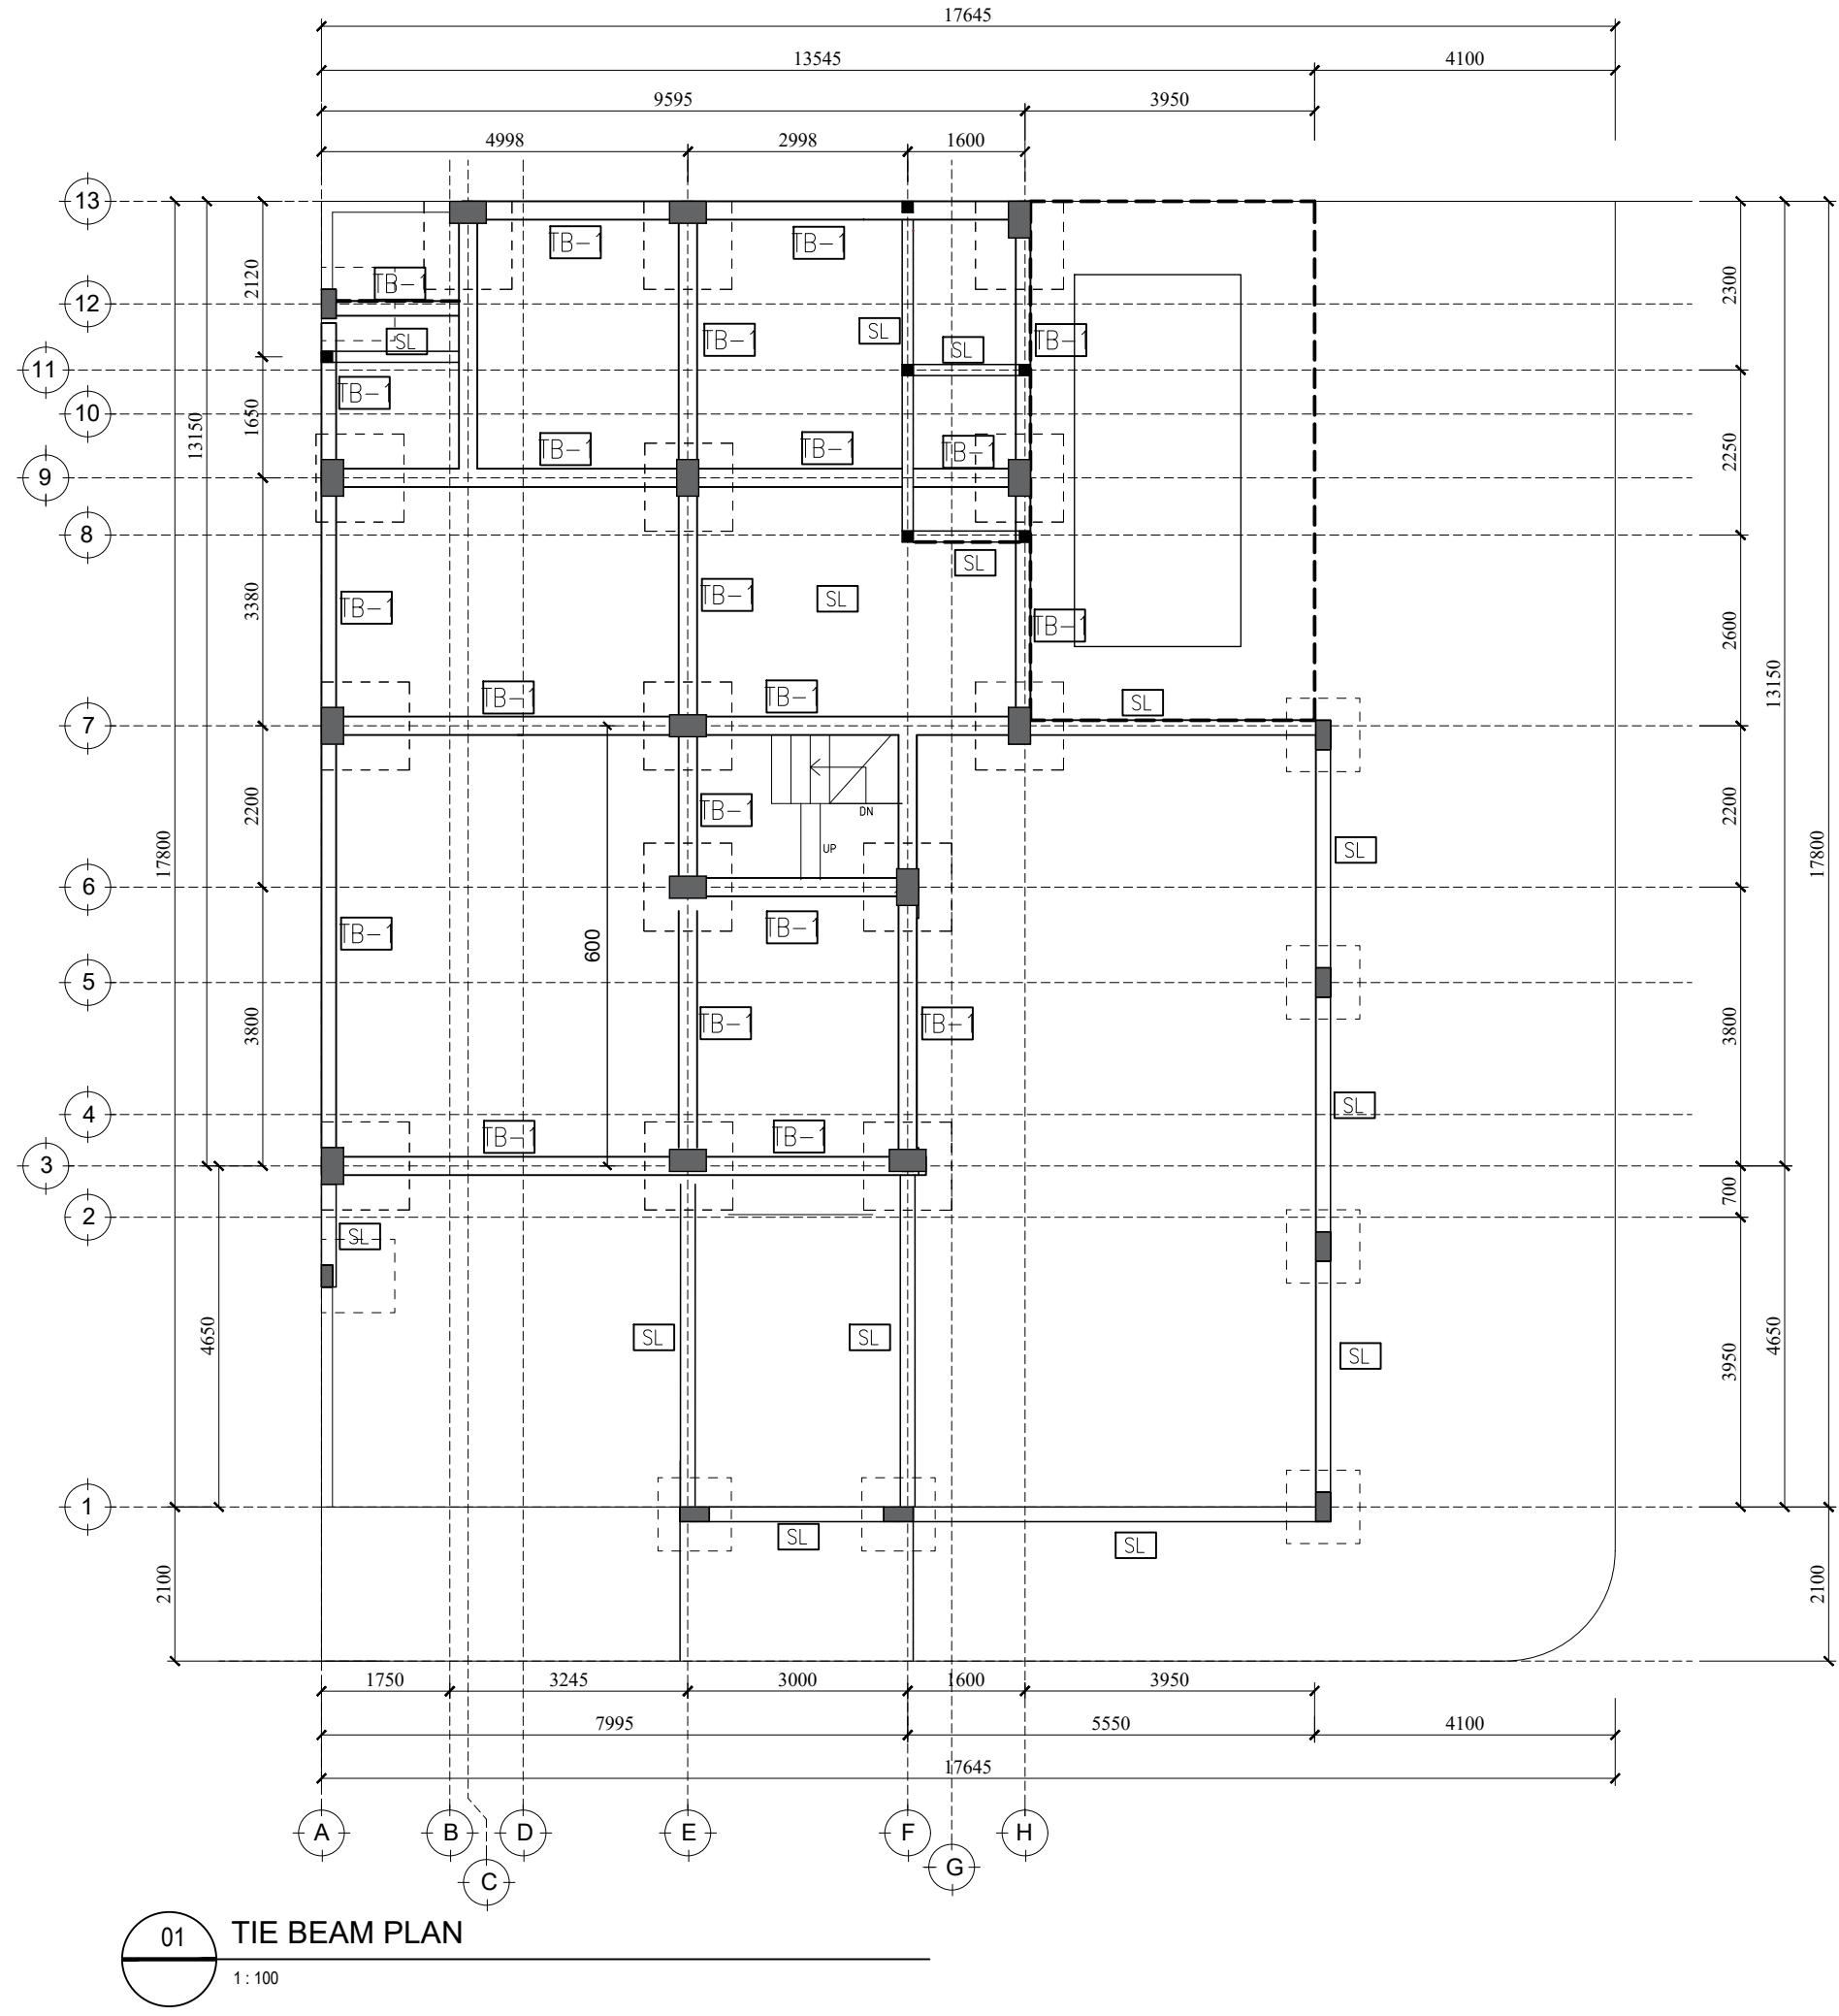


NAMA PROYEK	RESIDENTIAL HOUSE AKASIA 2 / 59					
CATATAN :						
Semua detail, rencangan dan karya seni yang tertera pada gambar ini dibuat oleh Undang-undang Huk. Cipta, serta hanya boleh untuk yang telah ditentukan dan tidak boleh diperbaiki tanpa ijin tertulis. Kontak berikut untuk mengetahui dimensi terhadap keadaan lapangan dan apabila ada kelakuan yang harus disampaikan kepada Arsitek. Gambar berdimensi tidak diperkenankan diambil. Sebelum pekerjaan dilaksanakan, kontraktor berkewajiban untuk meminta persetujuan gambar kerja dan contoh bukti dari Arsitek.						
PEMBERI TUGAS						
ARSITEK						
ERIC HANDAYA, S.T I.A.I						
DRAFTING						
REVISI : _____						
NO. _____						
JUDUL GAMBAR :						
FOUNDATION DETAILS TYPE F1 FOUNDATION DETAILS TYPE F2						
SKALA : 1:100	DIGAMBAR	TGL.				
DIPERIKSA		TGL.				
DISETUJUI		TGL.				
DISETUJUI PEMB. TUGAS		TGL.	-			
DIKELUARKAN UNTUK : FOR DESIGN DEVELOPMENT						
NO. PROYEK	NO. GAMBAR :	KODE GAMBAR :	REVISI :			
	70	STR-03				

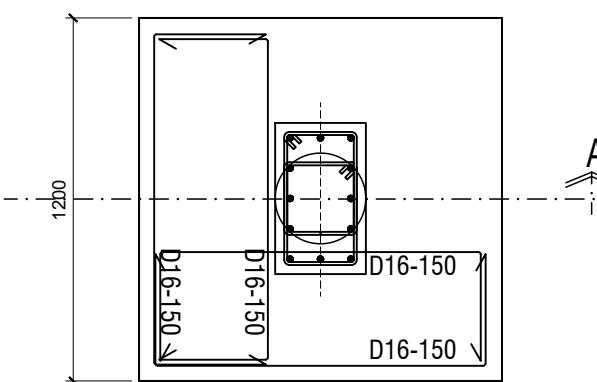


FOUNDATION DETAILS TYPE F1

SCALE 1:25

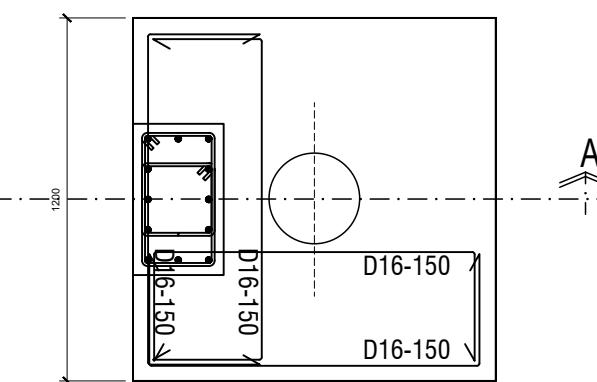

FOUNDATION DETAILS TYPE F2

SCALE 1:25

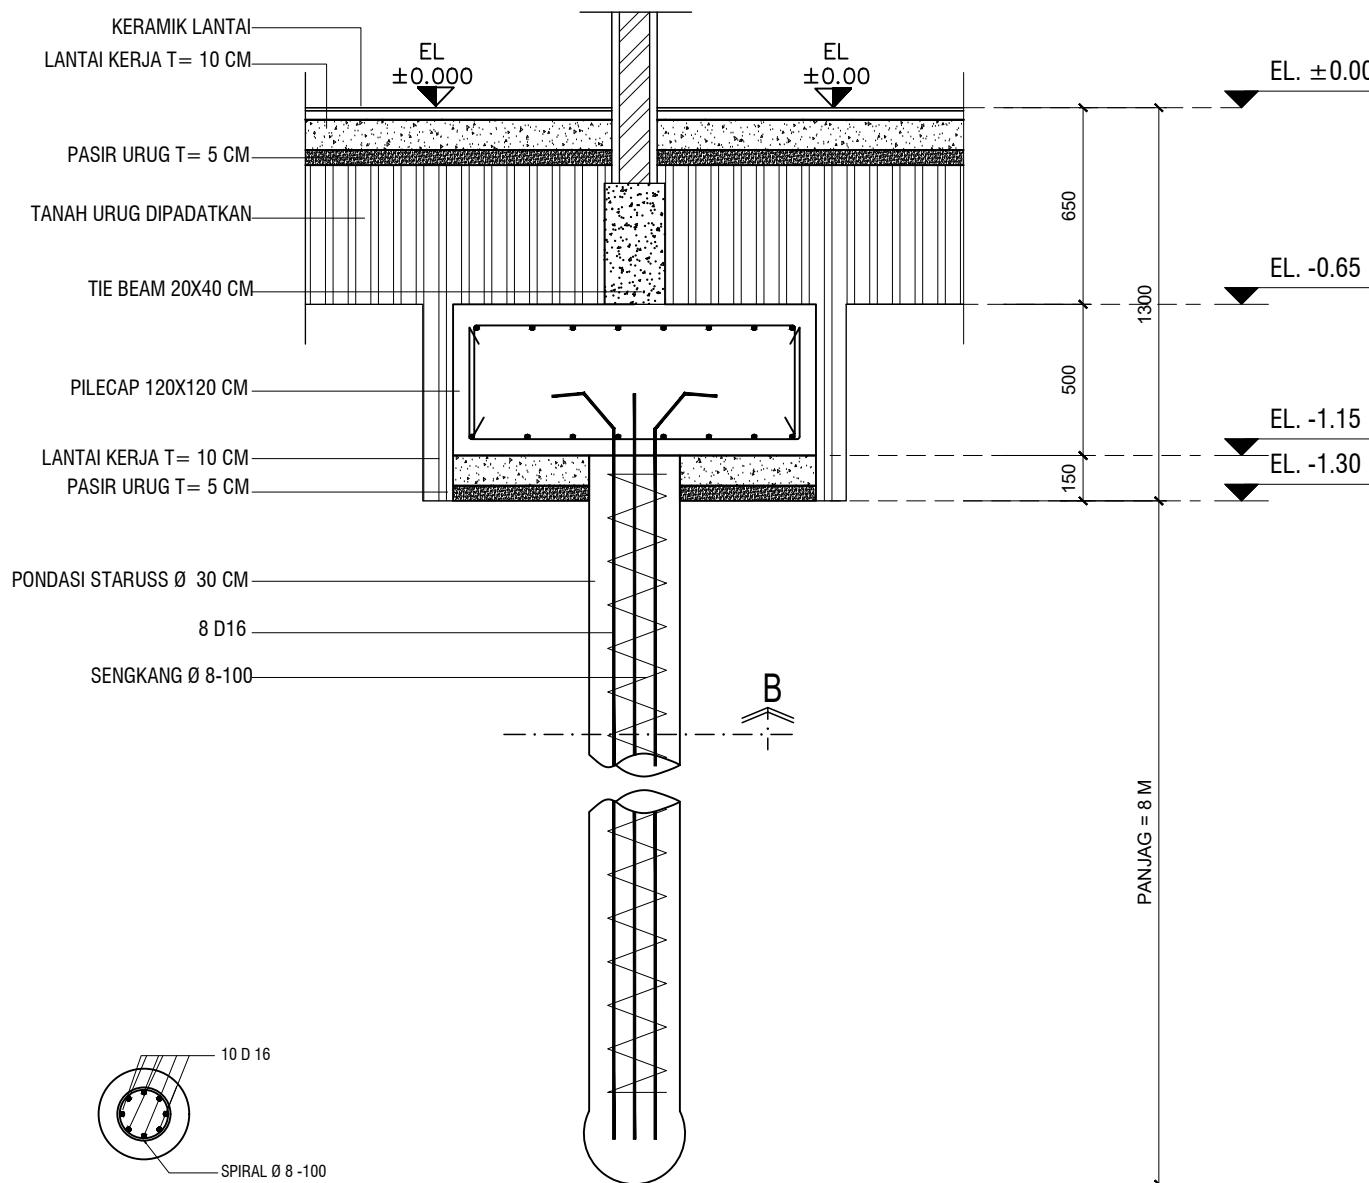


SECTION A

SCALE 1:25

SECTION A

SCALE 1:25

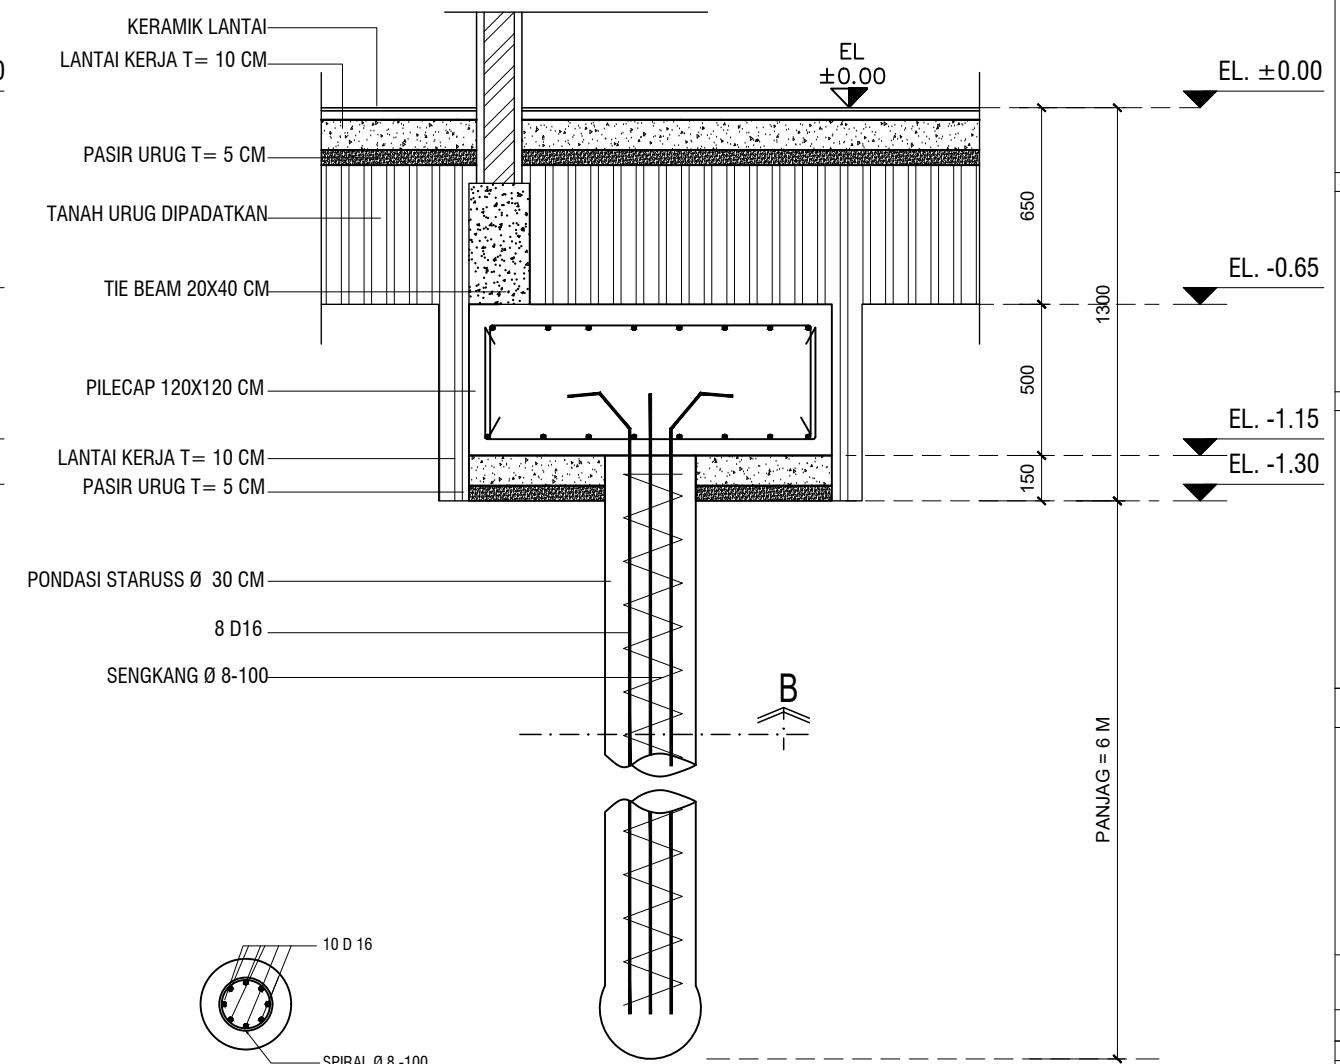


SECTION B

SCALE 1:25


SECTION A

SCALE 1:25


NAMA PROYEK	RESIDENTIAL HOUSE AKASIA 2 / 59		
CATATAN :	<p>Semua detail, rencangan dan karya seni yang tertera pada gambar ini diilustrasi dan diterangkan oleh Arsitek, serta hanya diperlukan untuk yang telah ditentukan dan tidak boleh diperbaiki tanpa ijin tertulis.</p> <p>Kontrak berlaku setelah memahami dimensi terhadap keadaan lapangan dan apabila ada ketidaksesuaian harus disampaikan kepada Arsitek.</p> <p>Gambar berdimensi tidak diperkenankan diakali.</p> <p>Sebelum pengerjaan dilaksanakan, kontraktor berkewajiban untuk meminta persetujuan gambar kerja dan contoh bukti dari Arsitek.</p>		
PEMBERI TUGAS			
ARSITEK			
ERIC HANDAYA, S.T I.A.I			
DRAFTING			
REVISI			
TGL			
NO.			
JUDUL GAMBAR :			
FOUNDATION DETAILS TYPE F3			
FOUNDATION DETAILS TYPE F4			
SKALA : 1:25	DIGAMBAR	TGL.	
DIPERIKSA		TGL.	
DISETUJUI		TGL.	
DIKELUARKAN UNTUK :	FOR DESIGN DEVELOPMENT		
NO. PROYEK	NO. GAMBAR :	KODE GAMBAR :	REVISI :
	71	STR-04	

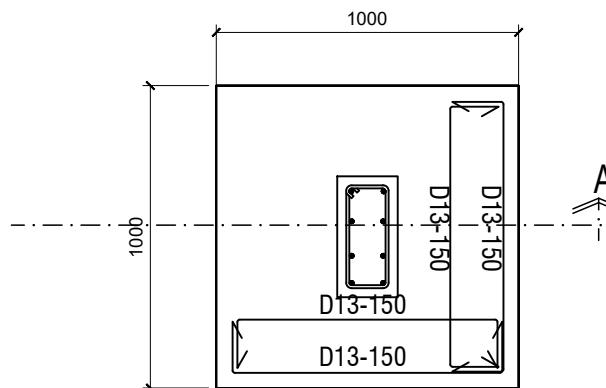


FOUNDATION DETAILS TYPE F3  
SCALE 1:25

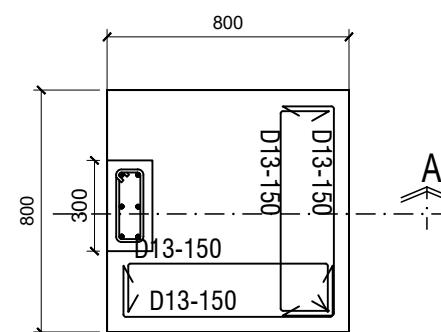

FOUNDATION DETAILS TYPE F4  
SCALE 1:25

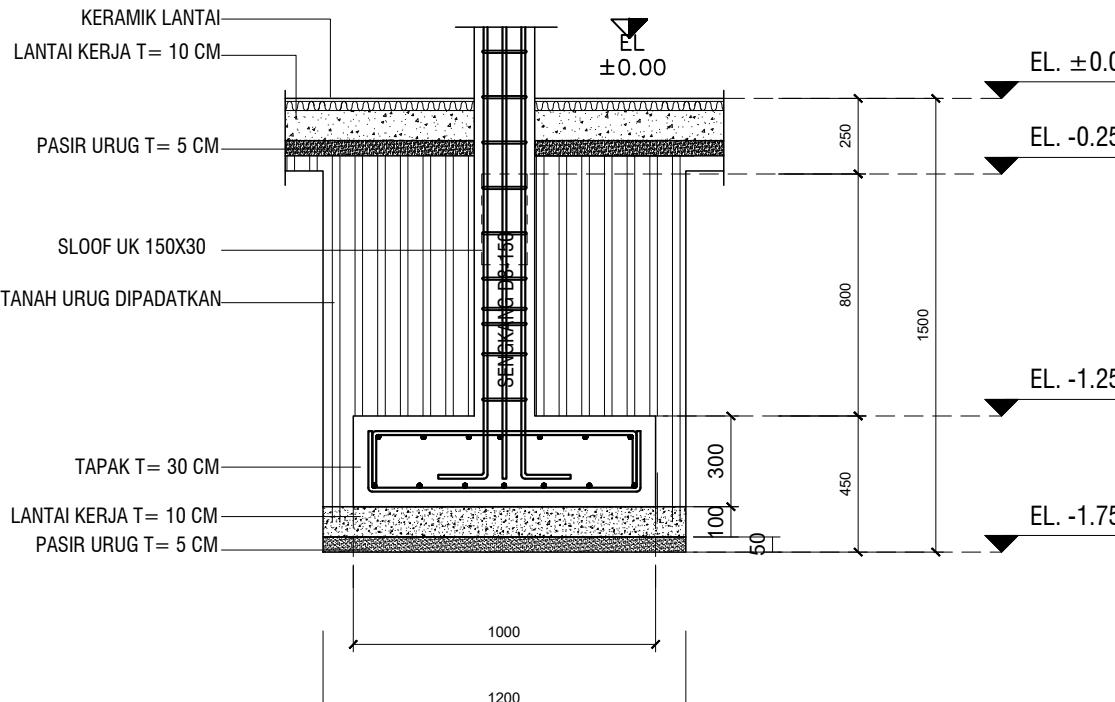

SECTION A  
SCALE 1:25

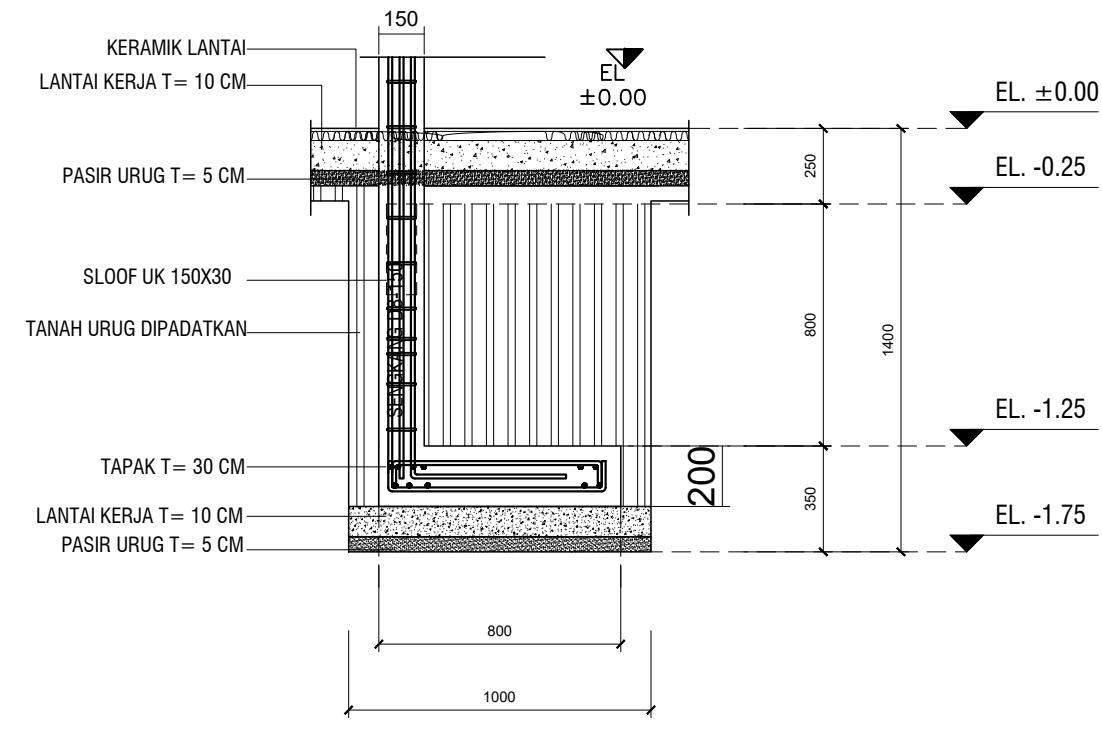


SECTION A  
SCALE 1:25


FOUNDATION DETAILS TYPE F3  
FOUNDATION DETAILS TYPE F4

SKALA :	1:25	DIGAMBAR	TGL.	
DIPERIKSA			TGL.	
DISETUJUI			TGL.	
DIKELUARKAN UNTUK :	FOR DESIGN DEVELOPMENT		TGL.	-
NO. PROYEK	NO. GAMBAR :	KODE GAMBAR :	REVISI :	
	71	STR-04		


NAMA PROYEK		RESIDENTIAL HOUSE AKASIA 2 / 59		
CATATAN :		<p>Sama dengan rencana dan karya seni yang tertulis pada gambar ini dilindungi oleh Undang-undang Hukum Cipta, serta hanya diperbolehkan untuk yang telah ditentukan dan tidak boleh diperbanyak tanpa ijin tertulis.</p> <p>Kontrak berlaku sejak ditandatangani dan merupakan dimensi terhadap keadaan lapangan dan apabila ada ketidakcocokan harus disampaikan kepada Arsitek.</p> <p>Gambar berdimensi tidak diperkenankan diambil.</p> <p>Sebelum pengerjaan dimulai, kontraktor berkewajiban untuk meminta persetujuan gambar kerja dan contoh teknis dari Arsitek.</p>		
PEMBERI TUGAS				
ARSITEK		ERIC HANDAYA, S.T I.A.I		
DRAFTING				
JUDUL GAMBAR :		GROUND BEAM FLOOR PLAN		
SKALA :		DIGAMBAR	TGL.	TGL.
1:100				
DIPERIKSA			TGL.	
DISETUJUI			TGL.	
DISETUJUI PEMB. TUGAS			TGL.	-
DIKELUARKAN UNTUK :		FOR DESIGN DEVELOPMENT		
NO. PROYEK	NO. GAMBAR :	KODE GAMBAR :	REVISI :	
	72	STR-05		

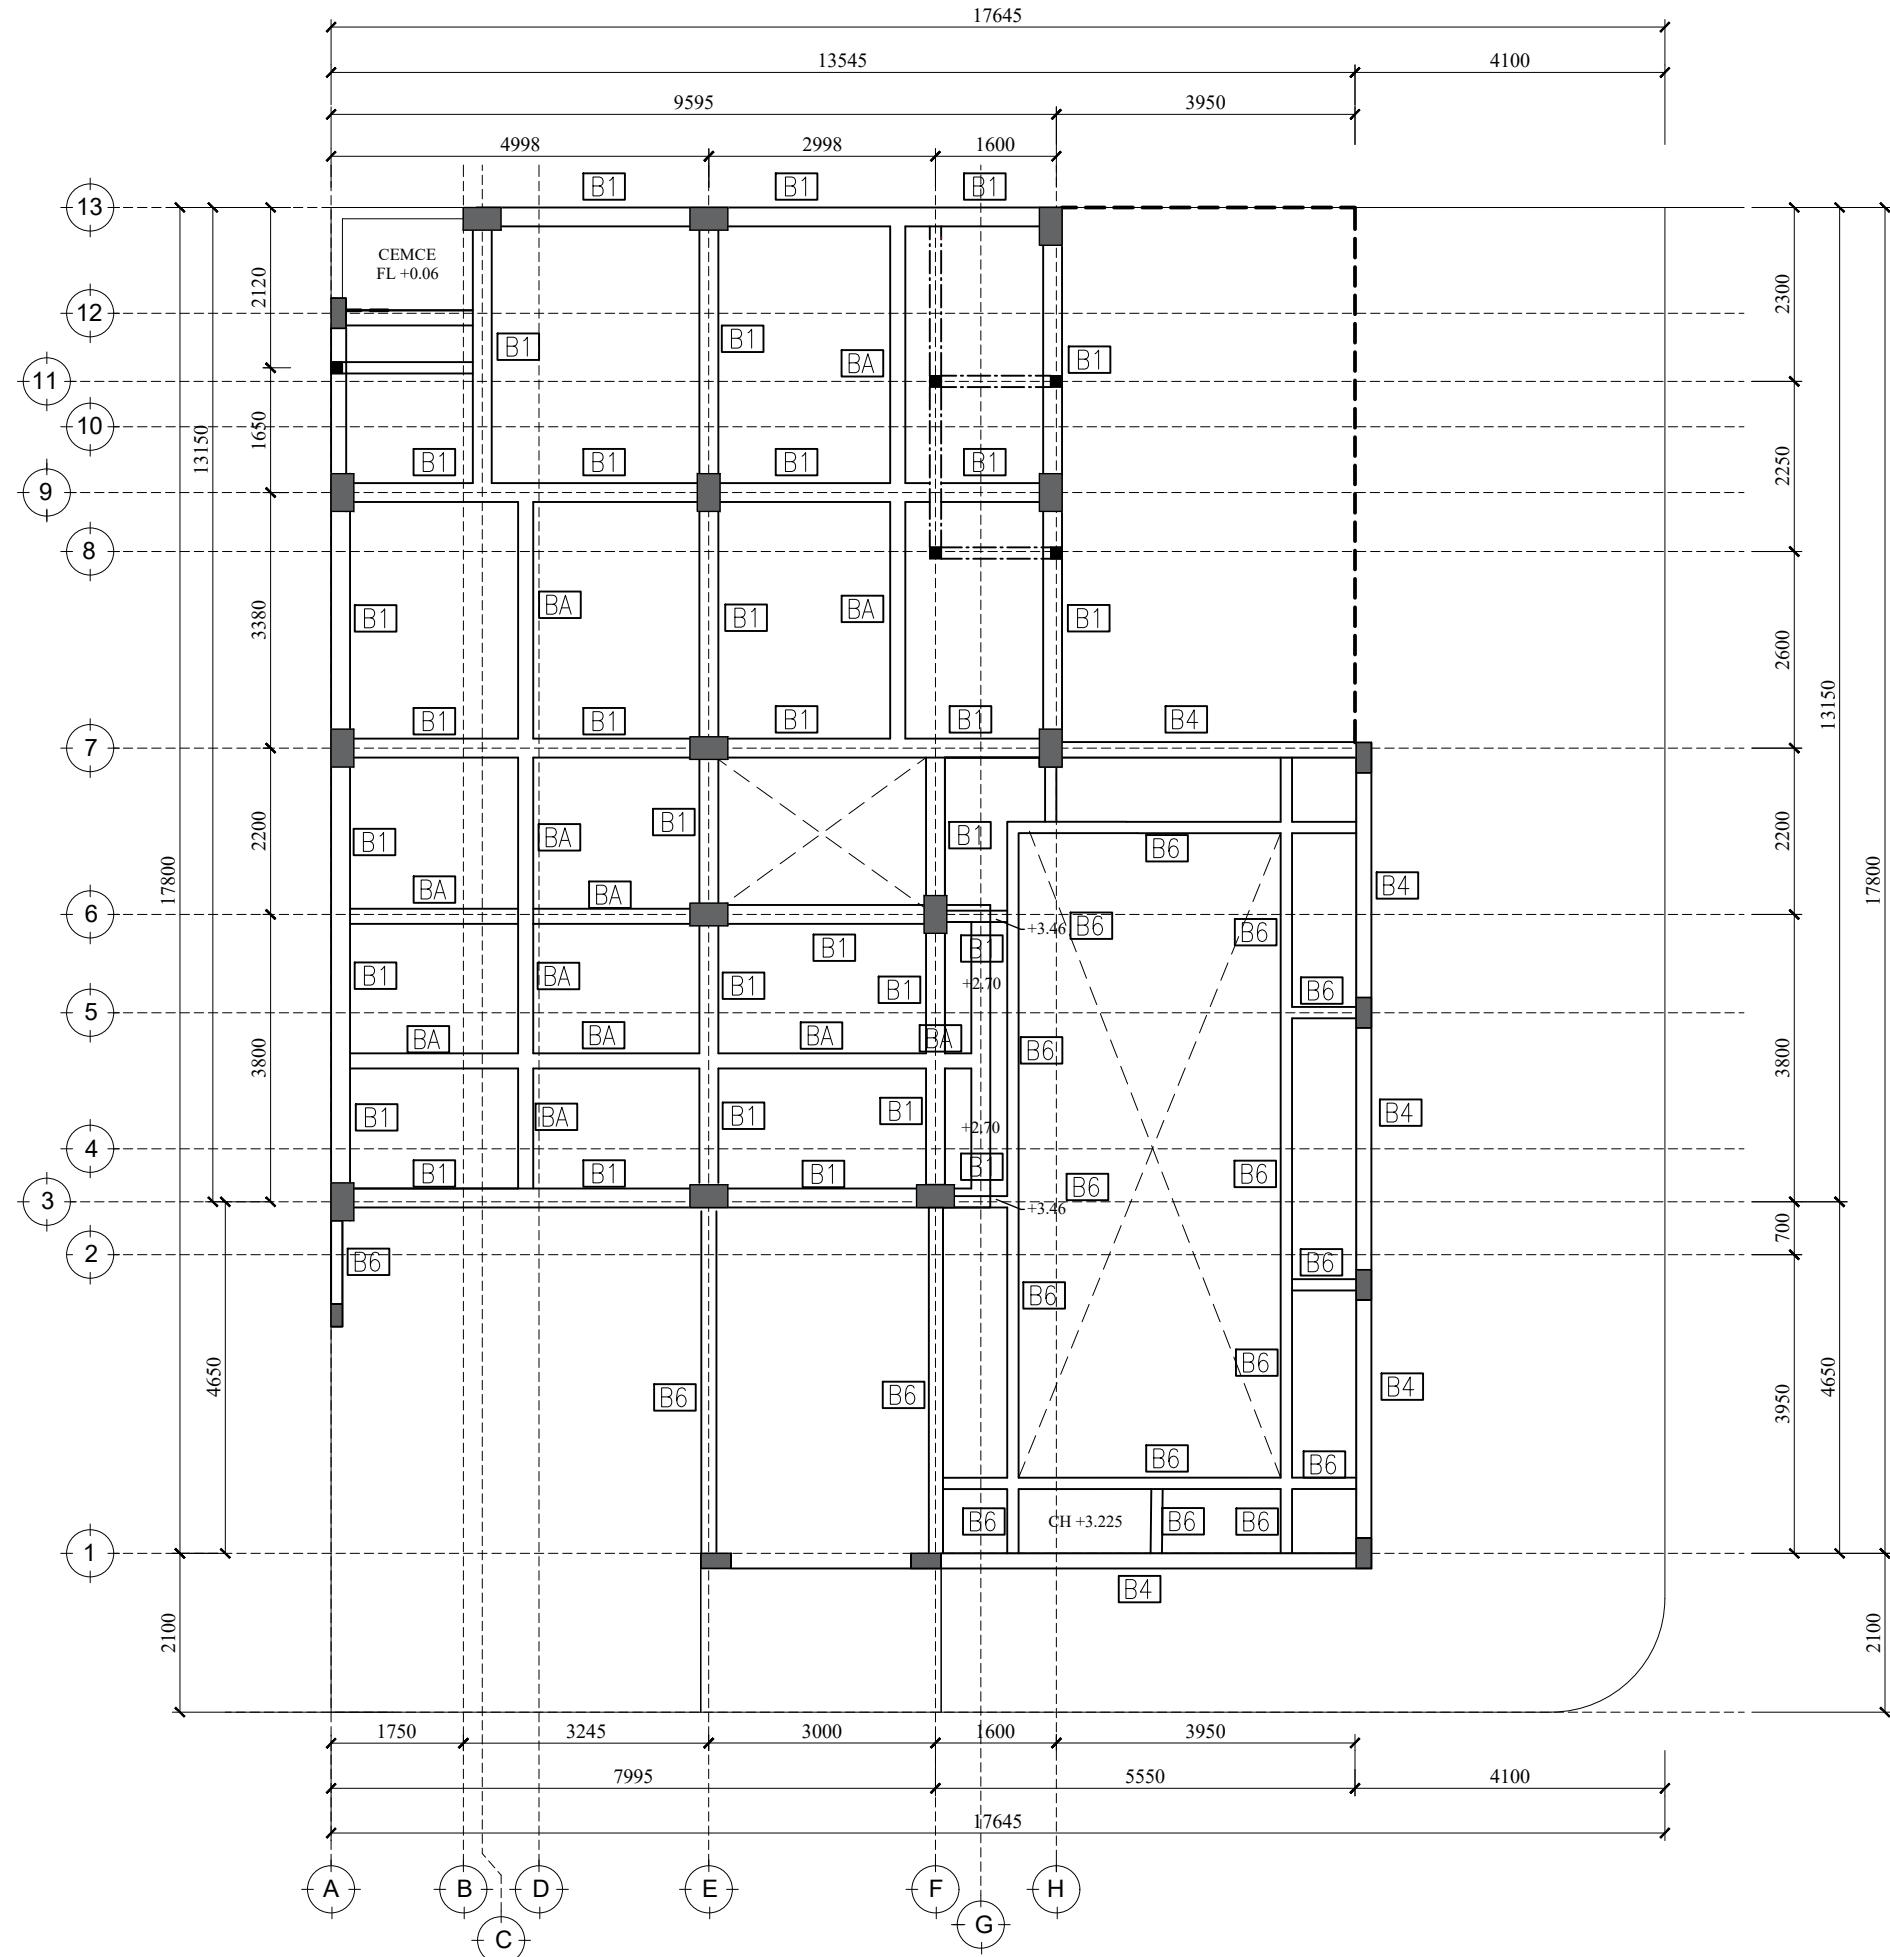


NAMA PROYEK		RESIDENTIAL HOUSE AKASIA 2 / 59		
CATATAN :		<p>Sama dengan rencana dan karya seni yang tertulis pada gambar ini dilindungi oleh Undang-undang Hukum Cipta, serta hanya diperbolehkan untuk yang telah ditentukan dan tidak boleh diperbaiki tanpa izin tertulis.</p> <p>Kontrak berlaku setelah memahami dimensi terhadap keadaan lapangan dan apabila ada ketidakcocokan harus disampaikan kepada Arsitek.</p> <p>Gambar berdimensi tidak diperkenankan diakses.</p> <p>Sebelum pengerjaan dimulai, kontraktor berkewajiban untuk meminta persetujuan gambar kerja dan contoh bukti dari Arsitek.</p>		
PEMBERI TUGAS				
ARSITEK		ERIC HANDAYA, S.T I.A.I		
DRAFTING				
JUDUL GAMBAR :		1ST BEAM FLOOR PLAN		
SKALA :		DIGAMBAR	TGL.	
1:100				
DIPERIKSA			TGL.	
DISETUJUI			TGL.	
DISETUJUI PEMB. TUGAS			TGL.	-
DIKELUARKAN UNTUK :		FOR DESIGN DEVELOPMENT		
NO. PROYEK	NO. GAMBAR :	KODE GAMBAR :	REVISI :	
	73	STR-06		

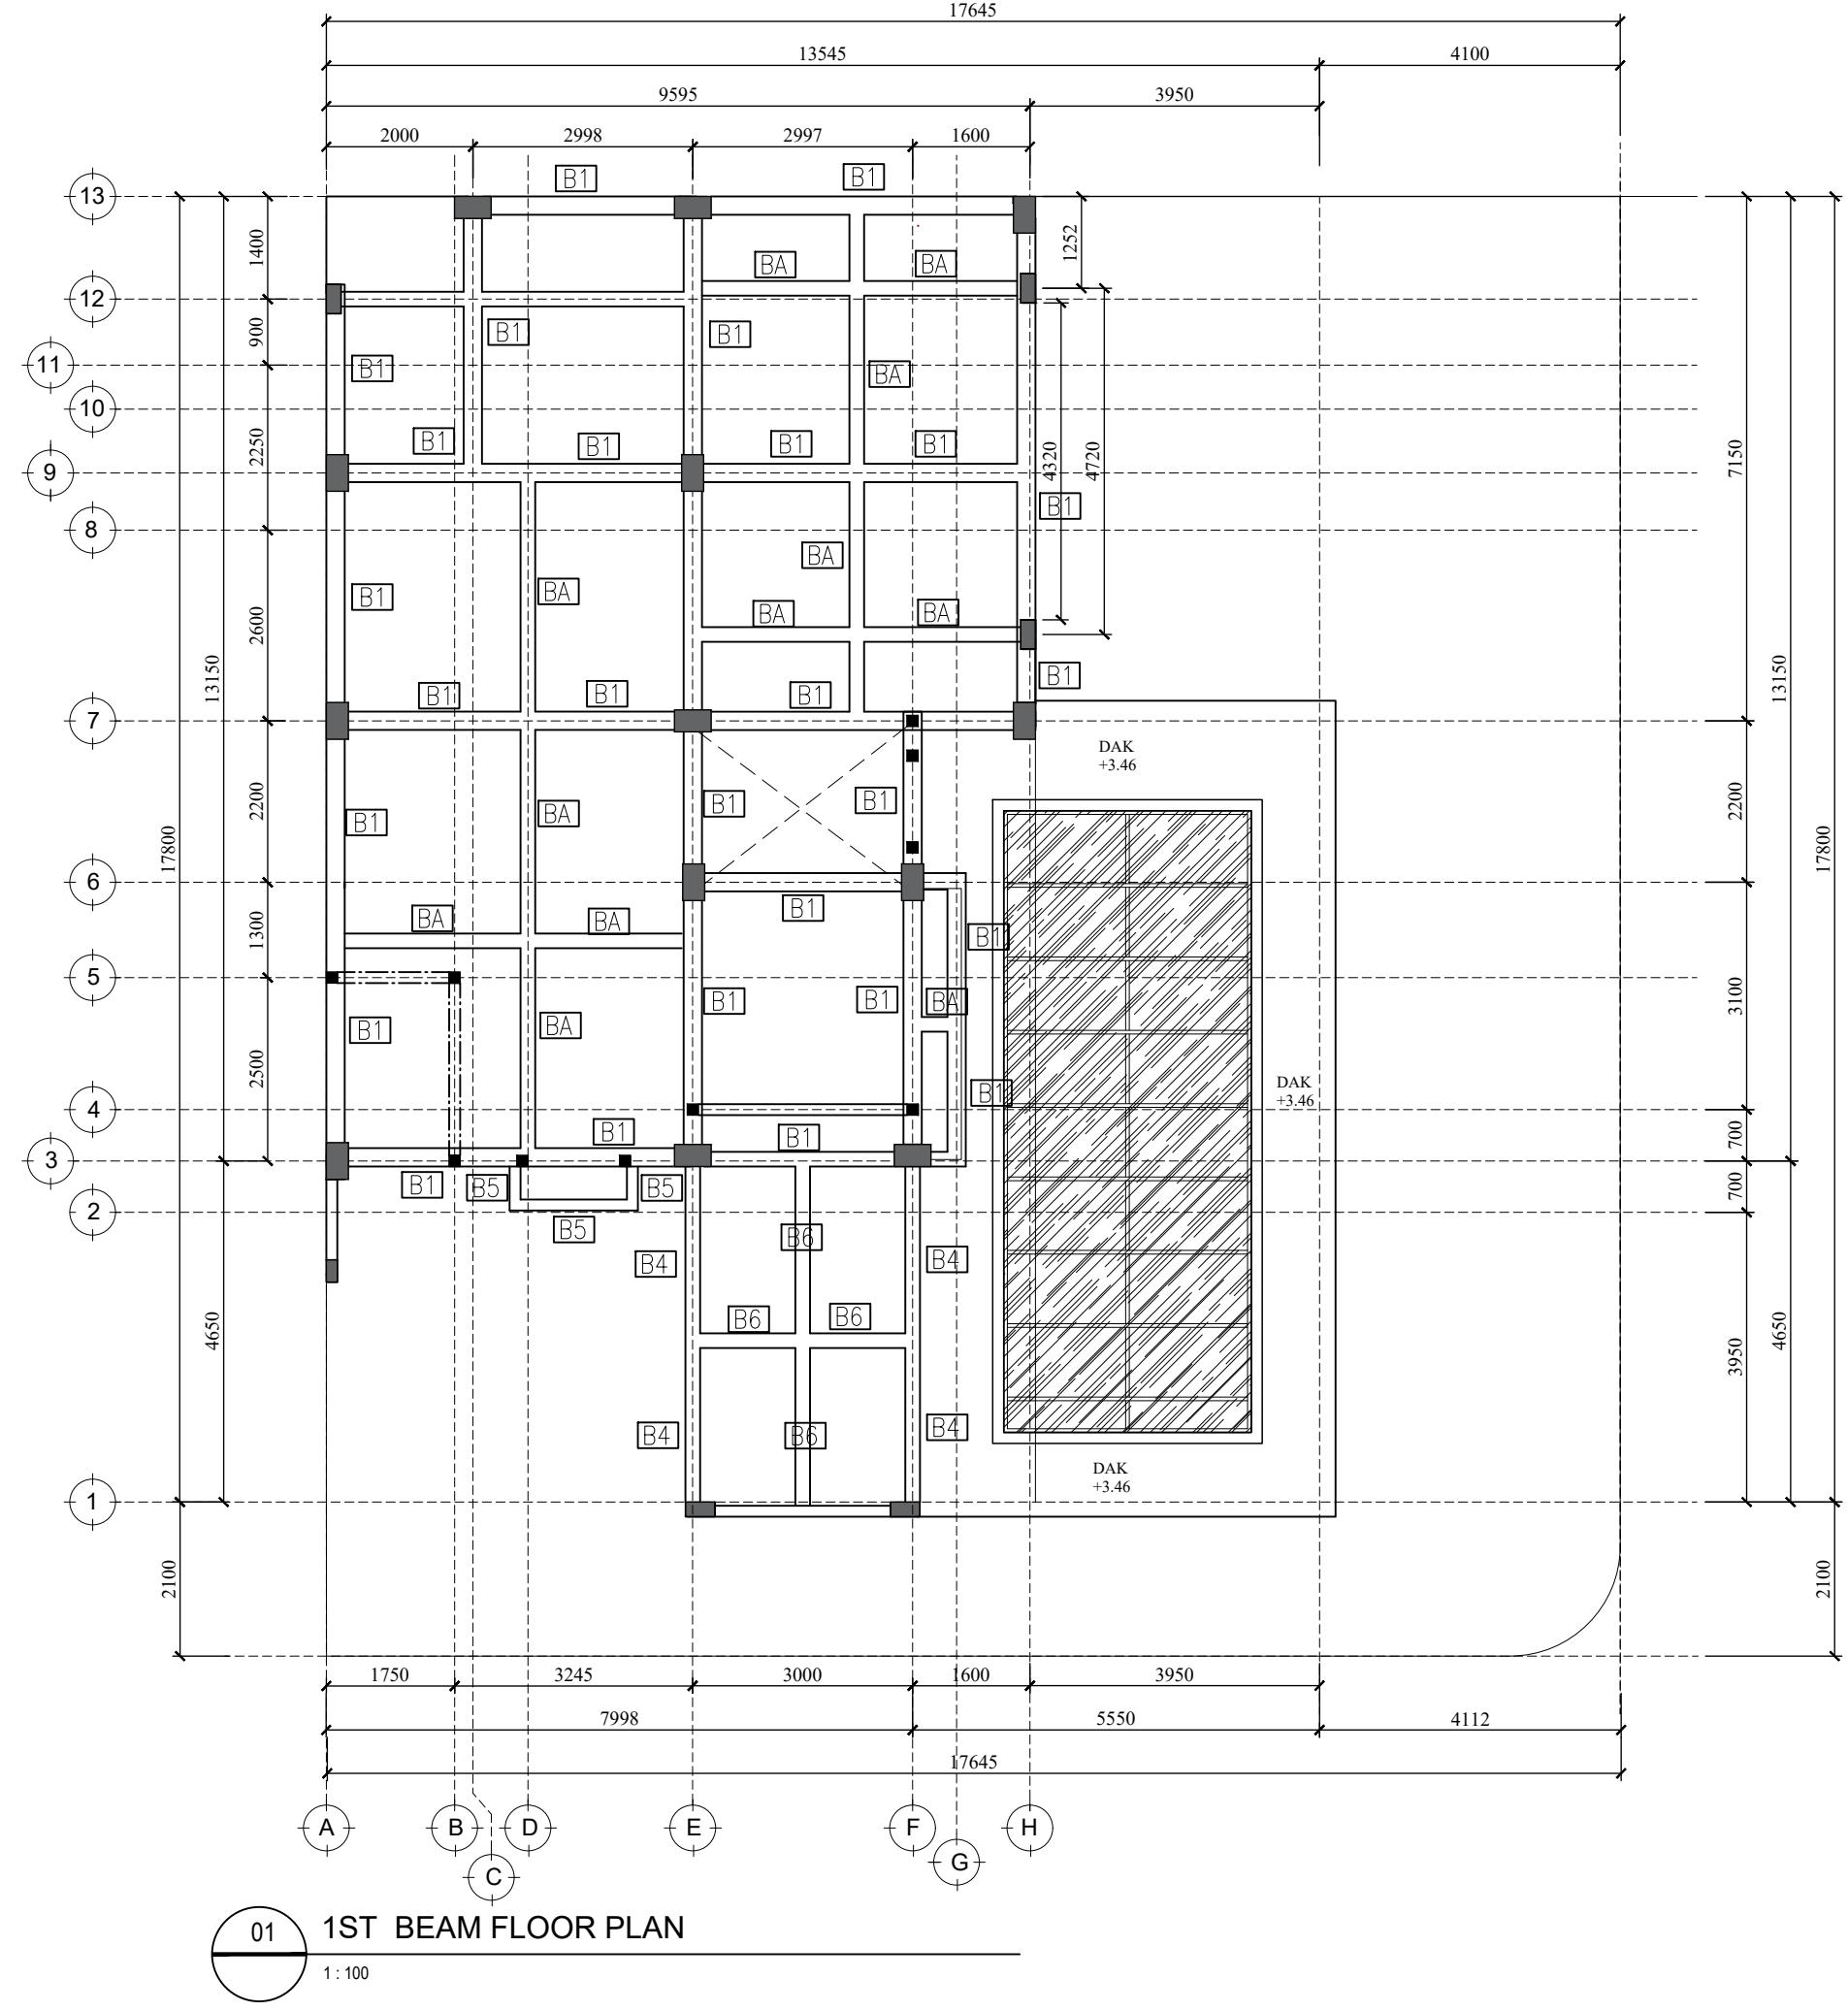

NAMA PROYEK		RESIDENTIAL HOUSE AKASIA 2 / 59					
CATATAN :		<p>Sama dengan rencana dan karya seni yang tertulis pada gambar ini dilindungi oleh Undang-undang Hak Cipta, serta hanya diperbolehkan untuk yang telah ditentukan dan tidak boleh diperbanyak tanpa ijin tertulis.</p> <p>Kontrak berlaku bila terdapat permasalahan dimensi terhadap keadaan lapangan dan apabila ada ketidaksesuaian harus disampaikan kepada Arsitek.</p> <p>Gambar berdimensi tidak diperkenankan diambil.</p> <p>Sebelum pengerjaan dimulai, kontraktor berkewajiban untuk meminta persetujuan gambar kerja dan contoh buah dari Arsitek.</p>					
PEMBERI TUGAS							
ARSITEK		ERIC HANDAYA, S.T I.A.I					
DRAFTING							
JUDUL GAMBAR :		2ND BEAM FLOOR PLAN					
SKALA :		1:100		DIGAMBAR		TGL.	
				DIPERIKSA		TGL.	
				DISETUJUI		TGL.	
DIKELUARKAN UNTUK :		FOR DESIGN DEVELOPMENT					
NO. PROYEK	NO. GAMBAR :	KODE GAMBAR :		REVISI :			
	74	STR-07					

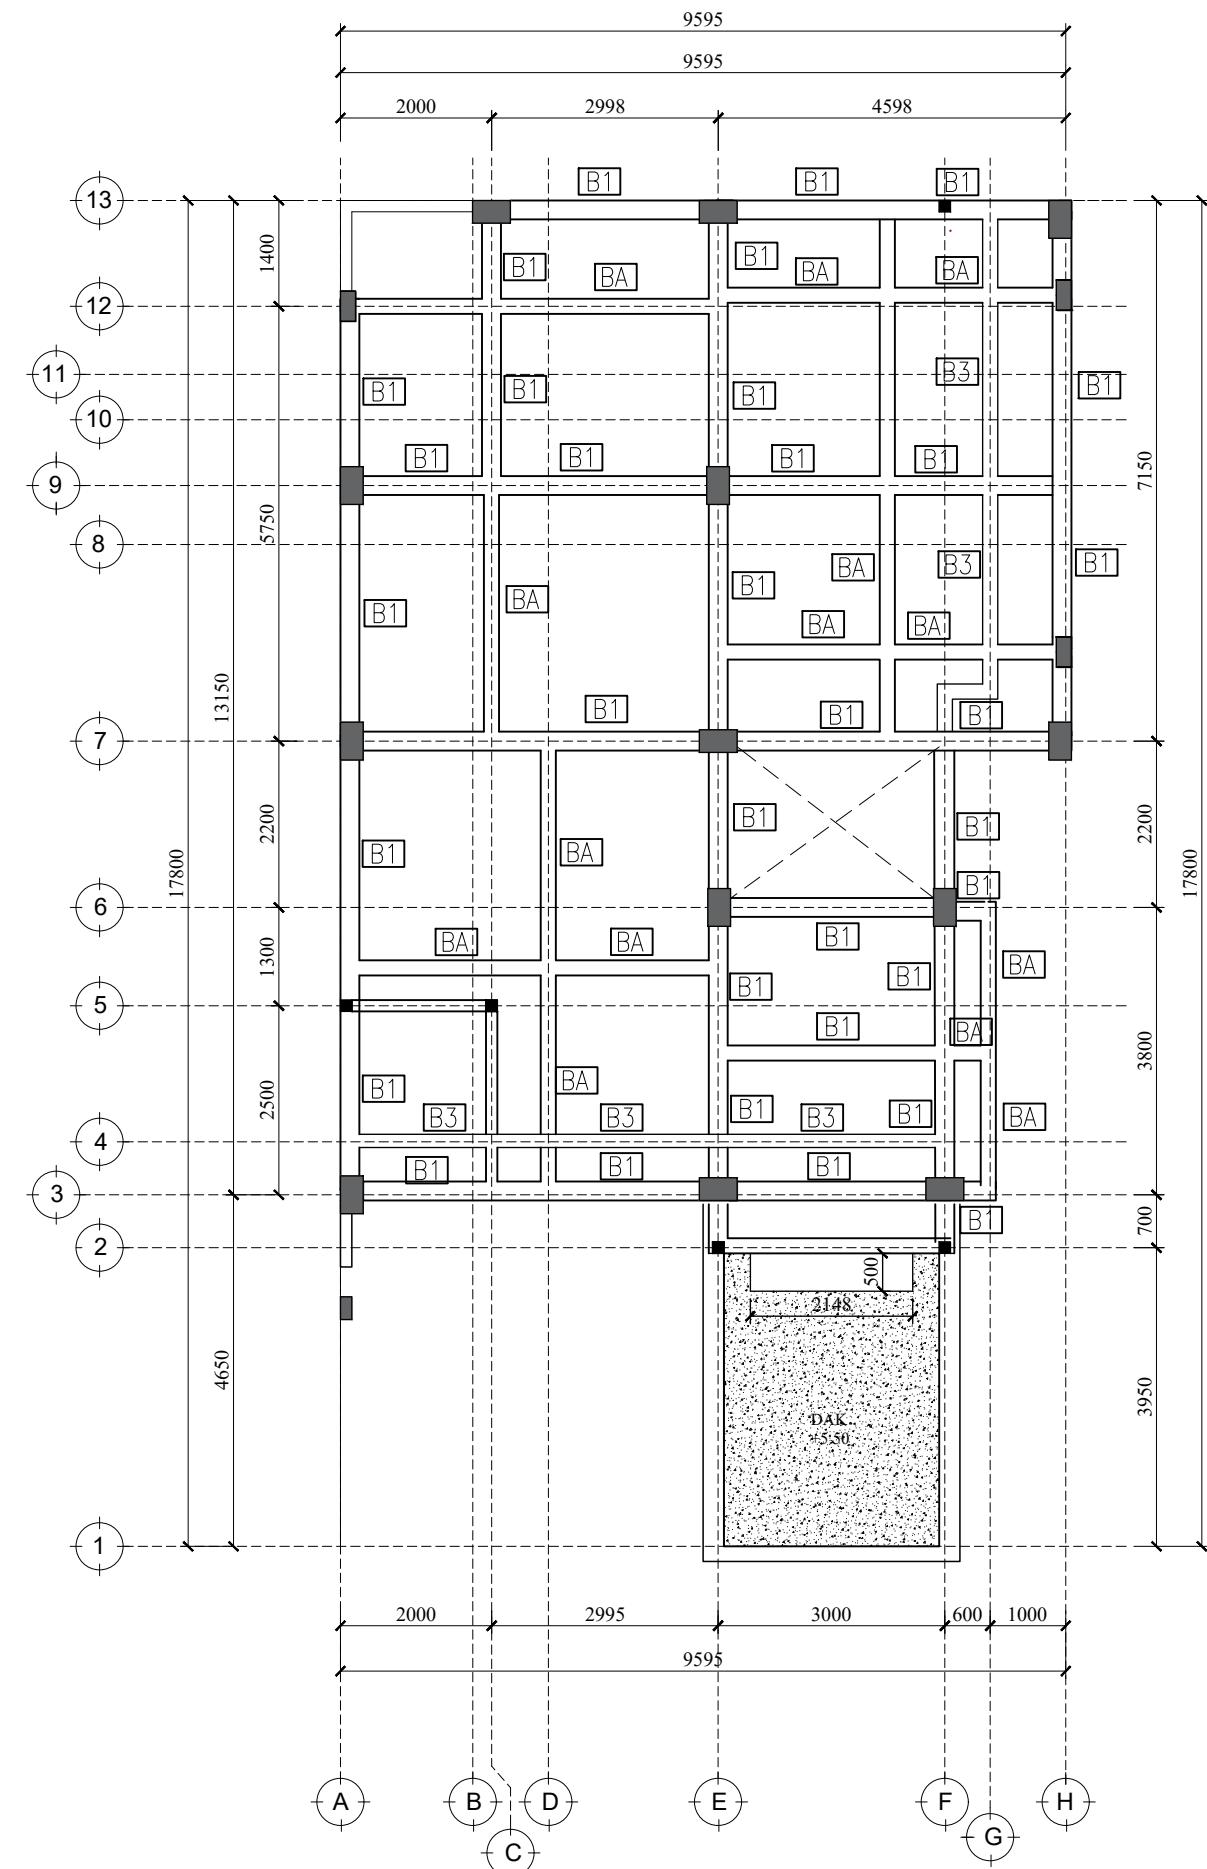


01 2ND BEAM FLOOR PLAN  
1 : 100

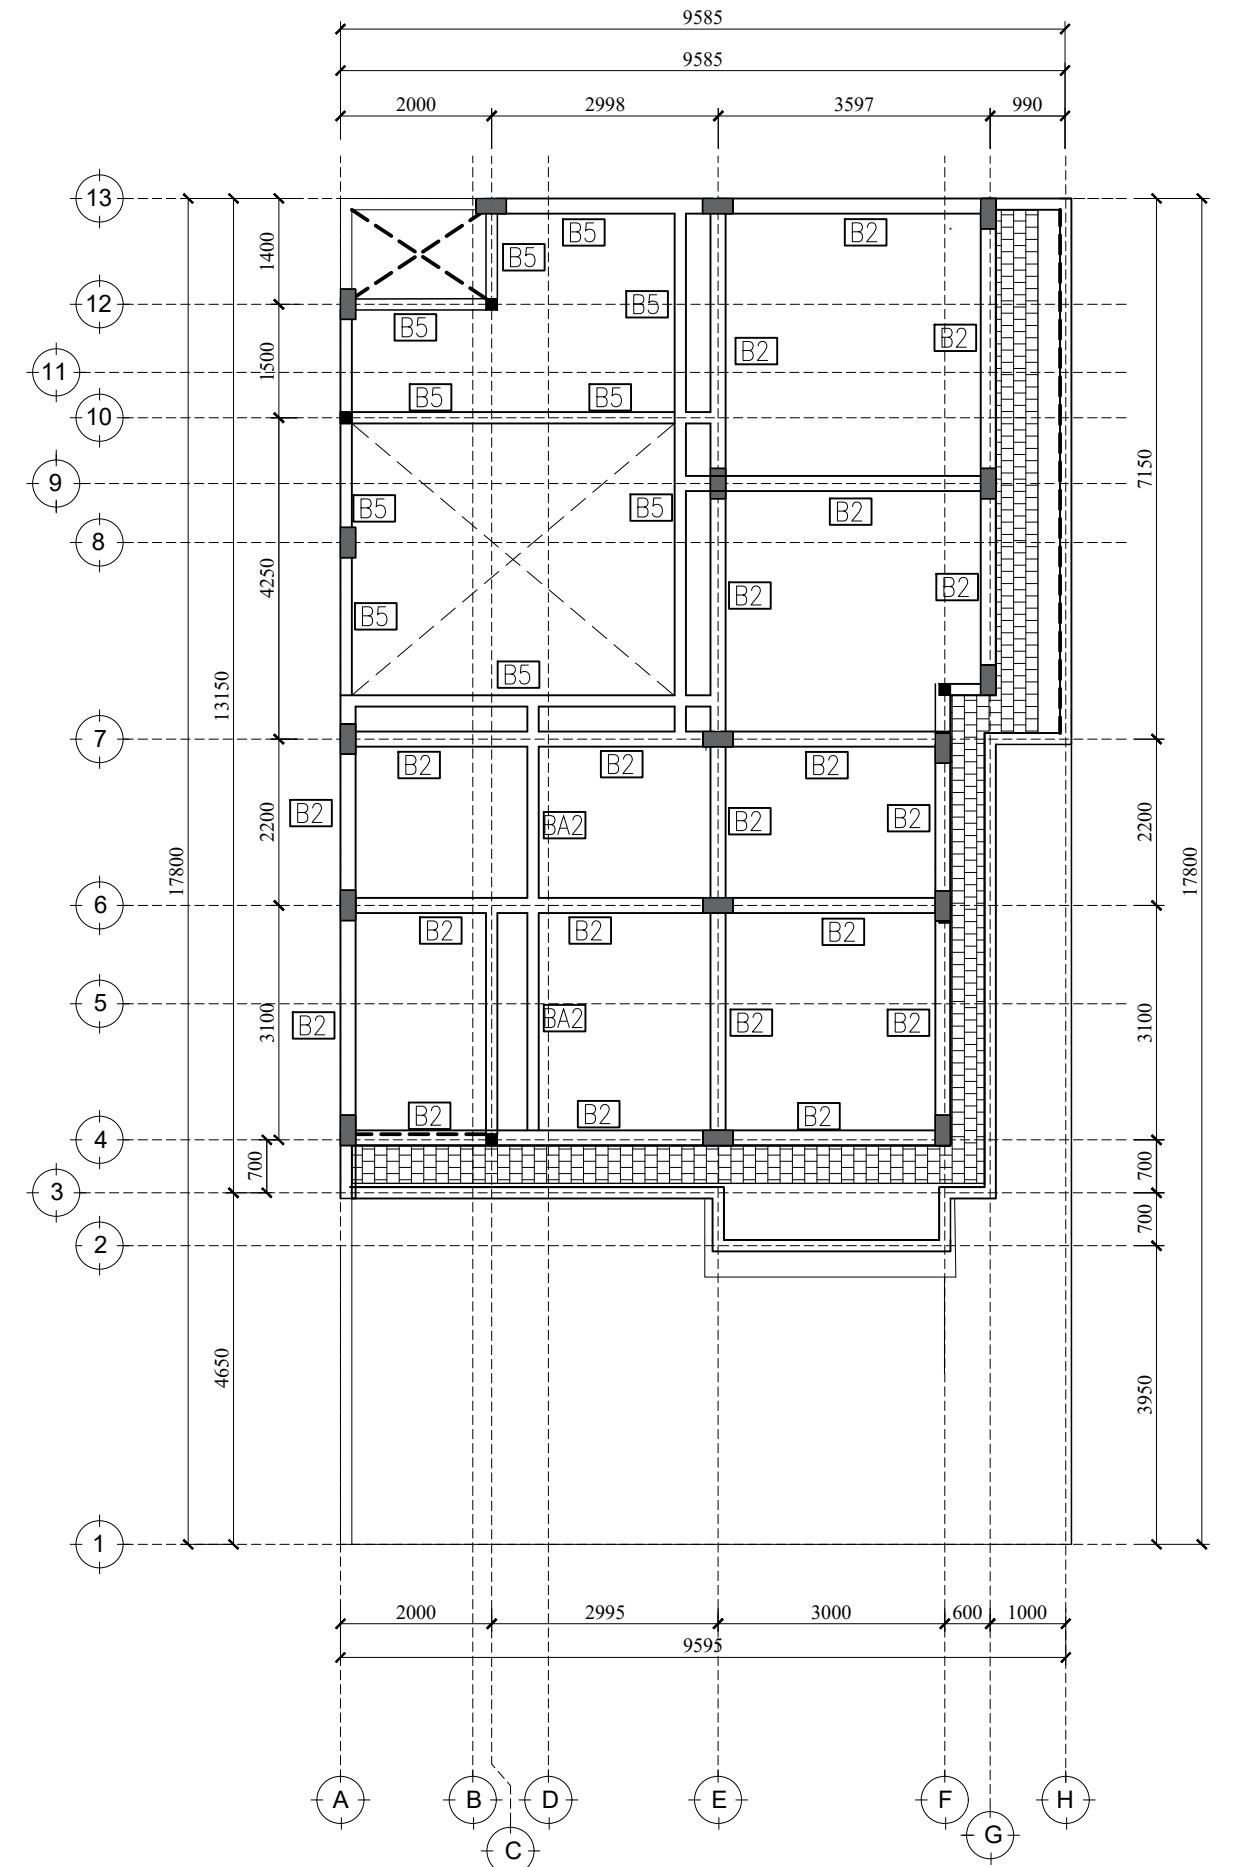


## 01 ROOF BEAM FLOOR PLAN


1 : 1

NAMA PROYEK	RESIDENTIAL HOUSE AKASIA 2 / 59		
CATATAN :	Simpan detail, rencangan dan karya seni yang tertulis pada gambar ini dilindungi oleh Undang-undang Hukum Cipta, serta hanya diperbolehkan untuk yang telah ditentukan dan tidak boleh diperbaiki tanpa ijin tertulis. Kompleksitas teknis dalam merumuskan dimensi terhadap kedudukan lapangan dan apabila ada ketidaksesuaian harus disampaikan kepada Arsitek. Gambar berdimensi tidak diperkenankan diakses. Sebelum pengerjaan dilaksanakan, kontraktor berkewajiban untuk meminta persetujuan gambar kerja dan contoh buah dari Arsitek.		
PEMBERI TUGAS			
ARSITEK	ERIC HANDAYA, S.T I.A.I		
DRAFTING			
JUDUL GAMBAR :	GROUND COLUMN FLOOR PLAN		
SKALA :	1:100	DIGAMBAR	TGL.
		DIPERIKSA	TGL.
		DISETUJUI	TGL.
DISETUJUI PEMB. TUGAS			TGL. -
DIKELUARKAN UNTUK : FOR DESIGN DEVELOPMENT			
NO. PROYEK	NO. GAMBAR :	KODE GAMBAR :	REVISI :
	76	STR-09	

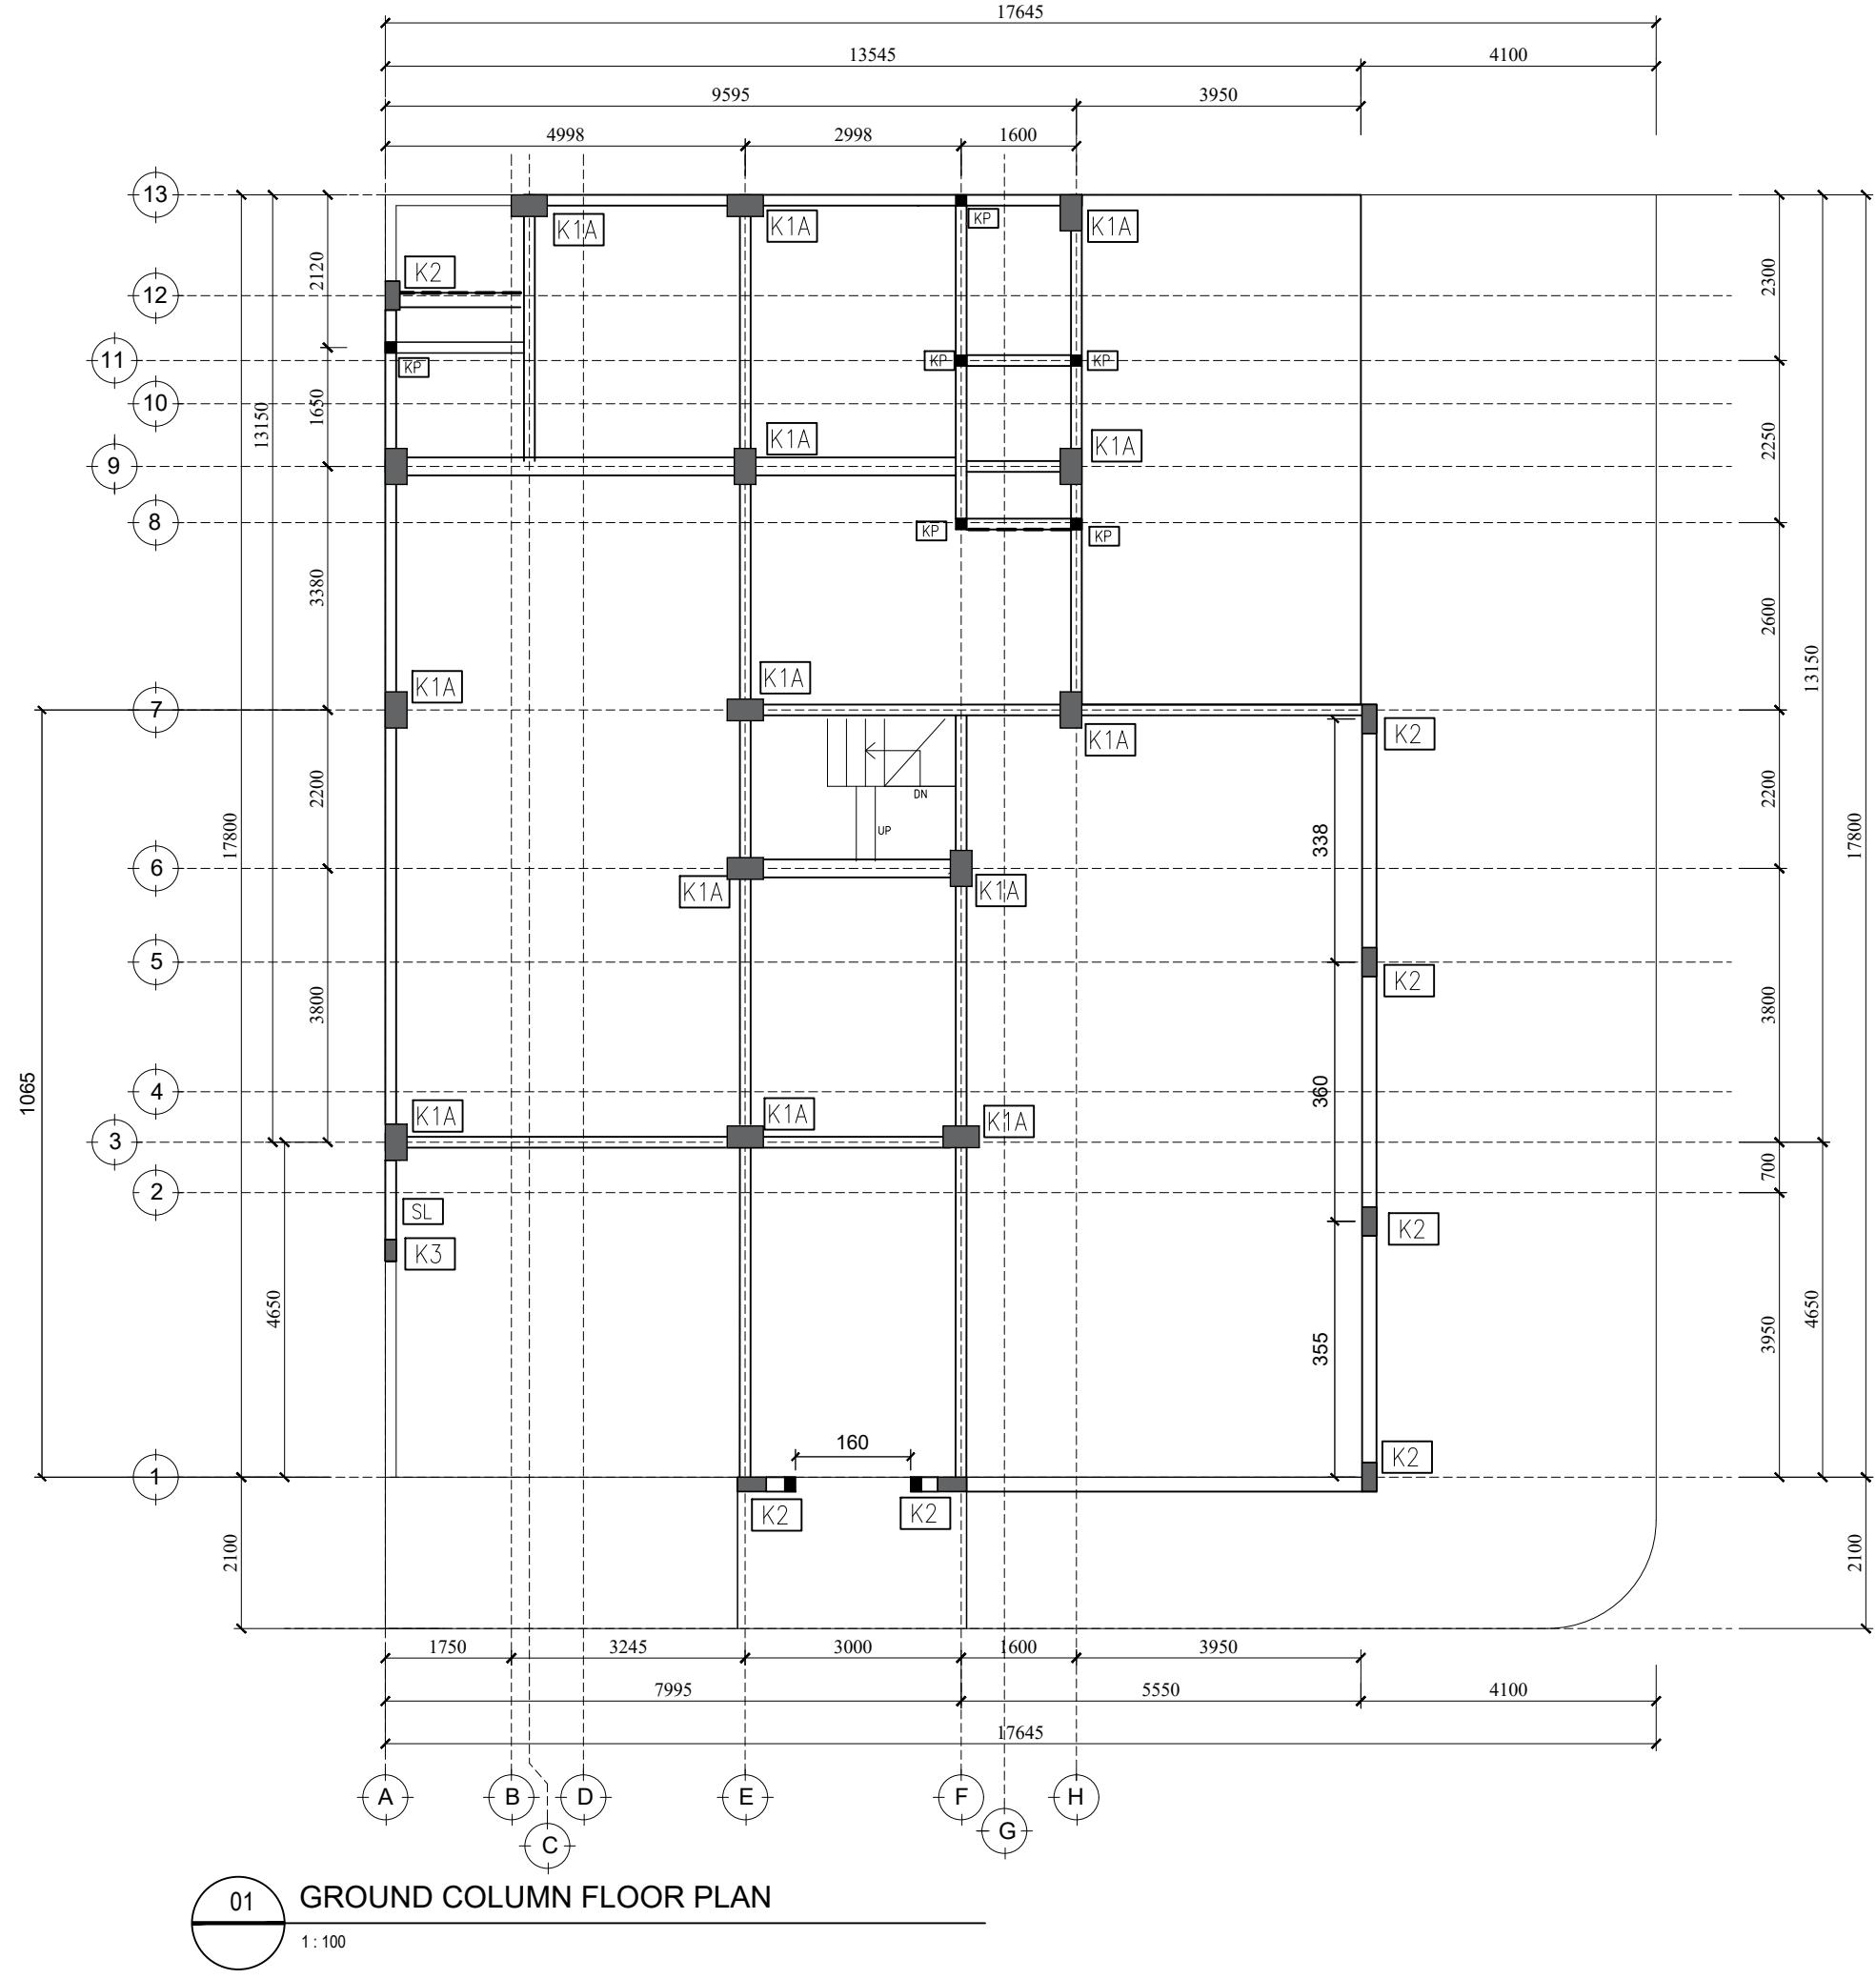

NAMA PROYEK	RESIDENTIAL HOUSE AKASIA 2 / 59					
<b>CATATAN :</b> Semua garis, retoran dan lingkaran seni yang tertera pada gambar ini diilustrasi dan diperbaiki tanpa izin tertulis. Kontak berikut ini untuk menyalas dimensi terhadap keadaan lapangan dan apabila ada ketidaksesuaian harus disampaikan kepada Arsitek. Gambar berdimensi tidak diperkenankan diskota. Sebelum pekerjaan dilaksanakan, kontraktor berkewajiban untuk meminta persetujuan gambar kerja dan contoh buah dari Arsitek.						
<b>PEMBERI TUGAS</b>						
ERIC HANDAYA, S.T I.A.I						
<b>ARSITEK</b>						
<b>DRAFTING</b>						
TOI						
REVISI						
NO. TOL						
<b>JUDUL GAMBAR :</b>						
1ST COLUMN FLOOR PLAN						
<b>SKALA :</b>						
1:100		DIGAMBAR	TGL.			
DIPERIKSA		TGL.				
DISETUJUI		TGL.				
DISETUJUI PEMB. TUGAS		TGL.	-			
<b>DIKELUARKAN UNTUK :</b>						
FOR DESIGN DEVELOPMENT						
<b>NO. PROYEK</b>						
01		KODE GAMBAR :	REVISI :			
1 : 100		STR-10				

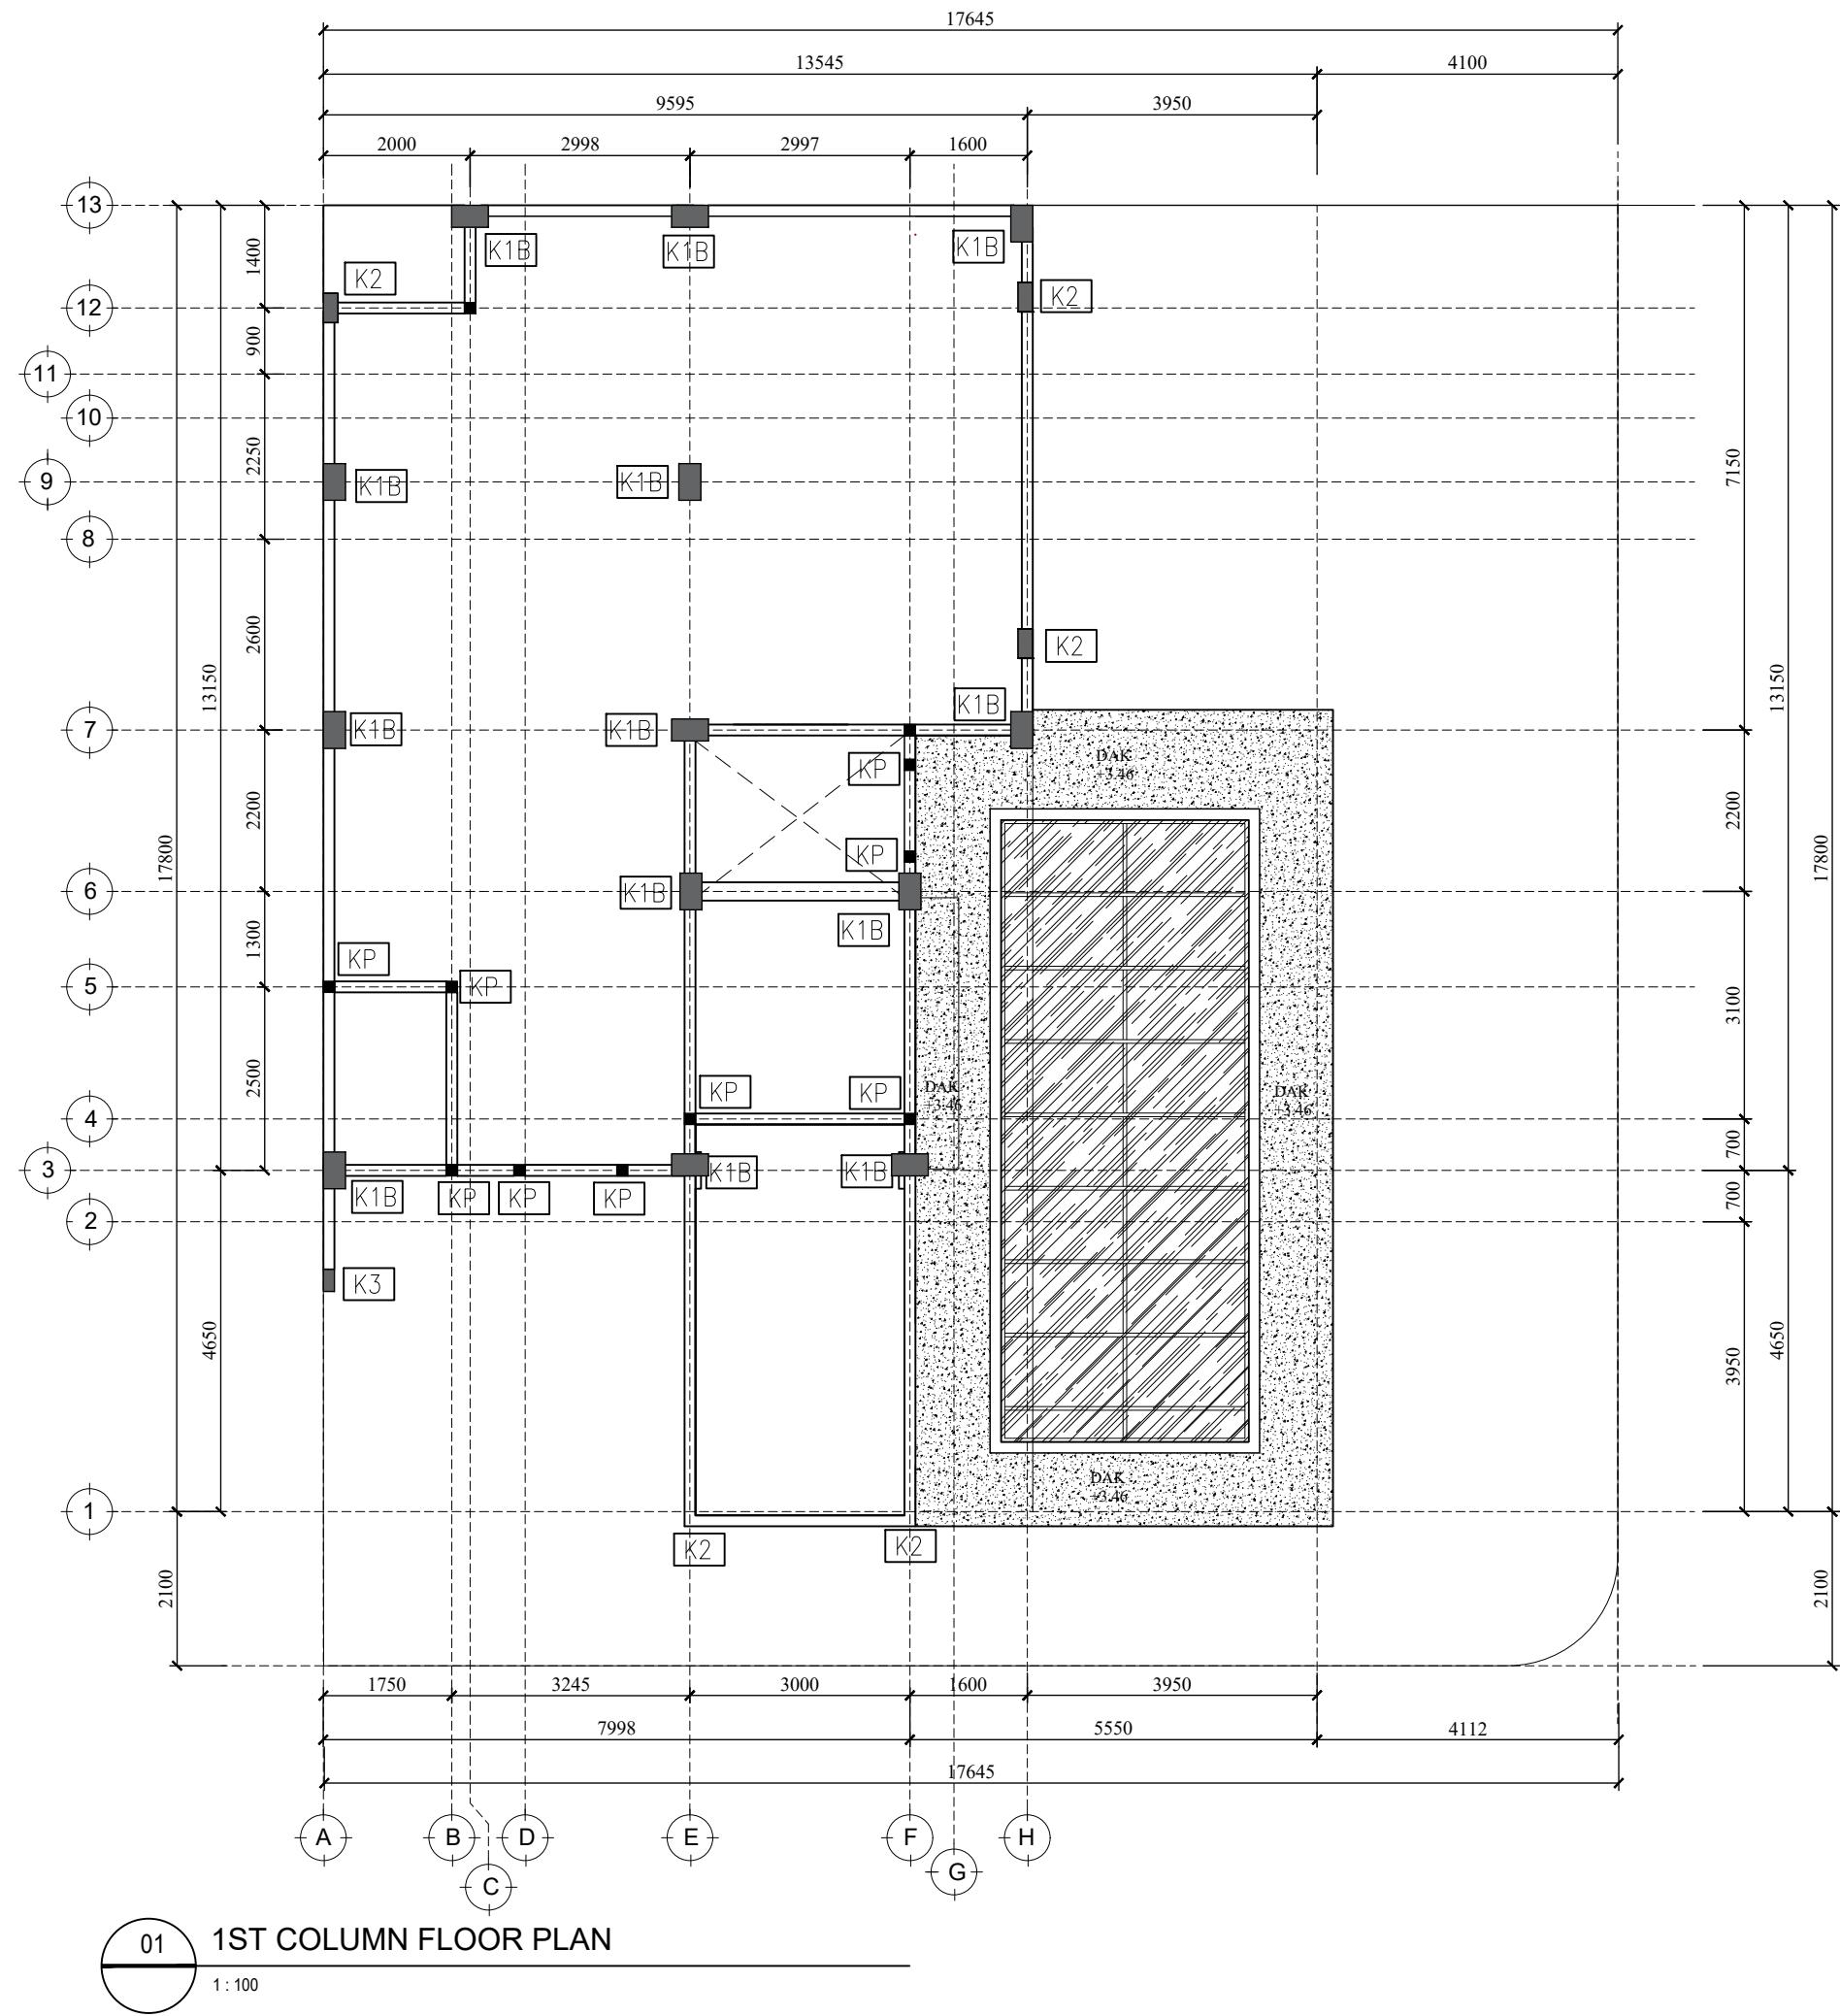

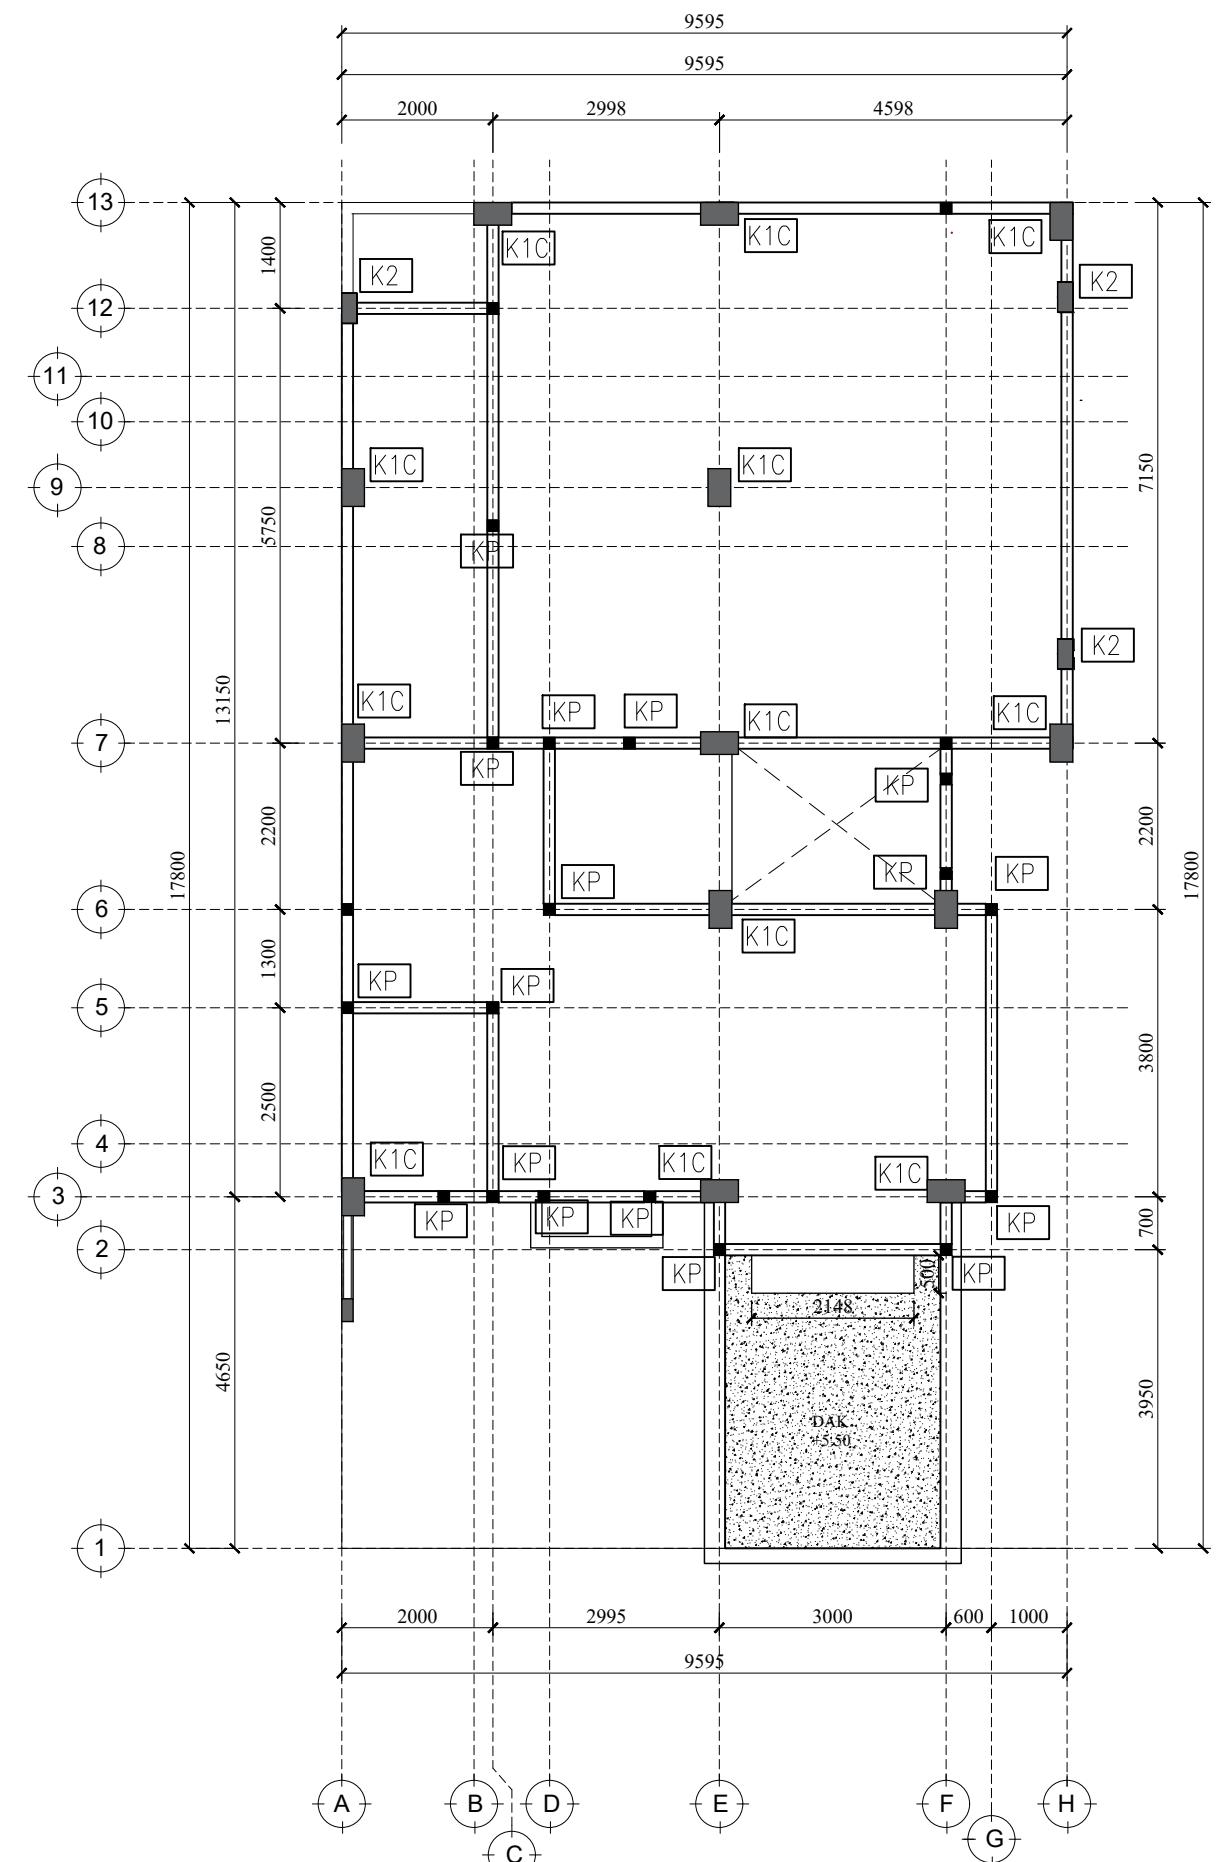



01 2ND COLUMN FLOOR PLAN

1:10

RESIDENTIAL HOUSE AKASIA 2 / 59


NAMA PROYEK	RESIDENTIAL HOUSE AKASIA 2 / 59		
CATATAN :	<p>Sama dengan rencana dan karya seni yang tertulis pada gambar ini dilakukan oleh Undang-undang Huk. Cipta, serta hanya diperlukan untuk yang telah ditentukan dan tidak boleh diperbaiki tanpa ijin tertulis.</p> <p>Kontrak berlaku sepanjang memenuhi dimensi terhadap keadaan lapangan dan apabila ada kelakuan yang harus disampaikan kepada Arsitek.</p> <p>Gambar berdimensi tidak diperkenankan diambil.</p> <p>Sebelum pengerjaan dimulai, kontraktor berkewajiban untuk meminta persetujuan gambar kerja dan contoh buah dari Arsitek.</p>		
PEMBERI TUGAS			
ARSITEK	ERIC HANDAYA, S.T I.A.I		
DRAFTING			
REVISI			
JUDUL GAMBAR :	3RD COLUMN FLOOR PLAN		
SKALA :	DIGAMBAR	TGL.	
1:100			
DIPERIKSA		TGL.	
DISETUJUI		TGL.	
DISETUJUI PEMB. TUGAS		TGL.	-
DIKELUARKAN UNTUK : FOR DESIGN DEVELOPMENT			
NO. PROYEK	NO. GAMBAR :	KODE GAMBAR :	REVISI :
	79	STR-12	

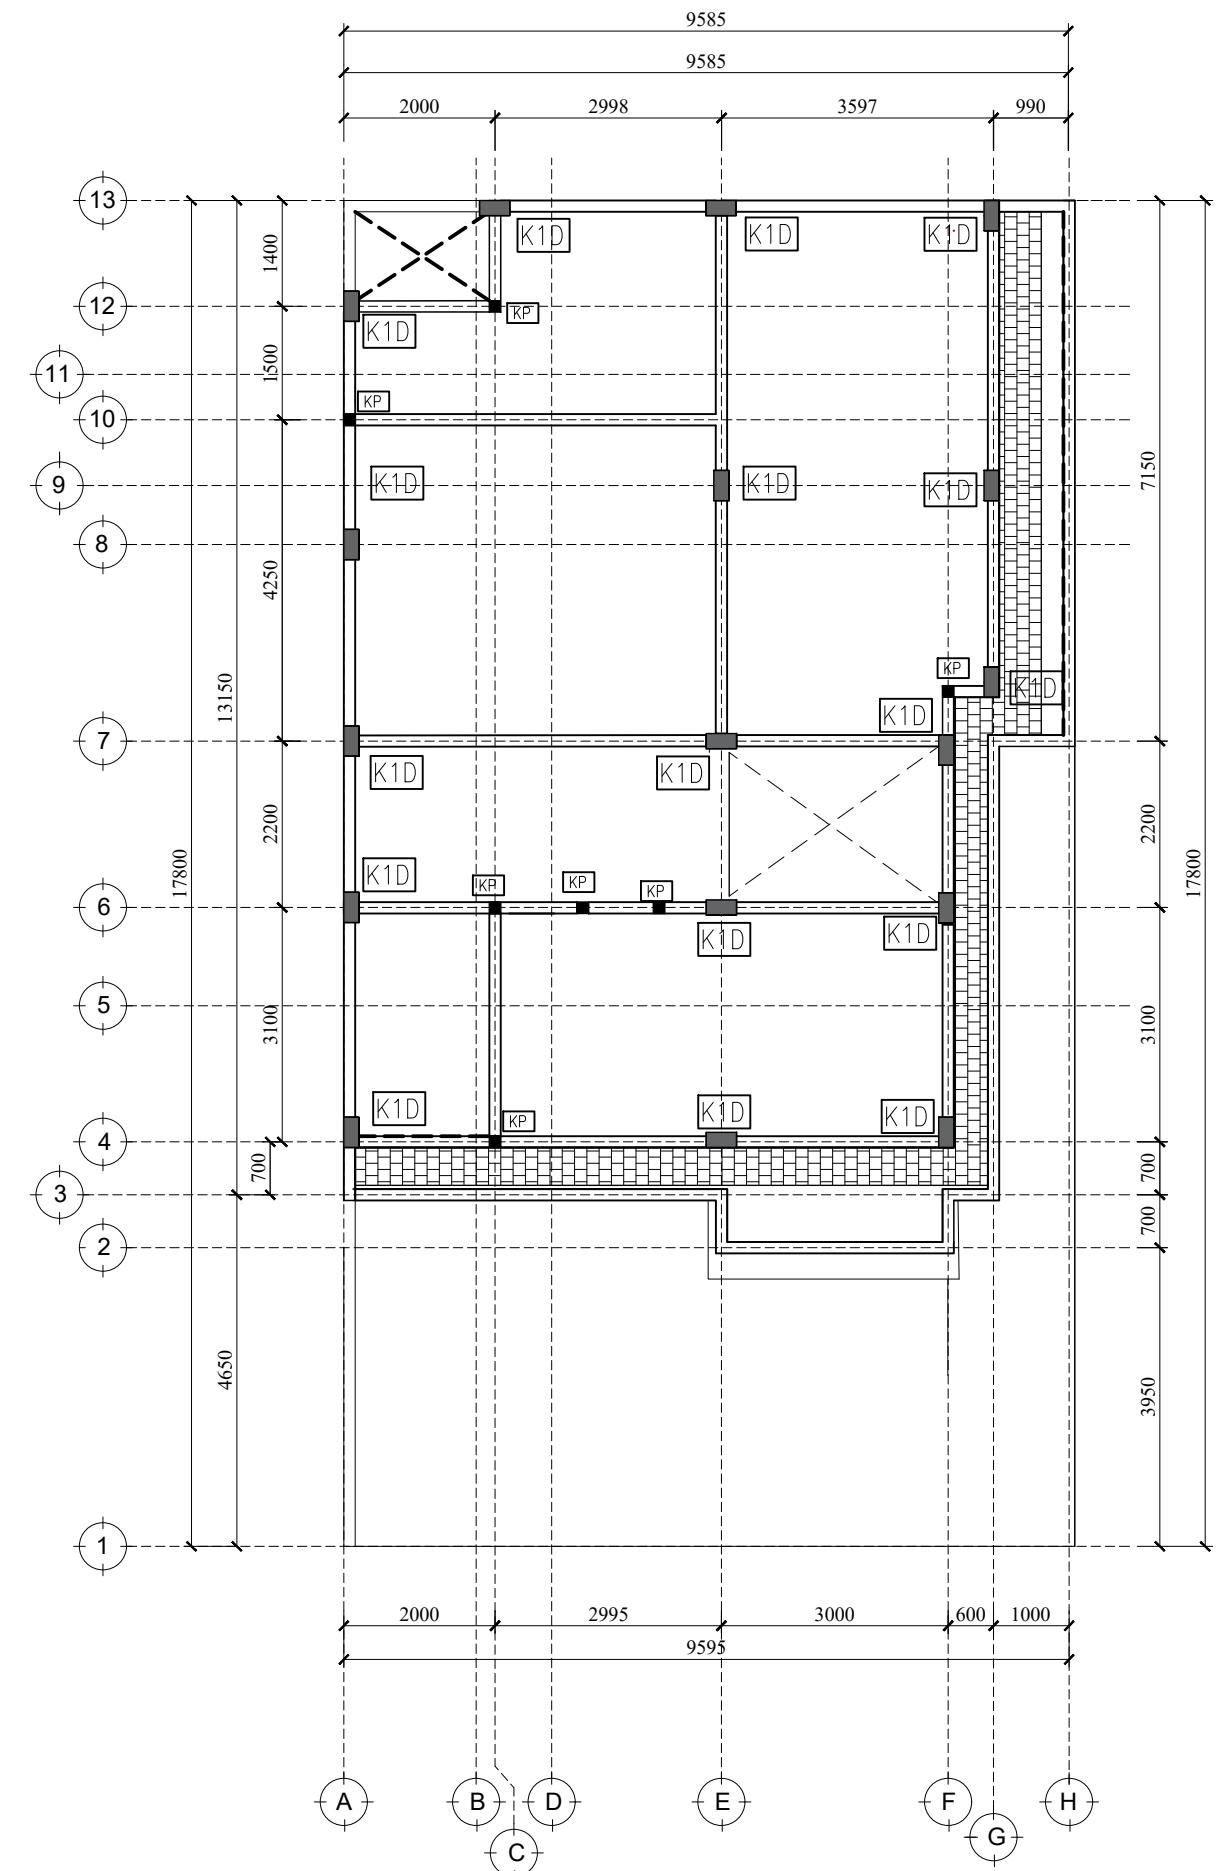

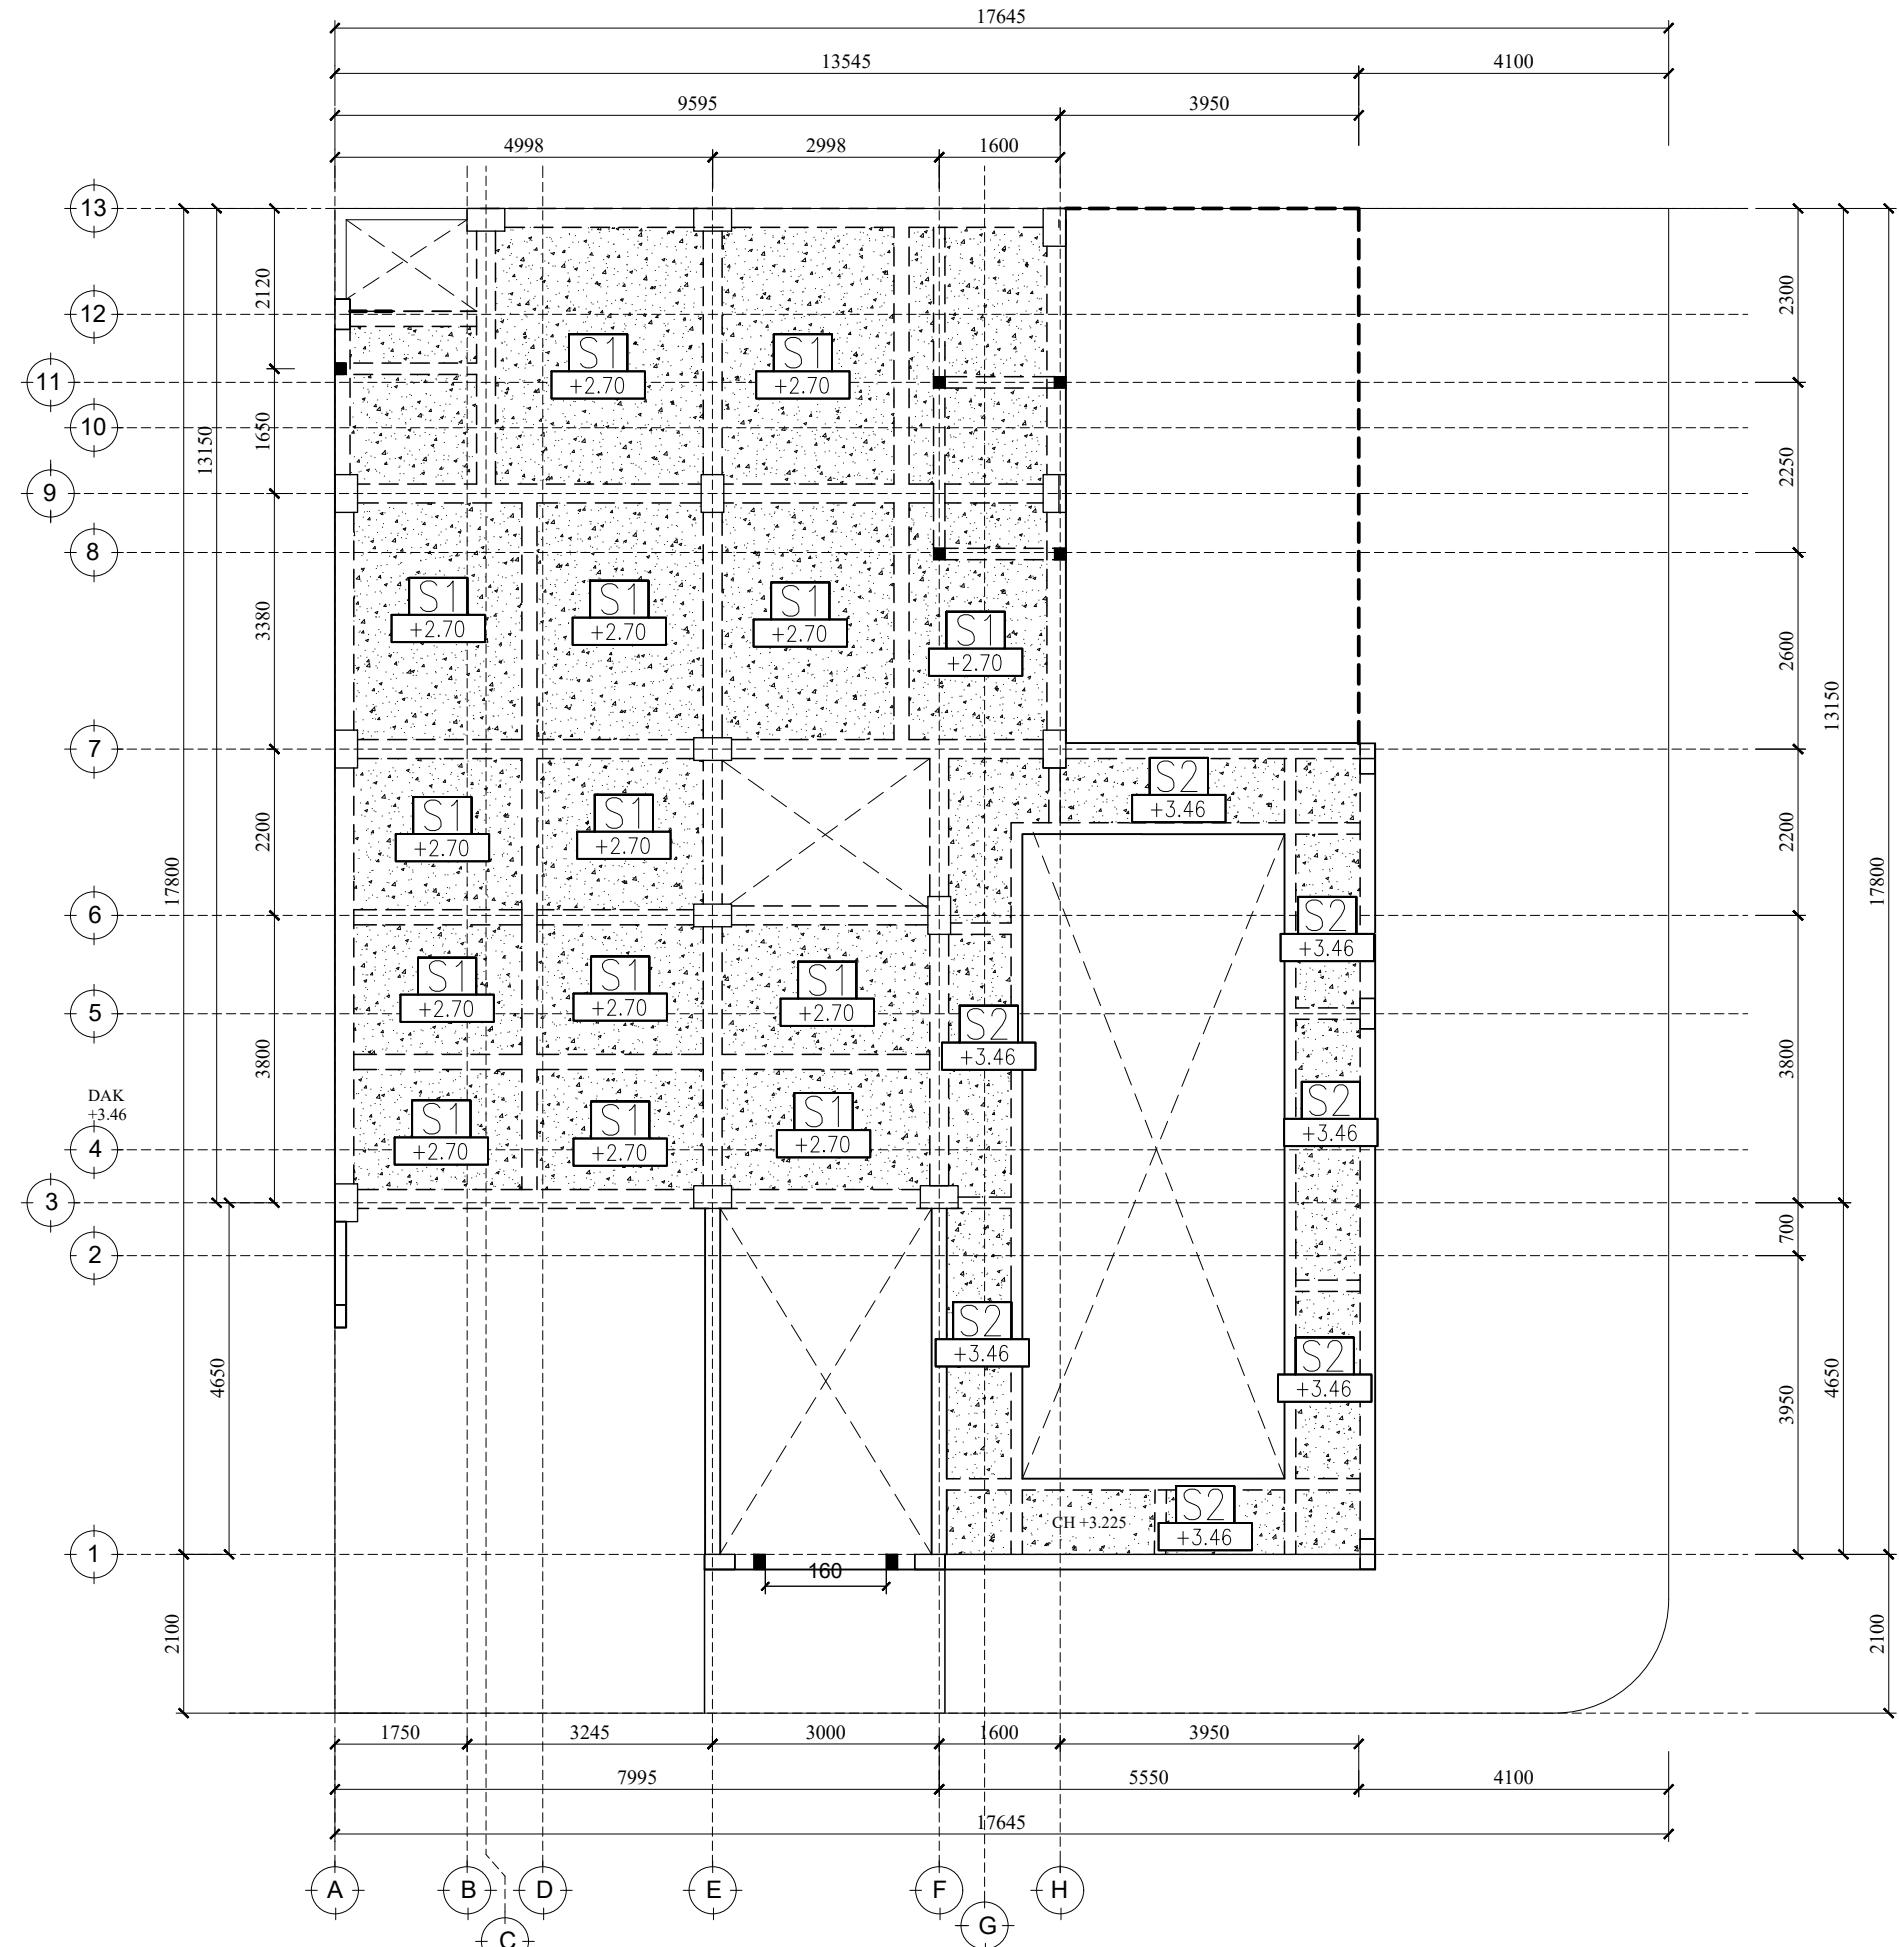





## 01 GROUND PLATFORM FLOOR PLAN

1:1

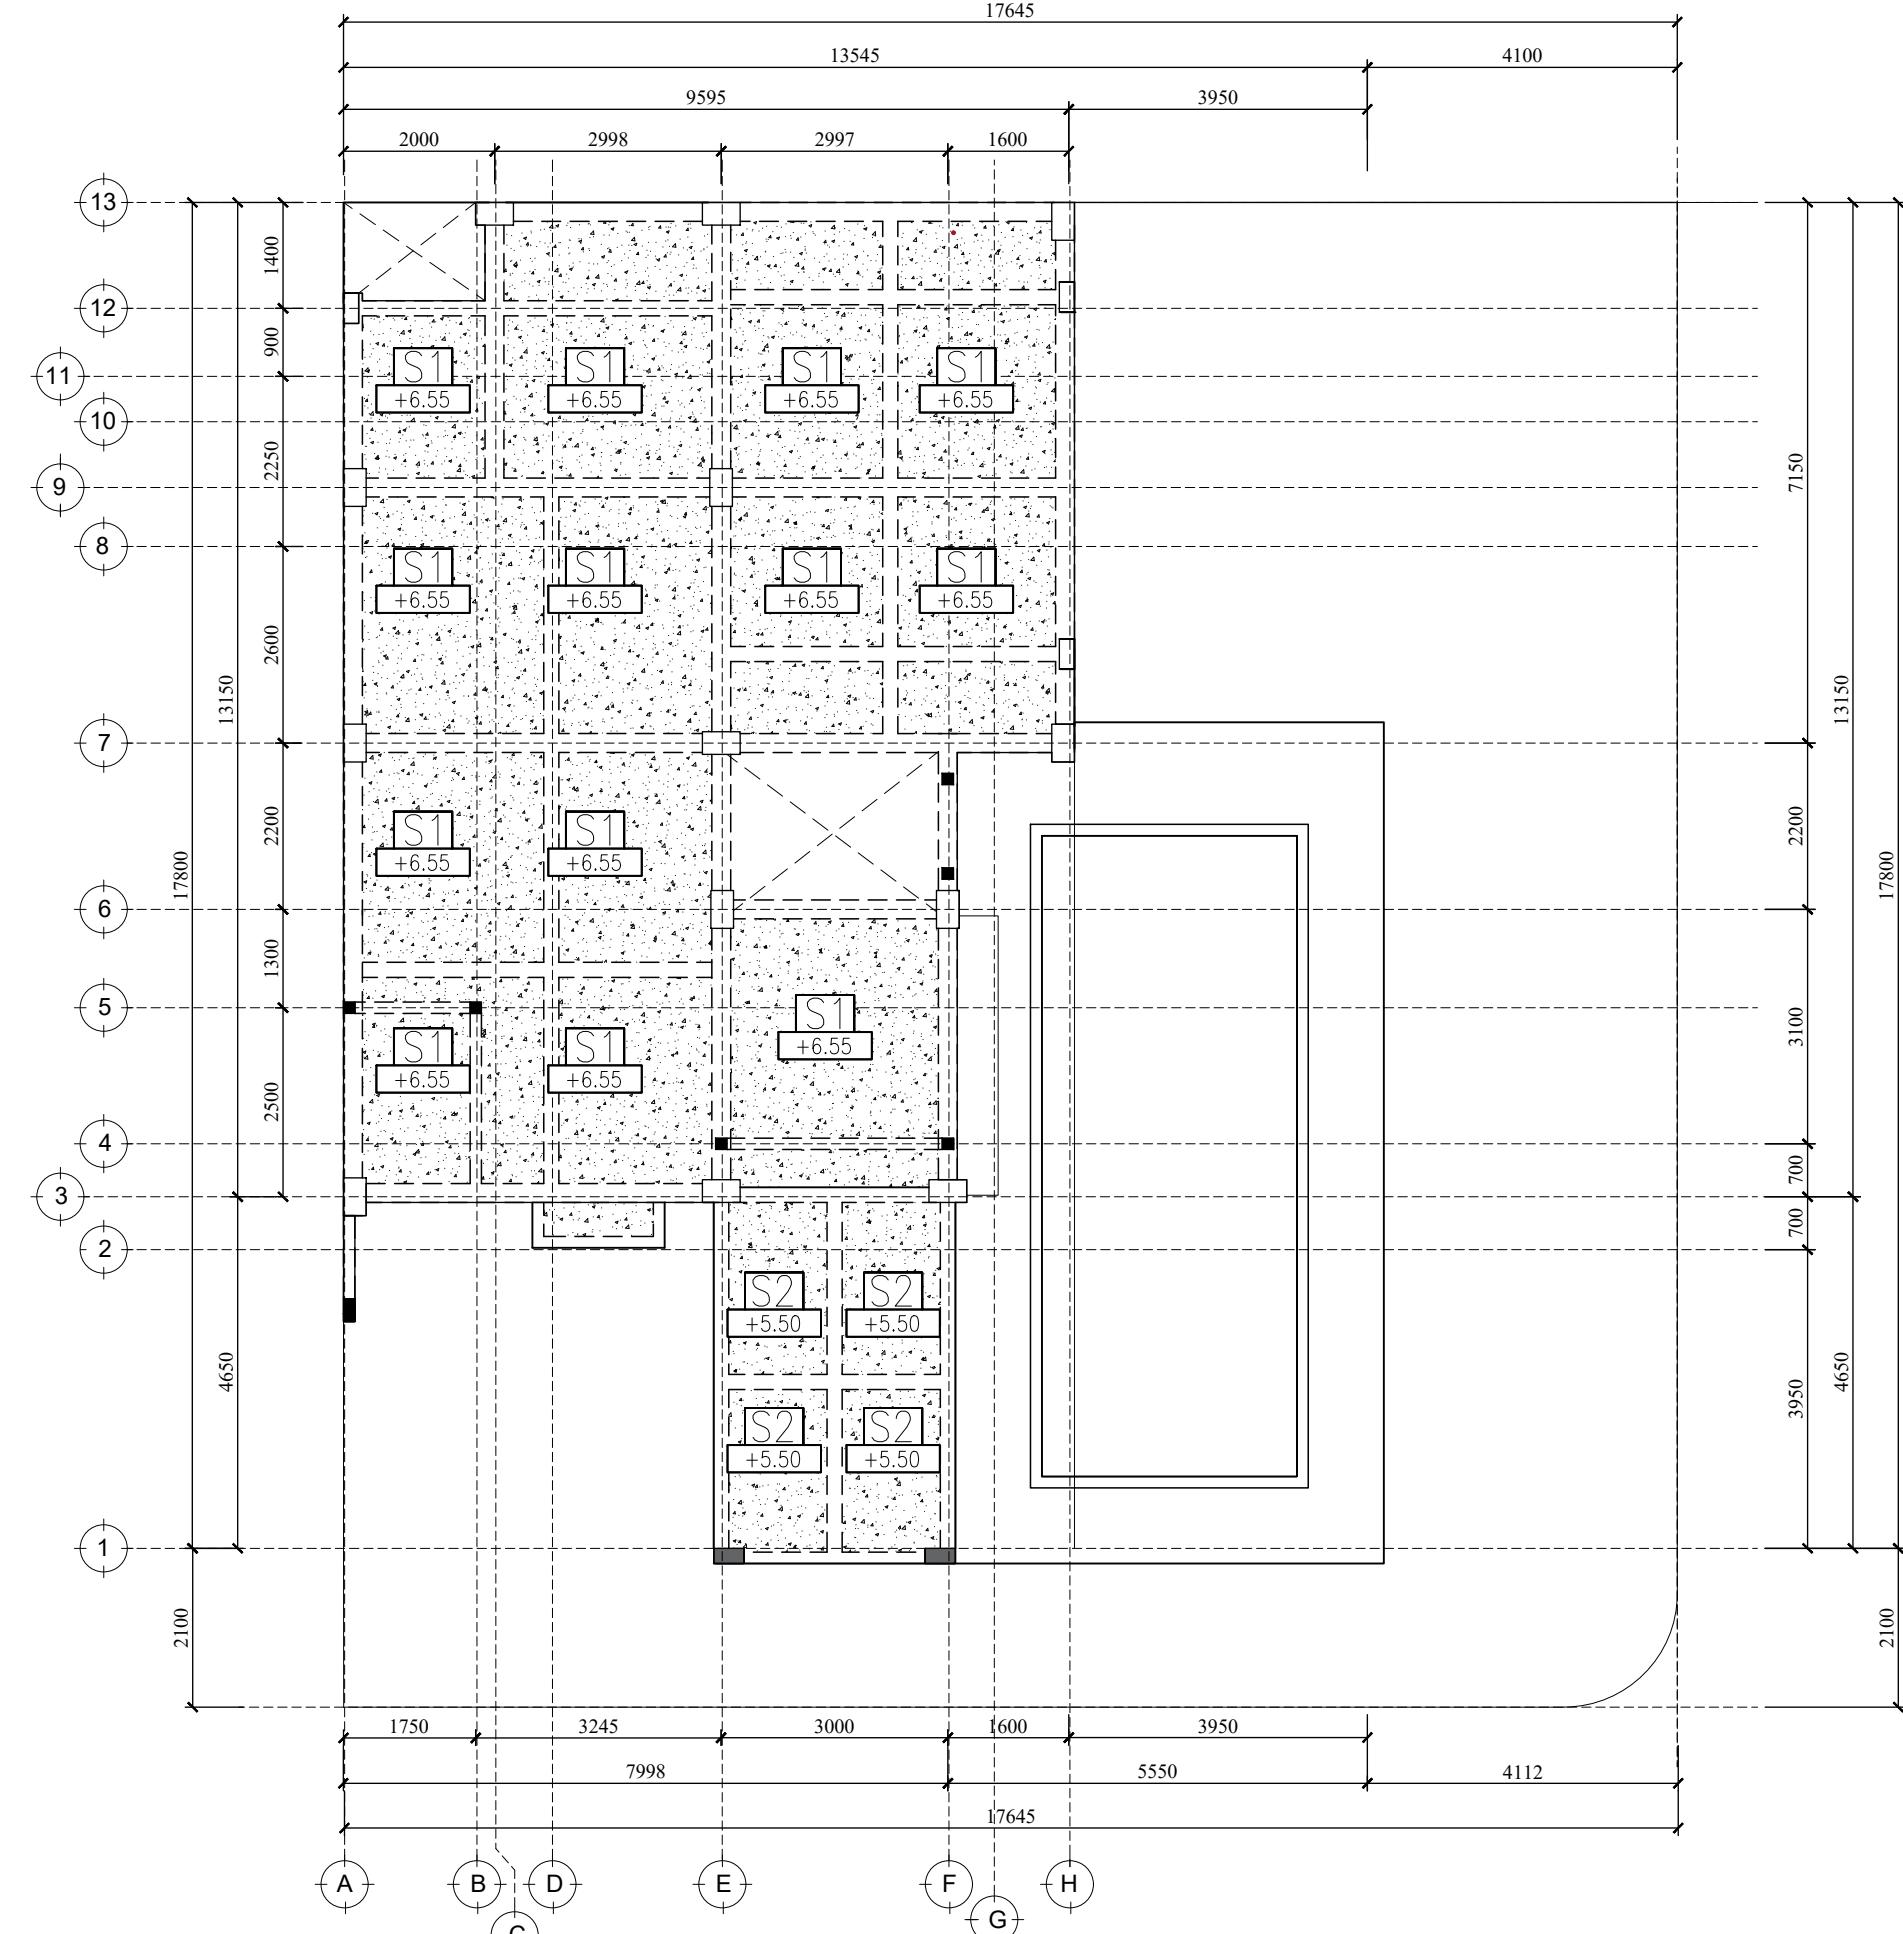


01 1ST PLATFORM FLOOR PLAN


1 : 1

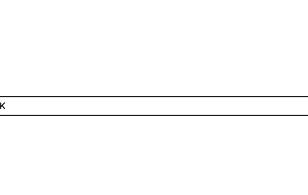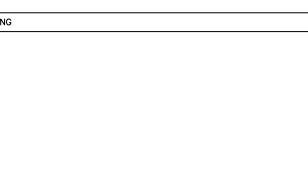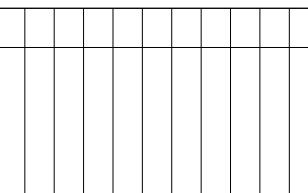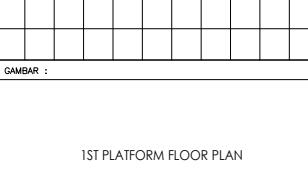NAMA PROYEK			
RESIDENTIAL HOUSE AKASIA 2 / 59			
CATATAN :			
<p>Semuas desain, rancangan dan kerja seni yang tertera pada gambar ini dilindungi oleh Undang-undang Huk. Cipta, serta hanya dipakai untuk yang telah ditentukan dan tidak boleh diperbarui tanpa ijin tertulis.</p> <p>Kontrak pelaksanaan pekerjaan memerlukan disetujui terhadap keadaan lapangan dan apabila ada ketidakcocokan harus dilaporkan kepada Arsitek.</p> <p>Gambar berdimensi tidak diperkenankan diambil.</p> <p>Sebaiknya pekerjaan dilakukan, kontraktor berkewajiban untuk meminta persetujuan gambar kerja dan contoh bahan dari Arsitek.</p>			
PEMBERI TUGAS			
			
ARSITEK			
			
ERIC HANDAYA, S.T I.A.I			
DRAFTING			
			
			
REVISI			
NO. TGL			
JUDUL GAMBAR :			
1ST PLATFORM FLOOR PLAN			
SKALA :		DIGAMBAR	TGL.
1:100		DIPERIKSA	TGL.
		DISETUJUI	TGL.
DISETUJUI PEMB. TUGAS			TGL. -
DIKELUARKAN UNTUK : FOR DESIGN DEVELOPMENT			
NO. PROYEK	NO. GAMBAR :	KODE GAMBAR :	REVISI :
	81	STR-14	

NAMA PROYEK		RESIDENTIAL HOUSE AKASIA 2 / 59		
CATATAN :		<p>Sama dengan rencana dan karya seni yang tertulis pada gambar ini dilindungi oleh Undang-undang Hak Cipta, serta hanya diperbolehkan untuk yang telah ditentukan dan tidak boleh diperbanyak tanpa ijin tertulis.</p> <p>Kontrak berlaku setelah memahami dimensi terhadap keadaan lapangan dan apabila ada ketidakcocokan harus disampaikan kepada Arsitek.</p> <p>Gambar berdimensi tidak diperkenankan diukur.</p> <p>Sebelum pengerjaan dimulai, kontraktor berkewajiban untuk meminta persetujuan gambar kerja dan contoh buah dari Arsitek.</p>		
PEMBERI TUGAS				
ARSITEK		ERIC HANDAYA, S.T I.A.I		
DRAFTING				
JUDUL GAMBAR :		2ND PLATFORM FLOOR PLAN		
SKALA :		DIGAMBAR	TGL.	TGL
1:100		DIPERIKSA	TGL.	
		DISETUJUI	TGL.	
		DISETUJUI PEMB. TUGAS		TGL. -
DIKELUARKAN UNTUK :		FOR DESIGN DEVELOPMENT		
NO. PROYEK	NO. GAMBAR :	KODE GAMBAR :	REVISI :	
	82	STR-15		

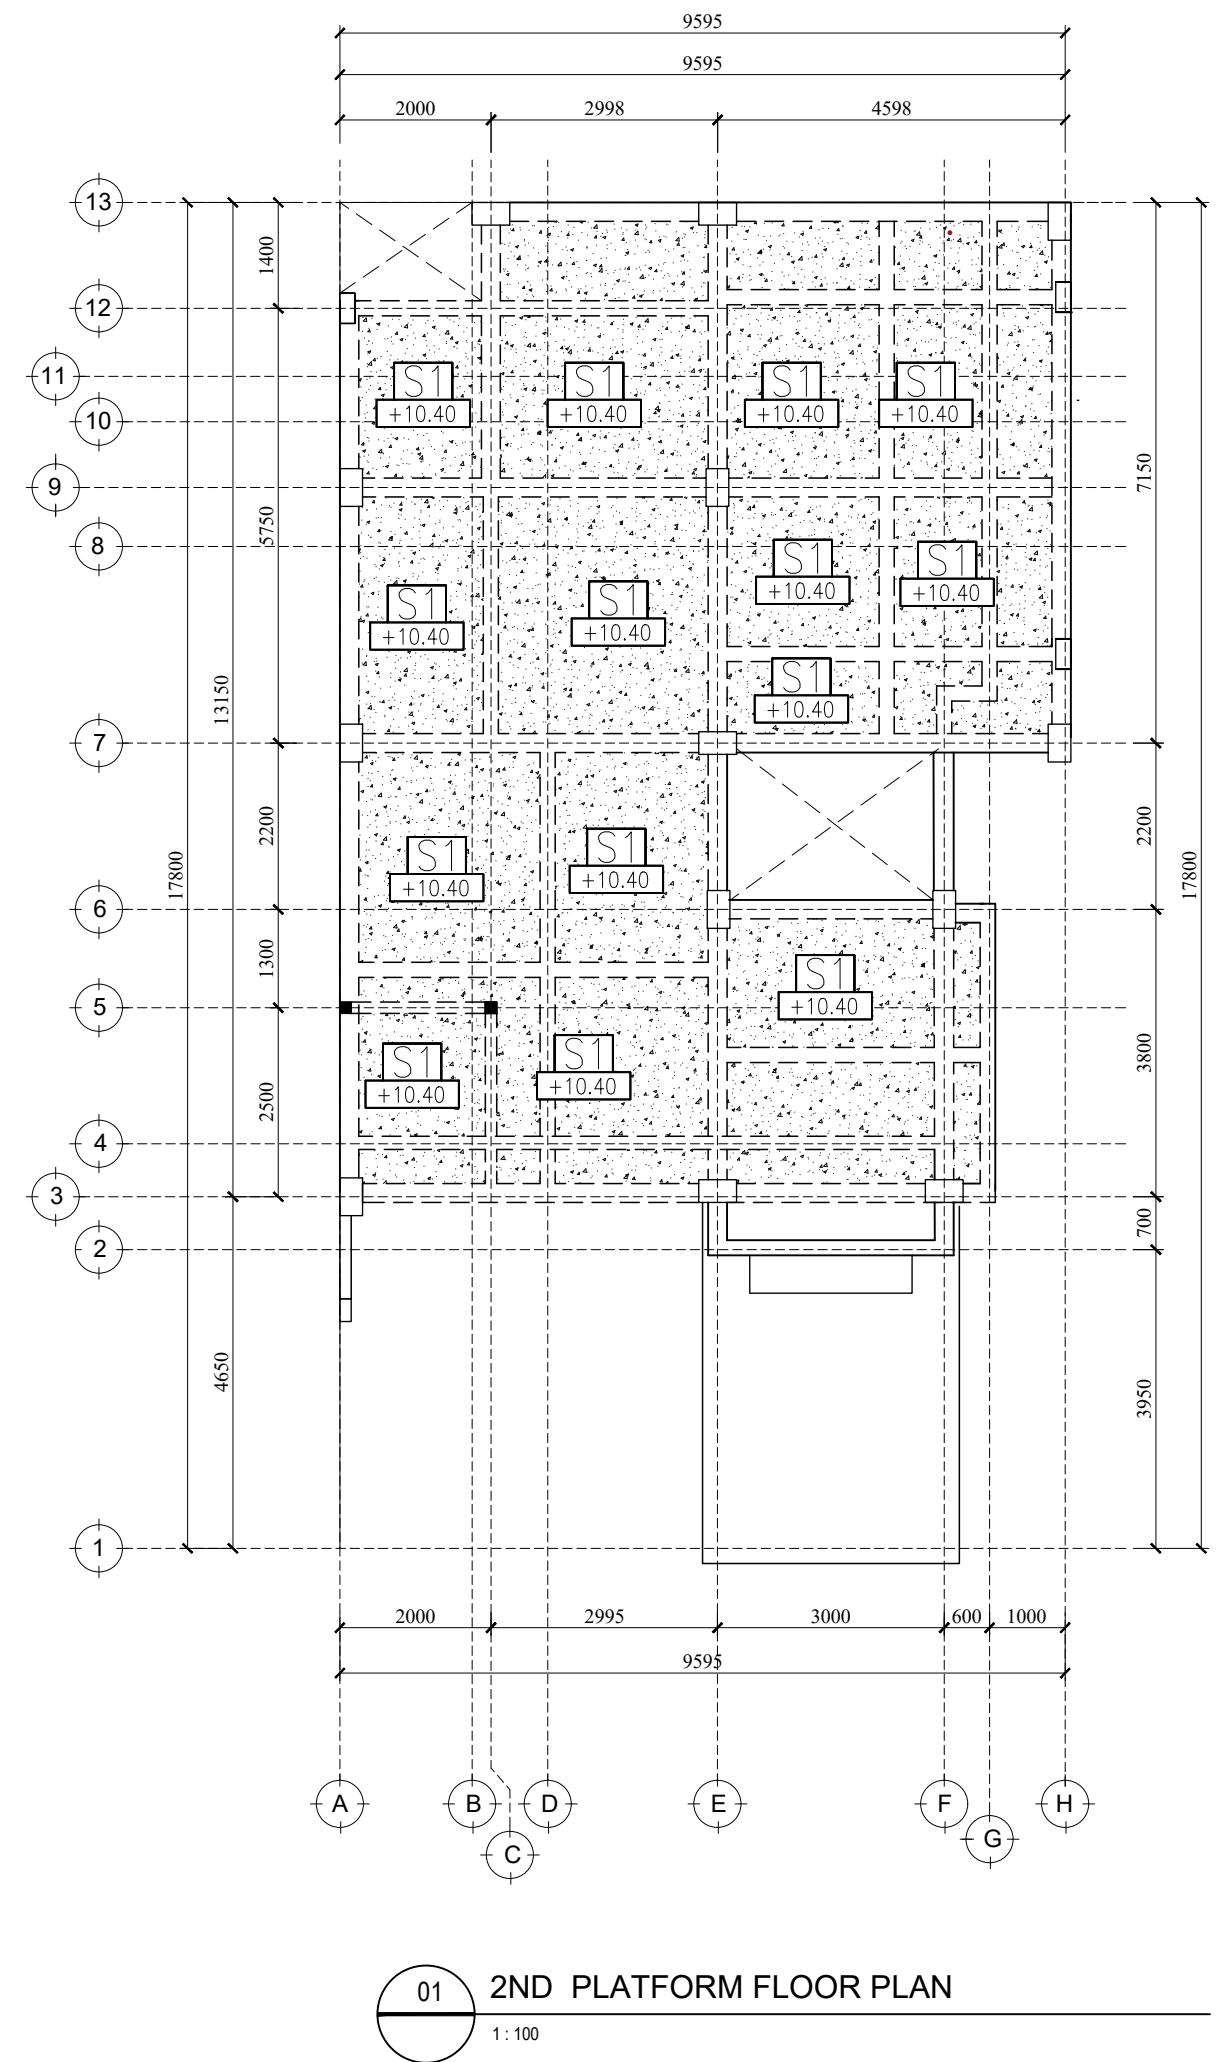

NAMA PROYEK	RESIDENTIAL HOUSE AKASIA 2 / 59		
CATATAN :	<p>Semua garis, retoran dan karya seni yang tertera pada gambar ini diilustrasi dan diperbaiki tanpa izin tertulis.</p> <p>Kontrak berlaku dengan menekuk dimensi terhadap keadaan lapangan dan apabila ada ketidakcocokan harus disepakati kepada Arsitek.</p> <p>Gambar berdimensi tidak diperkenankan diambil.</p> <p>Sebelum pengerjaan dilaksanakan, kontraktor berwajib untuk meminta persetujuan gambar kerja dan contoh buah dari Arsitek.</p>		
PEMBERI TUGAS			
ARSITEK	ERIC HANDAYA, S.T I.A.I		
DRAFTING			
JUDUL GAMBAR :	ROOF PLATFORM FLOOR PLAN		
SKALA :	DIGAMBAR	TGL.	TGL
1:100			
DIPERIKSA		TGL.	
DISETUJUI		TGL.	
DIKELUARKAN UNTUK :	FOR DESIGN DEVELOPMENT		
NO. PROYEK	NO. GAMBAR :	KODE GAMBAR :	REVISI :
	83	STR-16	

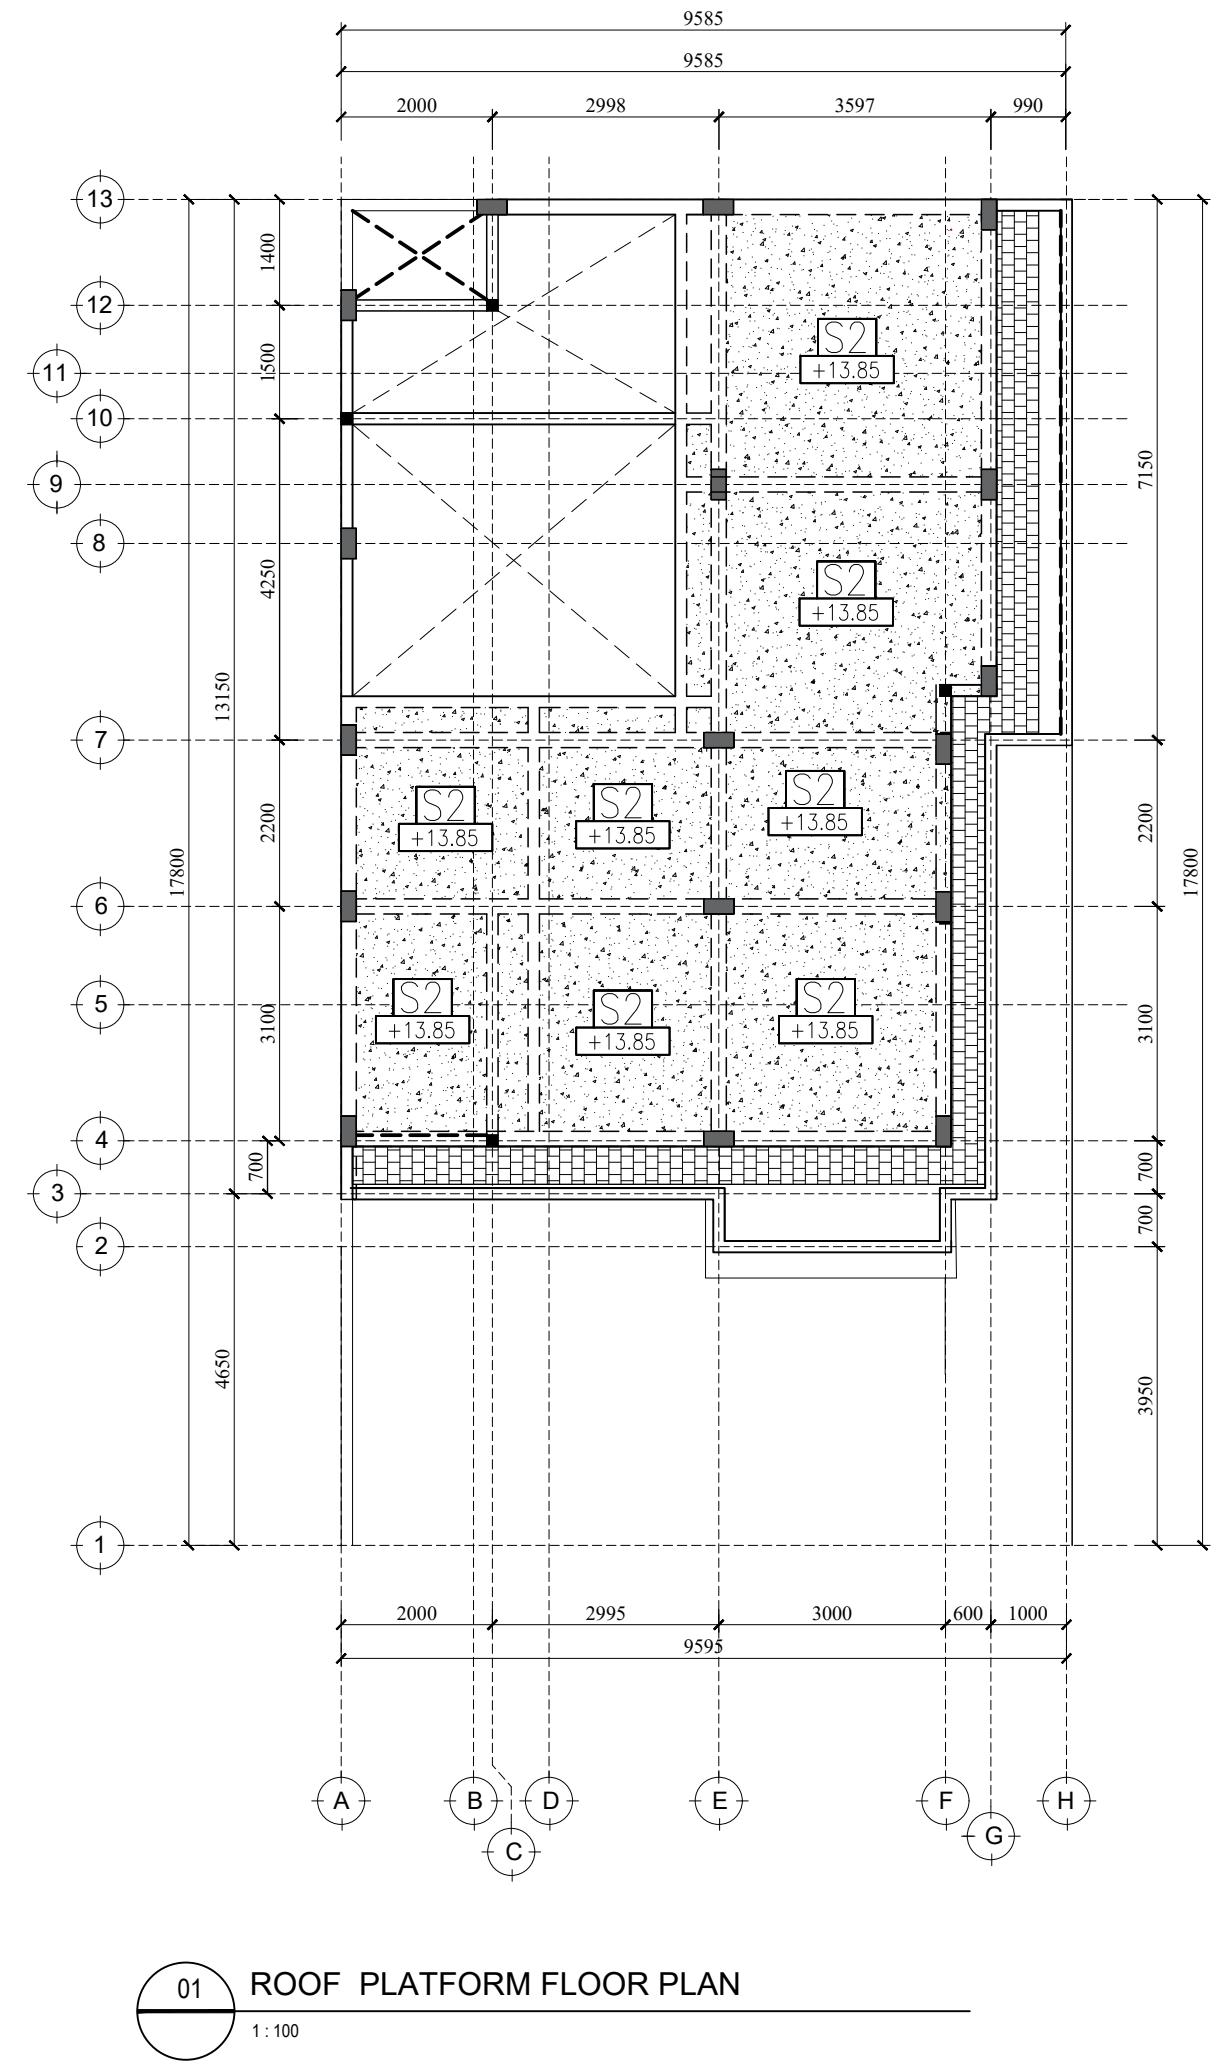

## DETAIL PEMBESIAN BALOK & TIE BEAM

NOTASI	B1		BA		B3		B4		B5	
	Tump.	Lap.	Tump.	Lap.	Tump.	Lap.	Tump.	Lap.	Tump.	Lap.
GAMBAR										
DIMENSI (MM)	250X500	250X500	200X300	200X300	250X400	250X400	200X400	200X400	150X350	150X350
TUL.ATAS	5 D16	3 D16	3 D16	2 D16	3 D16	2 D16	4 D16	4 D16	4 D13	4 D13
TUL.SAMPING	4 D13	4 D13	2 D13	2 D13	-	-	2 D10	2 D10	2 D10	2 D10
TUL.BAWAH	3 D16	5 D16	2 D16	3 D16	2 D16	3 D16	2 D16	2 D16	2 D13	2 D13
SENGKANG	2 D10-90	2 D10-140	2 D10-70	2 D10-110	2 D10-70	2 D10-110	2 D10-100	2 D10-100	2 D8-100	2 D8-100
NOTASI	B6		B6k		BAK		TIE BEAM			
	Tump.	Lap.	Tump.	Lap.	Tump.	Lap.				
GAMBAR										
DIMENSI (MM)	150X300	150X300	150X250	150X250	200X400	200X400				
TUL.ATAS	2 D13	2 D13	4 D13	4 D13	4 D13	4 D13				
TUL.SAMPING	-	-	-	-	-	-				
TUL.BAWAH	2 D13	2 D13	2 D13	2 D13	2 D13	2 D13				
SENGKANG	2 D8-100	2 D8-120	2 D8-100	2 D8-100	2 D10-100	2 D10-100				

## DETAIL PEMBESIAN KOLOM

NOTASI	K1A		K1B		K1C		K1D	K2	K3
	Tump.	Lap	Tump.	Lap	Tump.	Lap			
GAMBAR									
DIMENSI (MM)	300X500	300X500	300X500	300X500	300X500	300X500	150x350	400X200	300X150
TUL. UTAMA	12 D19	12 D19	10 D19	10 D19	8 D16	8 D16	8 D13	4 D16+4 D13	6 D13
SENGKANG	3 D10-150	2 D10-150	3 D10-150	2 D10-150	3 D10-150	2 D10-150	2 D8-50	2 D10-150	2 D8-150

NAMA PROYEK	RESIDENTIAL HOUSE AKASIA 2 / 59		
CATATAN :	<p>Semua detail, rencangan dan karya seni yang tertera pada gambar ini diilustrasi dan diketahui teknis dan akurat. Serta hanya diperlukan untuk yang telah ditentukan dan tidak boleh diperbaiki tanpa ijin tertulis.</p> <p>Kontrak berlaku selama memenuhi dimensi terhadap keadaan lapangan dan apabila ada ketidaksesuaian harus disampaikan kepada Arsitek.</p> <p>Gambar berdimensi tidak diperkenankan diskusi.</p> <p>Sebelum pekerjaan dilaksanakan, kontraktor berkewajiban untuk meminta persetujuan gambar kerja dan contoh bukti dari Arsitek.</p>		
PEMBERI TUGAS			
ARSITEK			
ERIC HANDAYA, S.T I.A.I			
DRAFTING			
REVISI :			
TOL			
NO.			
JUDUL GAMBAR :			
REINFORCING			
SKALA :	DIGAMBAR	TGL.	
1:5			
DIPERIKSA		TGL.	
DISETUJUI		TGL.	
DIKELUARKAN UNTUK :	FOR DESIGN DEVELOPMENT		
NO. PROYEK	NO. GAMBAR :	KODE GAMBAR :	REVISI :
	84		STR-17