

NAMA PROYEK			
RESIDENTIAL HOUSE AKASIA 2 / 59			
CATATAN :			
PEMBERI TUGAS			
ARSITEK			
DRAFTING			
			TDT
			R E V I S I
			TGL
			NO.
JUDUL GAMBAR :			
SKALA :	DIGAMBAR	TGL.	
	DIPERIKSA	TGL.	
	DISETUJUI	TGL.	
DISETUJUI PEMB. TUGAS		TGL.	-
DIKELUARKAN UNTUK : FOR DESIGN DEVELOPMENT			
NO. PROYEK	NO. GAMBAR :	KODE GAMBAR :	REVISI :

Architectural floor plan of a house with the following dimensions and room labels:

- Overall Dimensions:**
 - Width: 9516
 - Height: 6934
- Room Labels:**
 - DRYKITCHEN
 - DINNINGAREA
 - LIVINGROOM
 - TANGGA
 - FOYER
 - BATHROOM
 - TERAS
- Internal Dimensions (Horizontal):**
 - 1929 (Top Left)
 - 6059 (Top Center)
 - 1526 (Top Right)
 - 1686 (Bottom Left)
 - 3354 (Bottom Center-Left)
 - 2950 (Bottom Center-Right)
 - 1526 (Bottom Right)
 - 9514 (Bottom Total)
- Internal Dimensions (Vertical):**
 - 1503 (Left Top)
 - 5431 (Left Center)
 - 3699 (Left Bottom)
 - 2581 (Left Far Bottom)
 - 2004 (Right Top)
 - 3600 (Right Center)
 - 1576 (Right Bottom)
- Grid Lines:**
 - Horizontal: A, B, C, D, E, F
 - Vertical: 1, 2, 3, 4, 5, 6

01 1ST FLOOR PLAN
1:100

RESIDENTIAL HOUSE AKASIA 2 / 59

CATATAN :

PEMBERI TUGAS


ARSITEK

DRAFTING


[illegible]

JUDUL GAMBAR :

SKALA :	DIGAMBAR		TGL.	
	DIPERIKSA		TGL.	
	DISETUJUI		TGL.	
DISETUJUI PEMB. TUGAS			TGL.	—
DIKELUARKAN UNTUK : FOR DESIGN DEVELOPMENT				
NO. PROYEK	NO. GAMBAR :	KODE GAMBAR :		REVISI :

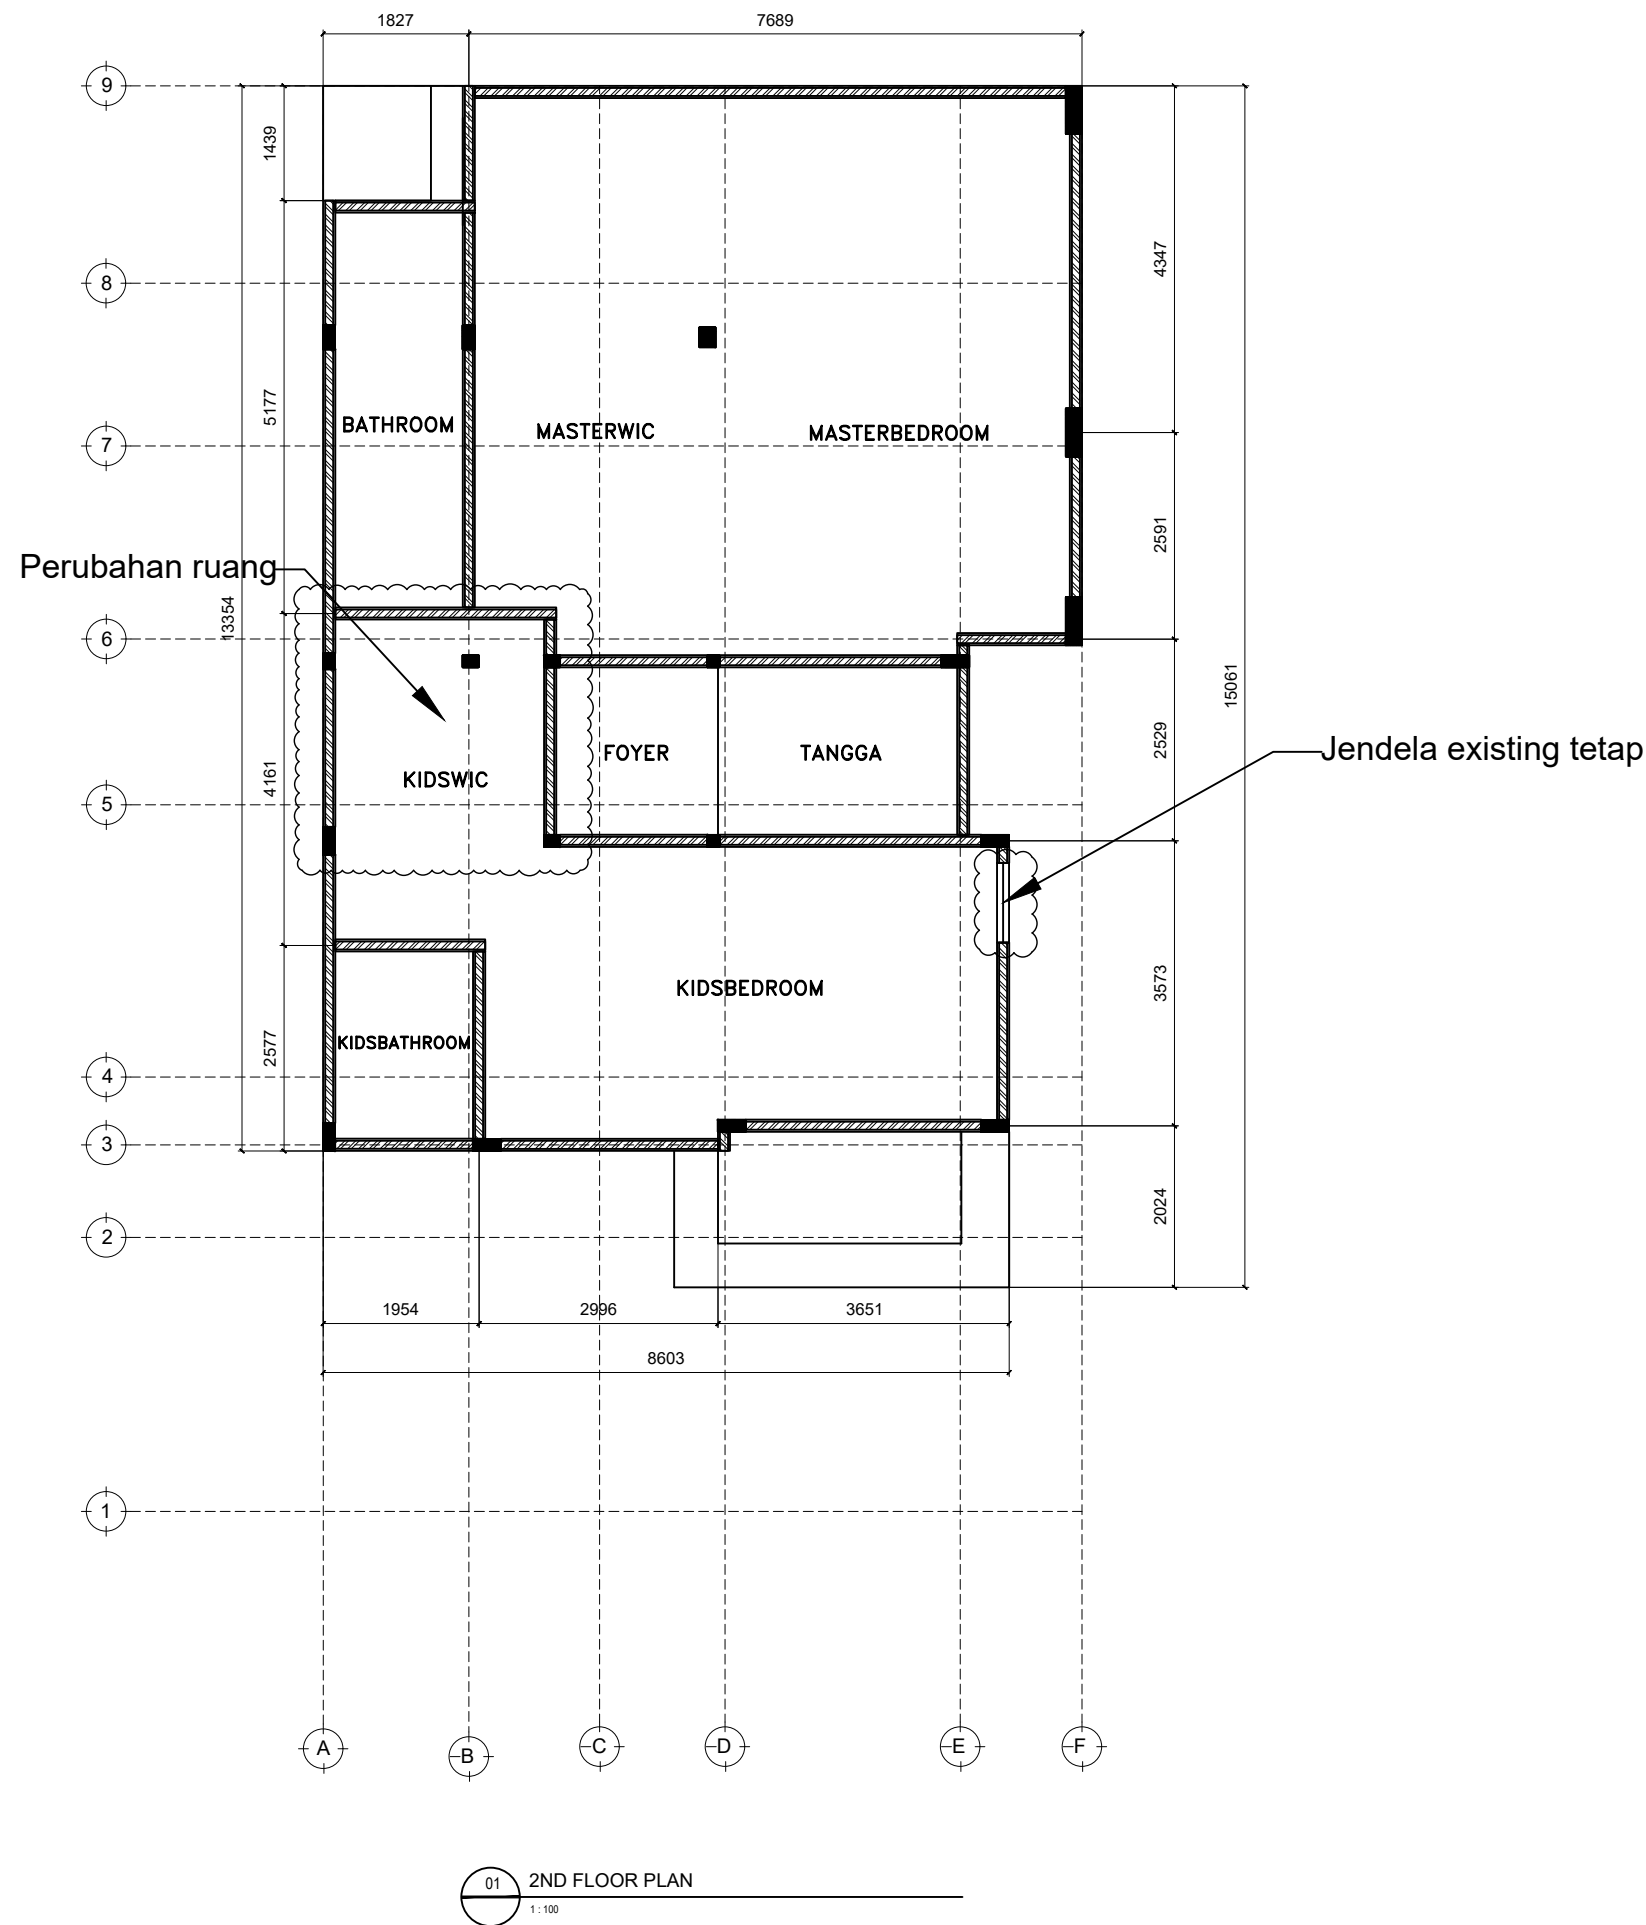

NAMA PROYEK			
RESIDENTIAL HOUSE AKASIA 2 / 59			
CATATAN :			
PEMBERI TUGAS			
ARSITEK			
DRAFTING			
			TDT
			R E V I S I
			TGL
			NO.
JUDUL GAMBAR :			
SKALA :	DIGAMBAR	TGL.	
	DIPERIKSA	TGL.	
	DISETUJUI	TGL.	
DISETUJUI PEMB. TUGAS		TGL.	-
DIKELUARKAN UNTUK : FOR DESIGN DEVELOPMENT			
NO. PROYEK	NO. GAMBAR :	KODE GAMBAR :	REVISI :

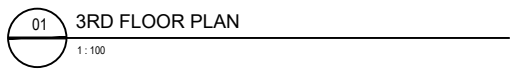

NAMA PROYEK												
RESIDENTIAL HOUSE AKASIA 2 / 59												
CATATAN :												
PEMBERI TUGAS												
ARSITEK												
DRAFTING												
												TDT
												R E V I S I
												TGL
												NO.
JUDUL GAMBAR :												
SKALA :		DIGAMBAR		TGL.								
		DIPERIKSA		TGL.								
		DISETUJUI		TGL.								
DISETUJUI PEMB. TUGAS				TGL.	-							
DIKELUARKAN UNTUK : FOR DESIGN DEVELOPMENT												
NO. PROYEK	NO. GAMBAR :		KODE GAMBAR :			REVISI :						