



NAMA PROYEK	RESIDENTIAL HOUSE AKASIA 2 / 59		
CATATAN :			
PEMBERI TUGAS			
ARSITEK			
DRAFTING			
JUDUL GAMBAR :			
SKALA :	DIGAMBAR	TGL.	
	DIPERIKSA	TGL.	
	DISETUJUI	TGL.	
DISETUJUI PEMB. TUGAS			TGL. -
DIKELUARKAN UNTUK : FOR DESIGN DEVELOPMENT			
NO. PROYEK	NO. GAMBAR :	KODE GAMBAR :	REVISI :

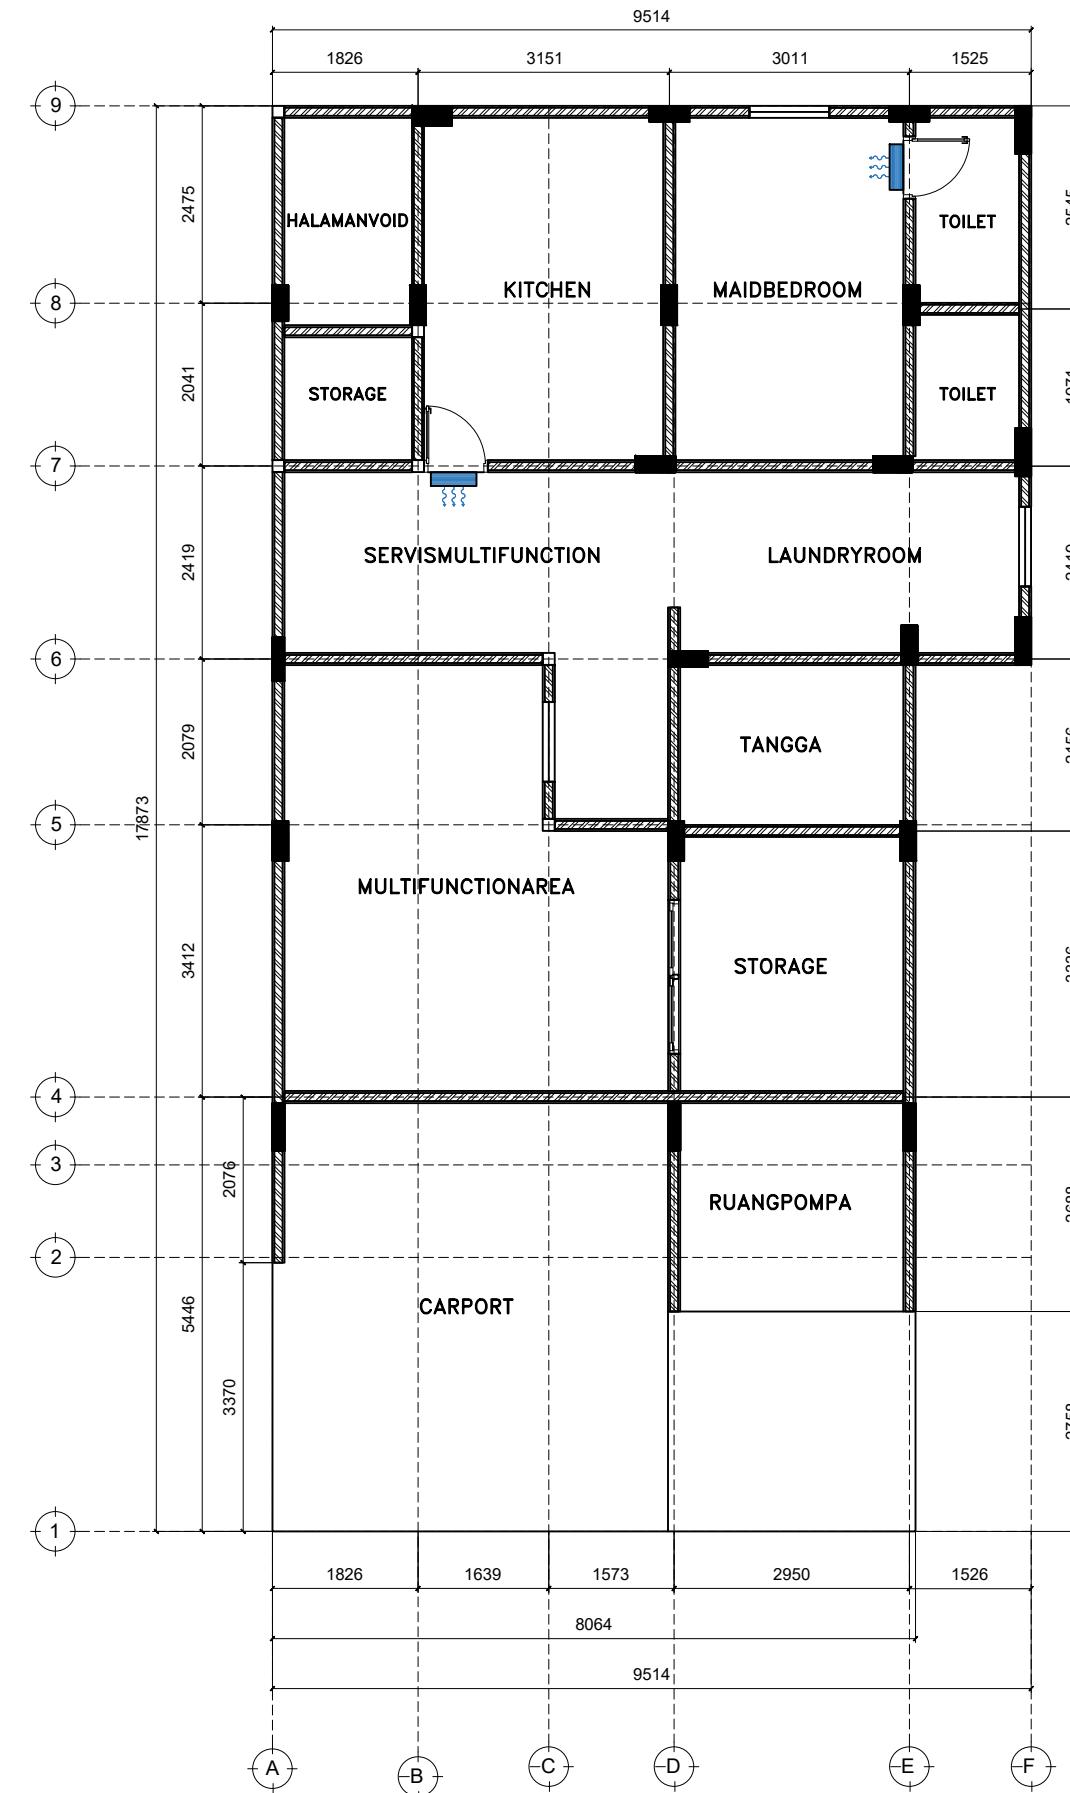


01 GROUND FLOOR PLAN  
1:100

NAMA PROYEK	RESIDENTIAL HOUSE AKASIA 2 / 59		
CATATAN :			
PEMBERI TUGAS			
ARSITEK			
DRAFTING			
JUDUL GAMBAR :			
SKALA :	DIGAMBAR	TGL.	
	DIPERIKSA	TGL.	
	DISETUJUI	TGL.	
DISETUJUI PEMB. TUGAS			TGL. -
DIKELUARKAN UNTUK : FOR DESIGN DEVELOPMENT			
NO. PROYEK	NO. GAMBAR :	KODE GAMBAR :	REVISI :

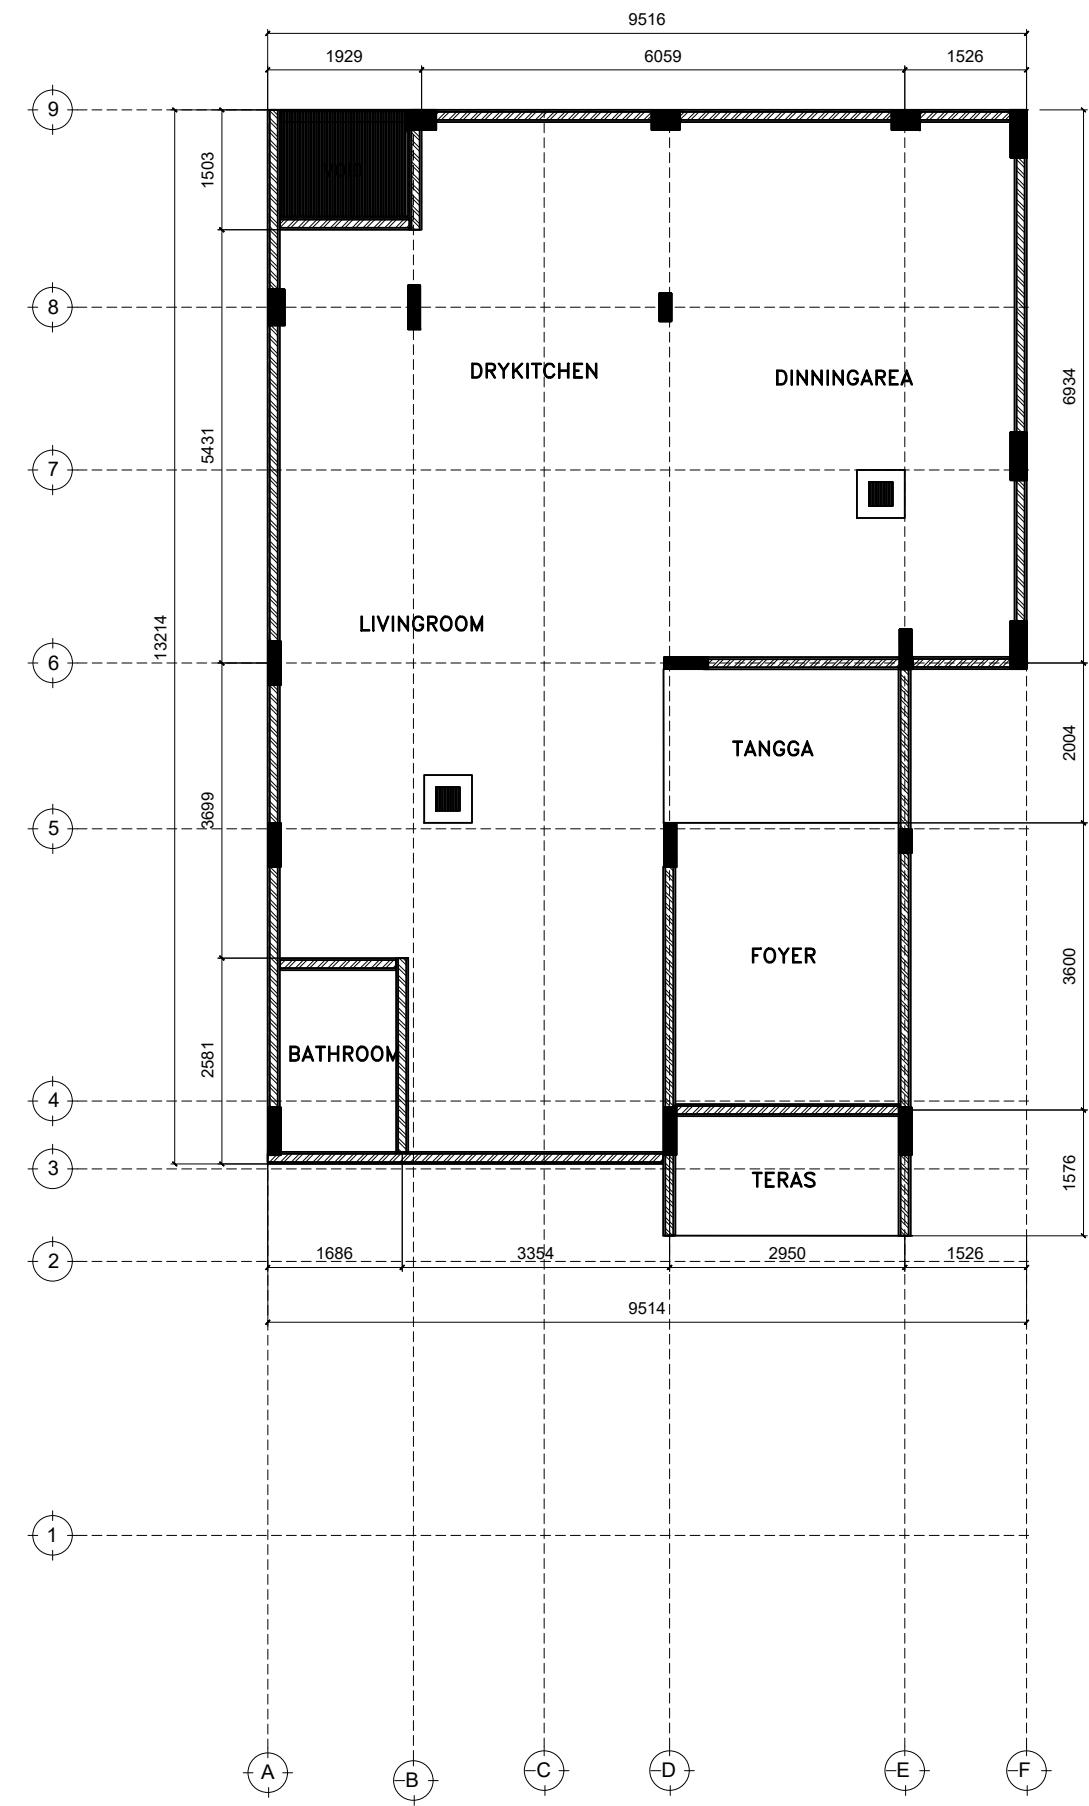


NAMA PROYEK	RESIDENTIAL HOUSE AKASIA 2 / 59		
CATATAN :			
PEMBERI TUGAS			
ARSITEK			
DRAFTING			
JUDUL GAMBAR :			
SKALA :	DIGAMBAR	TGL.	
	DIPERIKSA	TGL.	
	DISETUJUI	TGL.	
DISETUJUI PEMB. TUGAS			TGL. -
DIKELUARKAN UNTUK : FOR DESIGN DEVELOPMENT			
NO. PROYEK	NO. GAMBAR :	KODE GAMBAR :	REVISI :

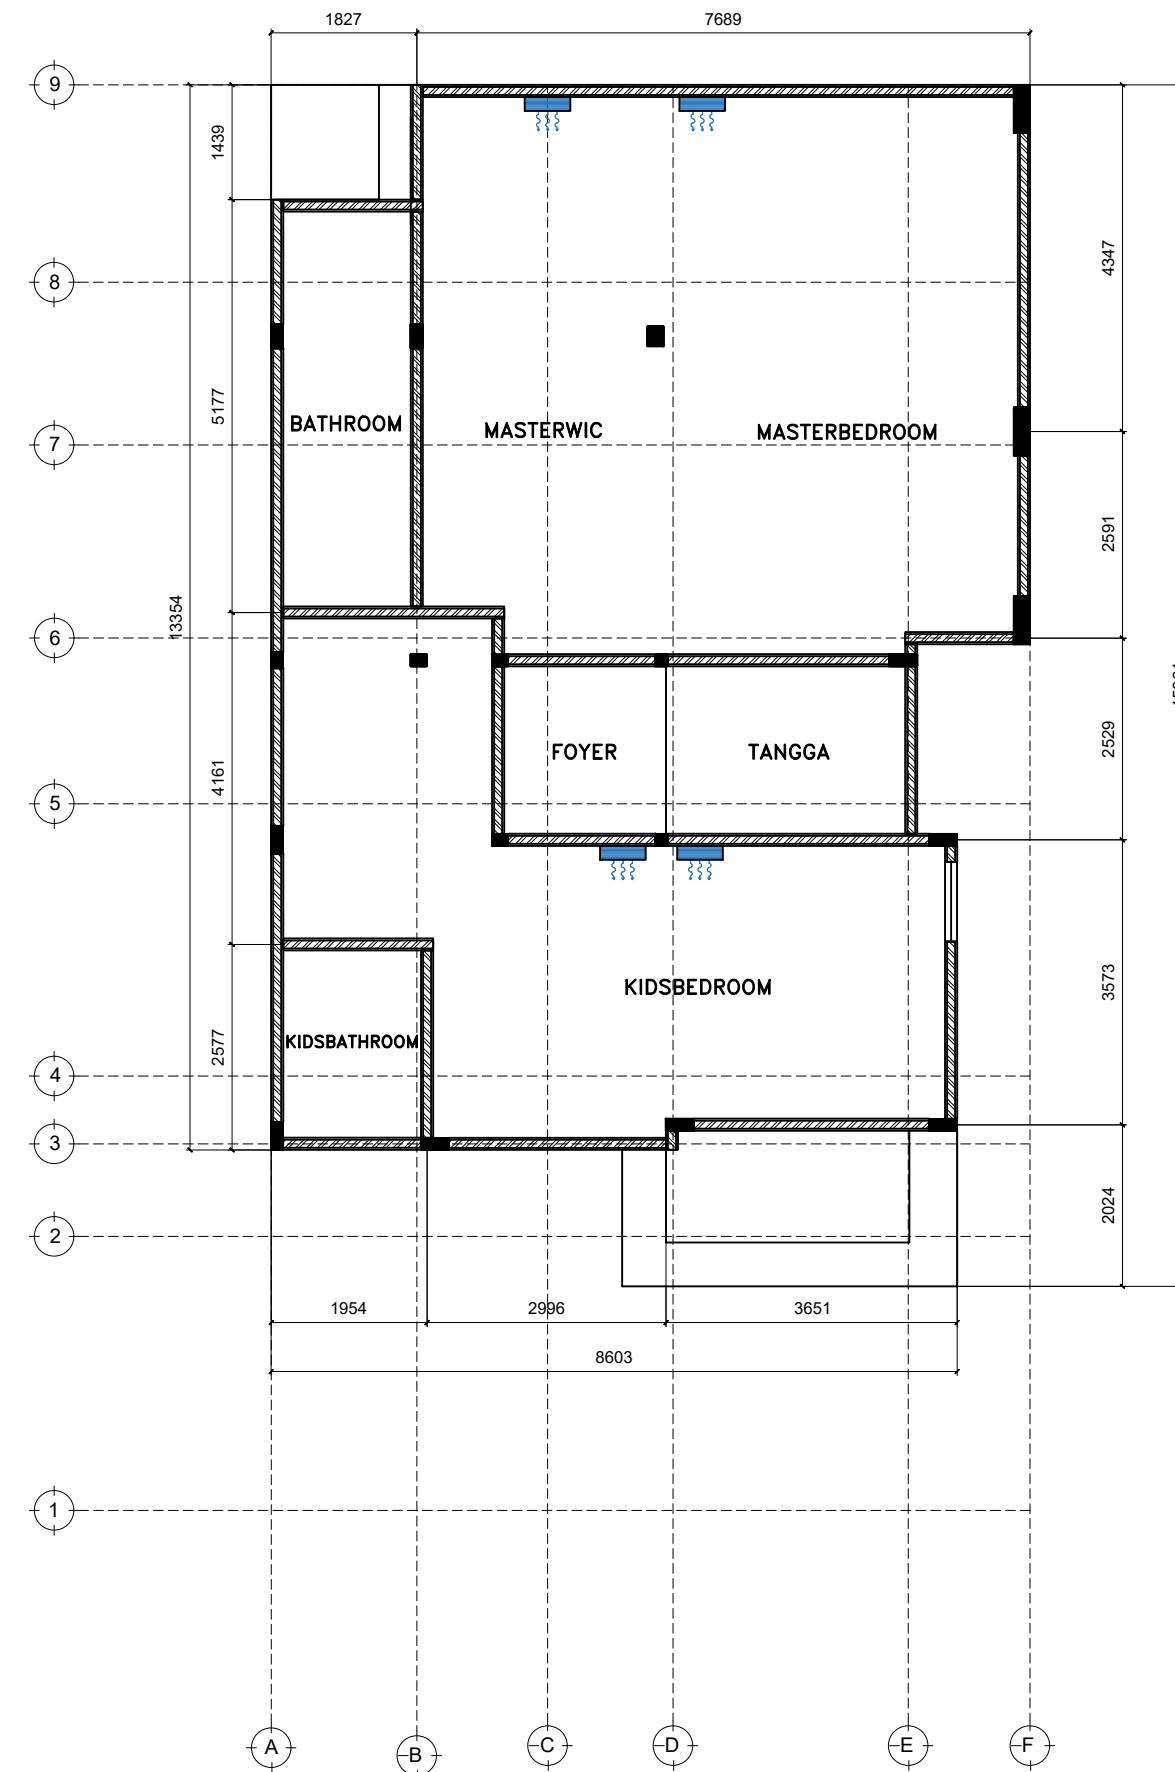

01 2ND FLOOR PLAN  
1:100

NAMA PROYEK	RESIDENTIAL HOUSE AKASIA 2 / 59		
CATATAN :			
PEMBERI TUGAS			
ARSITEK			
DRAFTING			
JUDUL GAMBAR :			
SKALA :	DIGAMBAR	TGL.	
	DIPERIKSA	TGL.	
	DISETUJUI	TGL.	
DIKELUARKAN UNTUK :	FOR DESIGN DEVELOPMENT		
NO. PROYEK	NO. GAMBAR :	KODE GAMBAR :	REVISI :

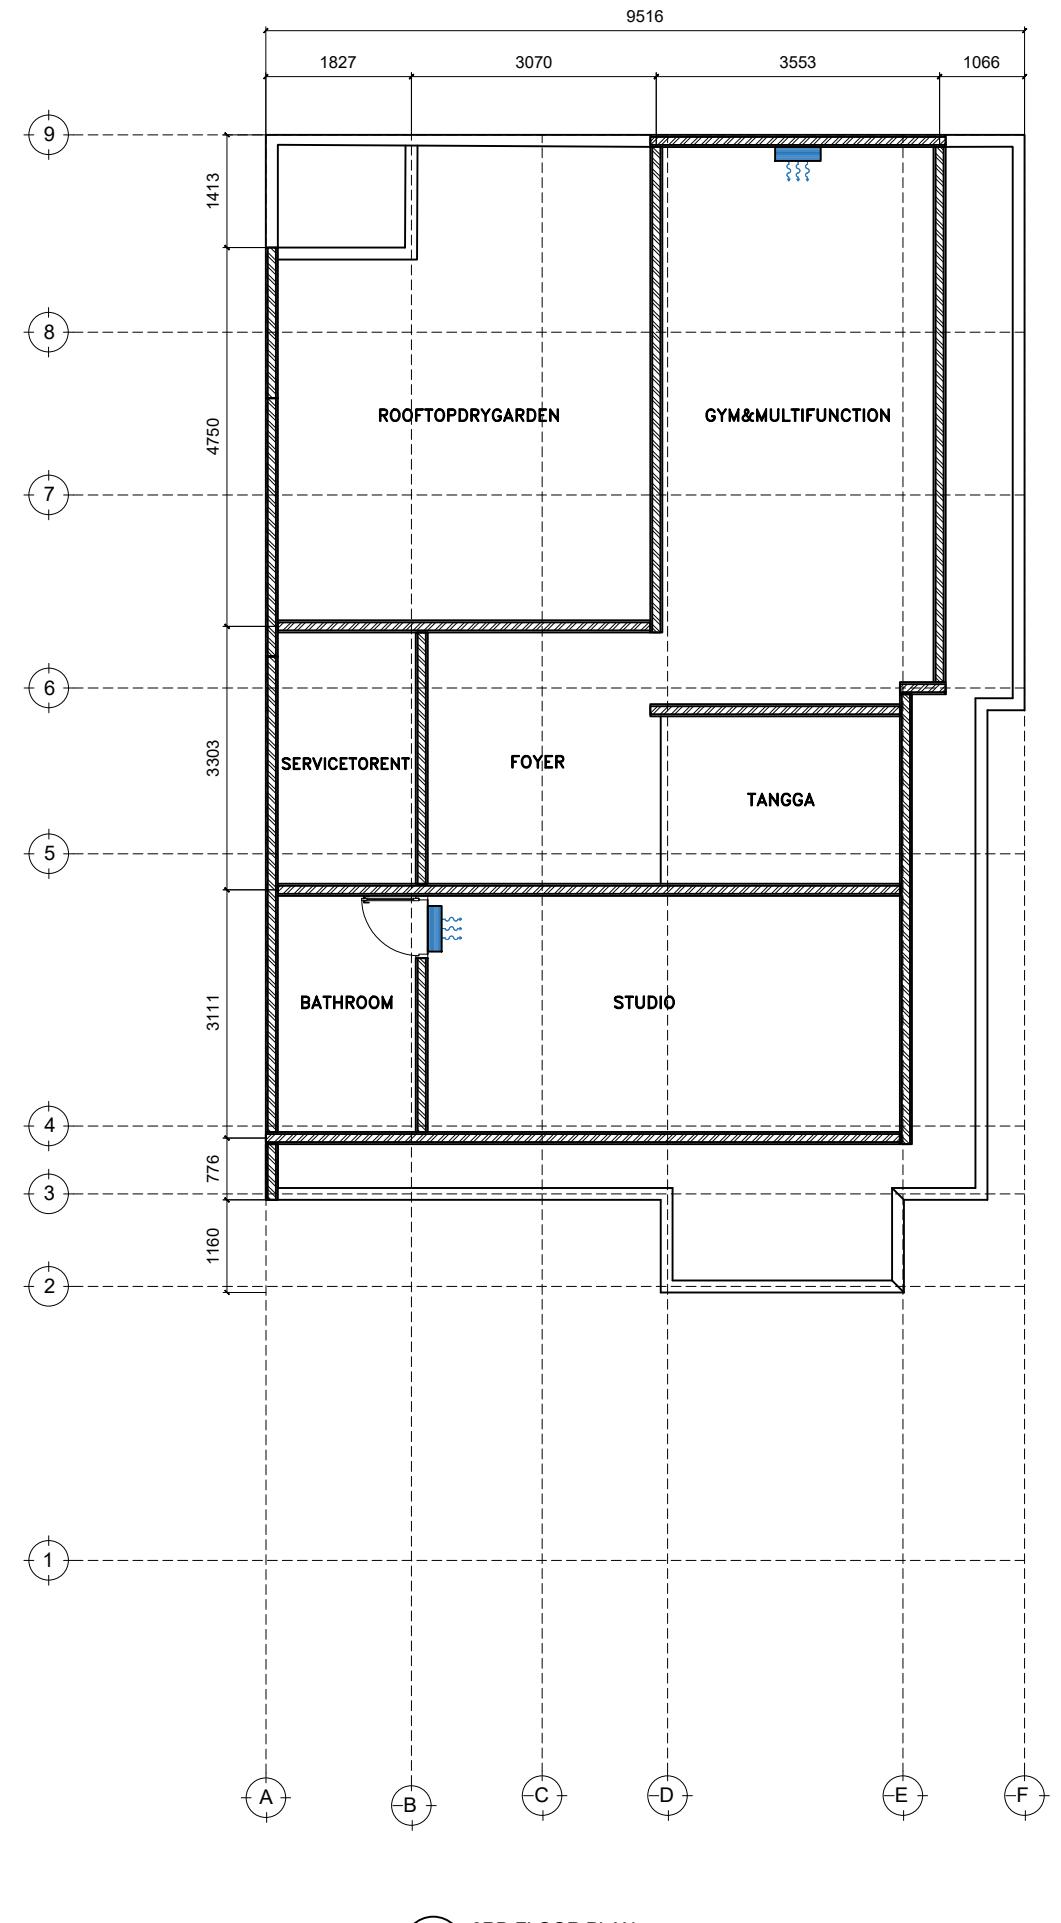

01 3RD FLOOR PLAN  
1:100