




NAMA PROYEK	RESIDENTIAL HOUSE AKASIA 2 / 59		
CATATAN :	<p>Sama dengan rencangan dan karya seni yang tertulis pada gambar ini dilindungi oleh Undang-undang Hukum Cipta, serta hanya diperbolehkan untuk yang telah ditentukan dan tidak boleh diperbanyak tanpa ijin tertulis.</p> <p>Kontrakor berwenang untuk memerlukan dimensi terhadap keadaan lapangan dan apabila ada ketidakcocokan harus disampaikan kepada Arsitek.</p> <p>Gambar berdimensi tidak diperkenankan diakses.</p> <p>Sebelum pengerjaan dimulai, kontraktor berkewajiban untuk meminta persetujuan gambar kerja dan contoh buah dari Arsitek.</p>		
PEMBERI TUGAS			
ARSITEK			
ERIC HANDAYA, S.T I.A.I			
DRAFTING			
R E V I S I			
TOL			
NO.			
JUDUL GAMBAR :			
FOUNDATION DETAILS TYPE F3			
FOUNDATION DETAILS TYPE F4			
SKALA : 1:25	DIGAMBAR	TGL.	
DIPERIKSA		TGL.	
DISETUJUI		TGL.	
DIKELUARKAN UNTUK :	FOR DESIGN DEVELOPMENT		
NO. PROYEK	NO. GAMBAR :	KODE GAMBAR :	REVISI :
	71	STR-04	

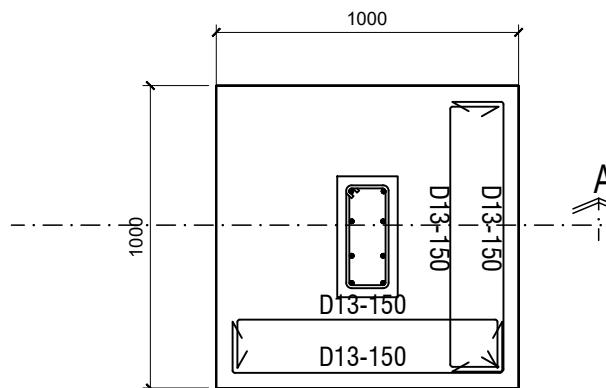


FOUNDATION DETAILS TYPE F3
SCALE 1:25

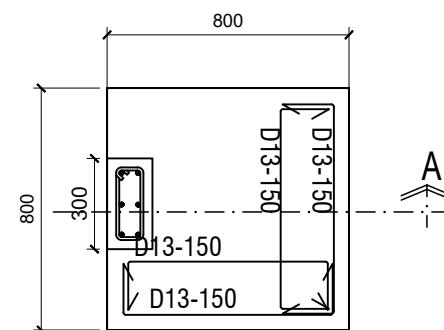

FOUNDATION DETAILS TYPE F4
SCALE 1:25

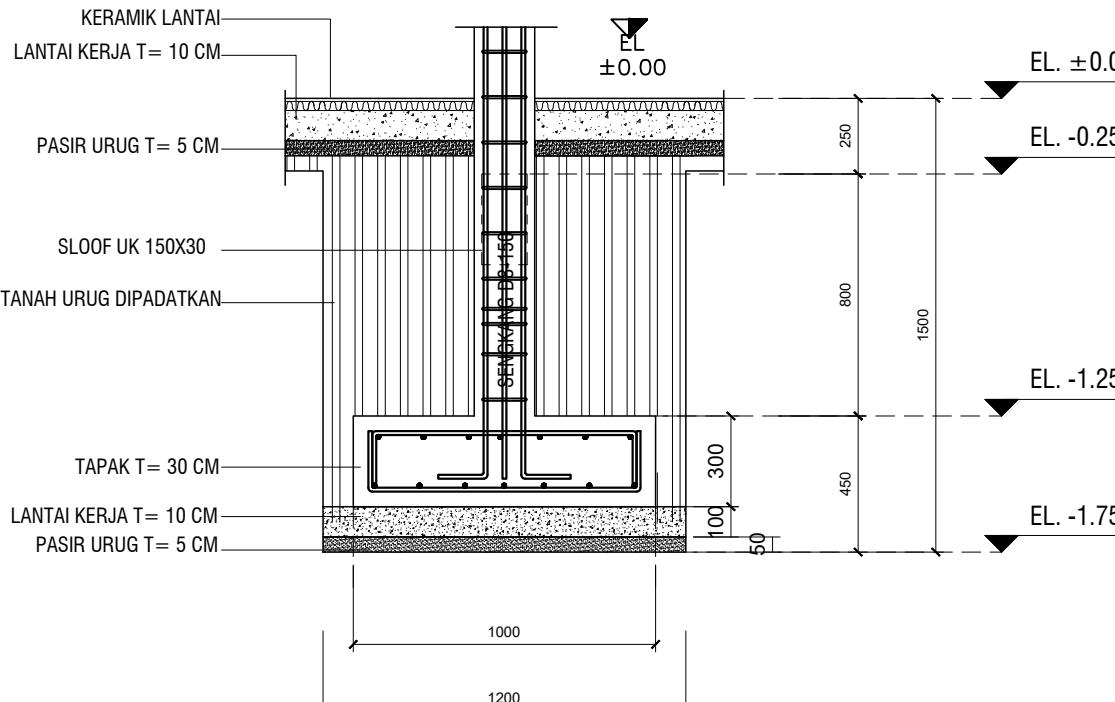

SECTION A
SCALE 1:25

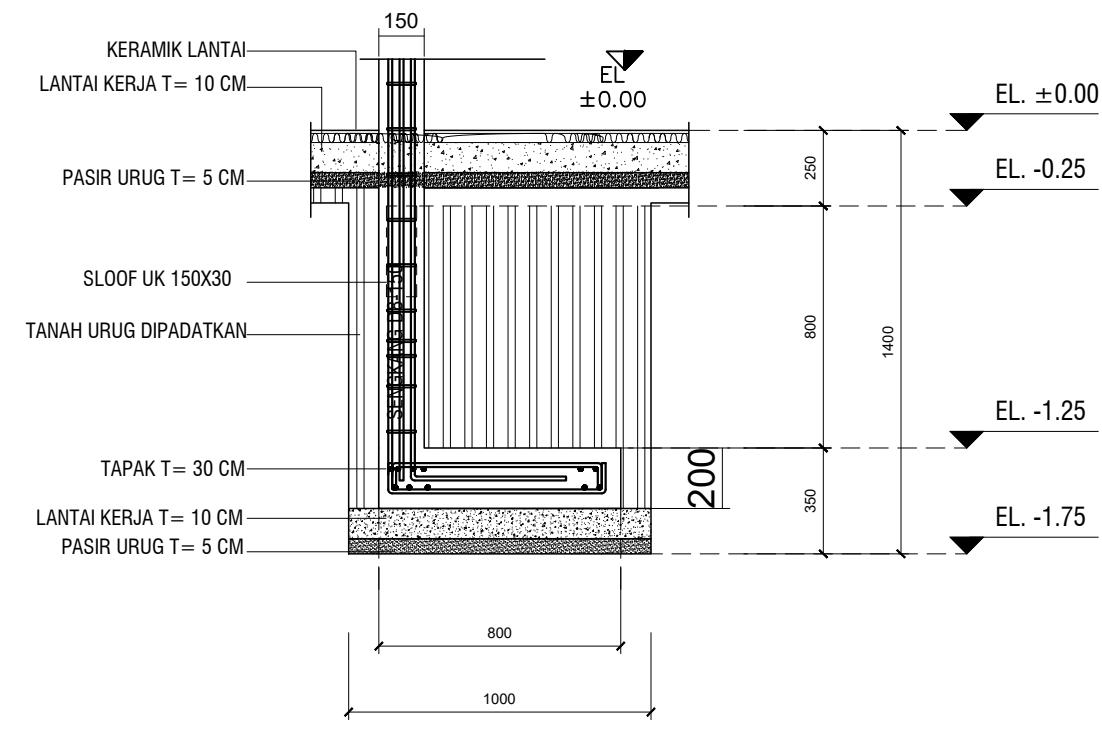

SECTION A
SCALE 1:25

FOUNDATION DETAILS TYPE F3
FOUNDATION DETAILS TYPE F4

SKALA :	DIGAMBAR	TGL.	
1:25	DIPERIKSA	TGL.	
DISETUJUI		TGL.	
DIKELUARKAN UNTUK :	FOR DESIGN DEVELOPMENT		
NO. PROYEK	NO. GAMBAR :	KODE GAMBAR :	REVISI :
	71	STR-04	