



Sesuai dengan rancangan dan karya seni yang tertera pada gambar ini diindungi oleh Undang-undang Hak Cipta, serta hanya dapat untuk yang telah ditentukan dan tidak boleh diperbaiki, dilanjutkan, atau dimodifikasi tanpa memerlukan izin tertulis dari pemilik hak cipta. Kegiatan berikut dianggap sebagai pelanggaran terhadap keadaan lapangan dan apabila ada ketidaksesuaian harus dilaporkan kepada Arsitek. Garansi berdimensi tidak diperkenankan diskota. Sebelum pekerjaan dilaksanakan, kontraktor berkewajiban untuk meminta persetujuan gambar kerja dan contoh bahan dari Arsitek.

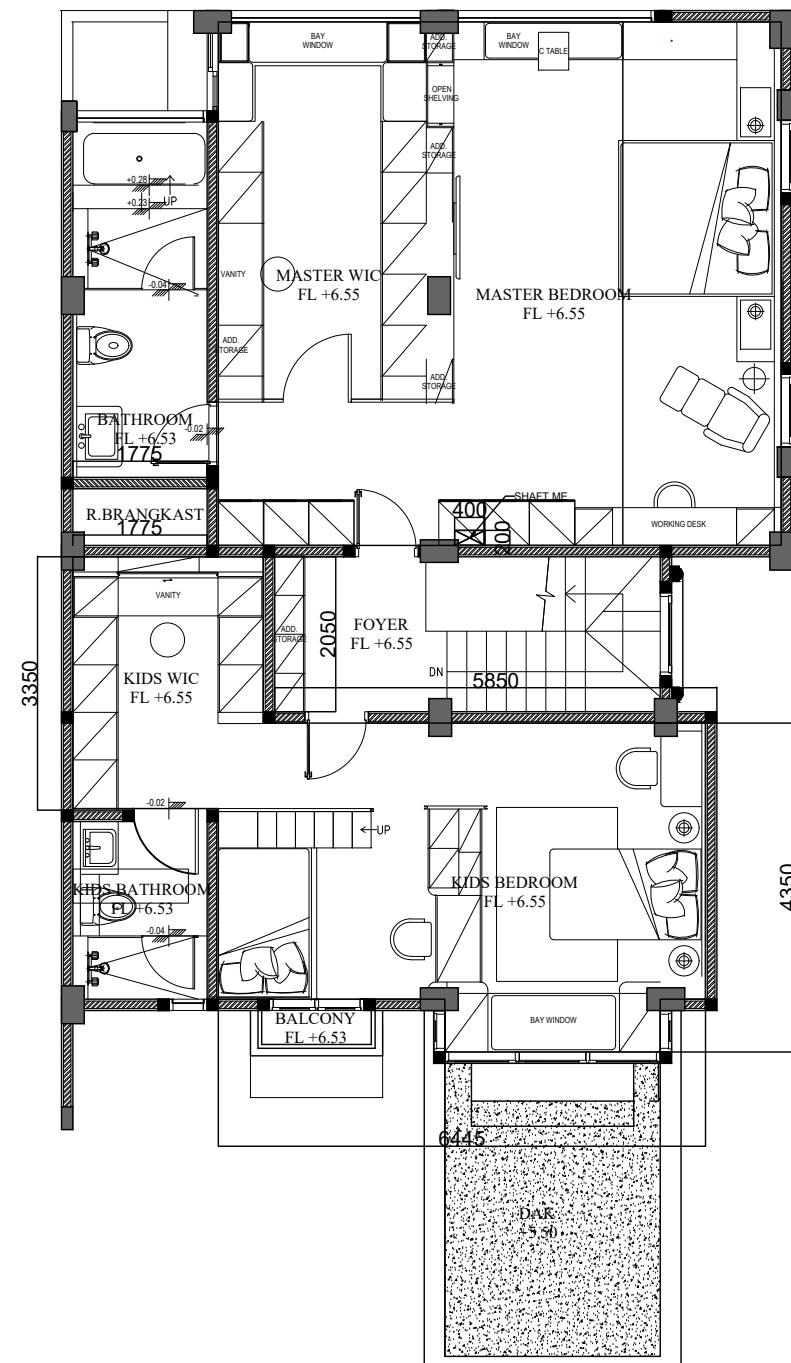

KIDS BEDROOM, KIDS WIC	33.23 M2
MASTER BEDROOM. MASTER WIC	51.55 M2

01 2ND FLOOR PLAN
1 : 100

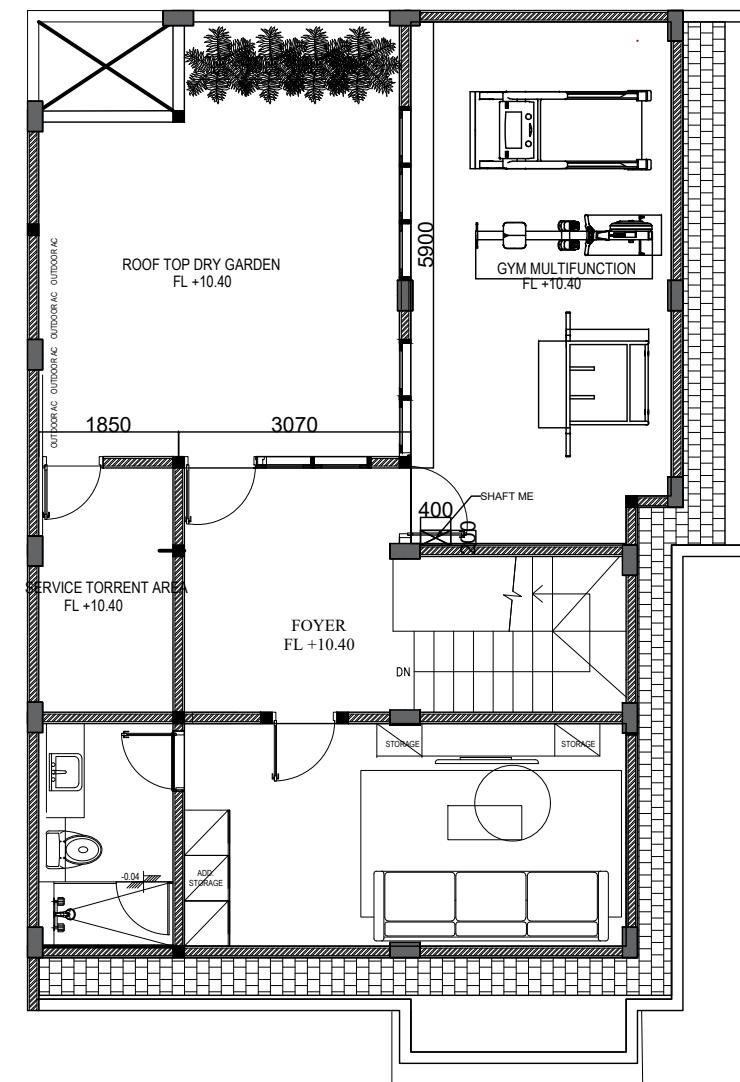

STUDIO	17.21 M2
MASTER BEDROOM. MASTER WIC	23.38 M2

01 3RD FLOOR PLAN
1 : 100

2nd AC PLAN
3rd AC PLAN

SKALA : 1:100	DIGAMBAR		TGL.	
	DIPERIKSA		TGL.	
	DISETUJUI		TGL.	
DISETUJUI PEMB. TUGAS		TGL.	-	
DIKELUARKAN UNTUK : FOR DESIGN DEVELOPMENT				
NO. PROYEK	NO. GAMBAR :	KODE GAMBAR :	REVISI :	
	67	MEP-14		