


NAMA PROYEK	RESIDENTIAL HOUSE AKASIA 2 / 59		
CATATAN :	<p>Sama dengan rencangan dan lantai seni yang tertulis pada gambar ini dilindungi oleh Undang-undang Hak Cipta, serta hanya diperbolehkan untuk yang telah ditentukan dan tidak boleh diperbaiki tanpa ijin tertulis.</p> <p>Kontrak berlaku setelah memahami dimensi terhadap keadaan lapangan dan apabila ada ketidaksesuaian harus disampaikan kepada Arsitek.</p> <p>Gambar berdimensi tidak diperkenankan diakses.</p> <p>Sebelum pengerjaan dimulai, kontraktor berkewajiban untuk meminta persetujuan gambar kerja dan contoh teknis dari Arsitek.</p>		
PEMBERI TUGAS			
ARSITEK	ERIC HANDAYA, S.T I.A.I		
DRAFTING			
JUDUL GAMBAR :			
GROUND PLATFORM FLOOR PLAN			
SKALA :	DIGAMBAR	TGL.	
1:100	DIPERIKSA	TGL.	
	DISETUJUI	TGL.	
DISETUJUI PEMB. TUGAS		TGL.	-
DIKELUARKAN UNTUK : FOR DESIGN DEVELOPMENT			
NO. PROYEK	NO. GAMBAR :	KODE GAMBAR :	REVISI :
	80	STR-13	

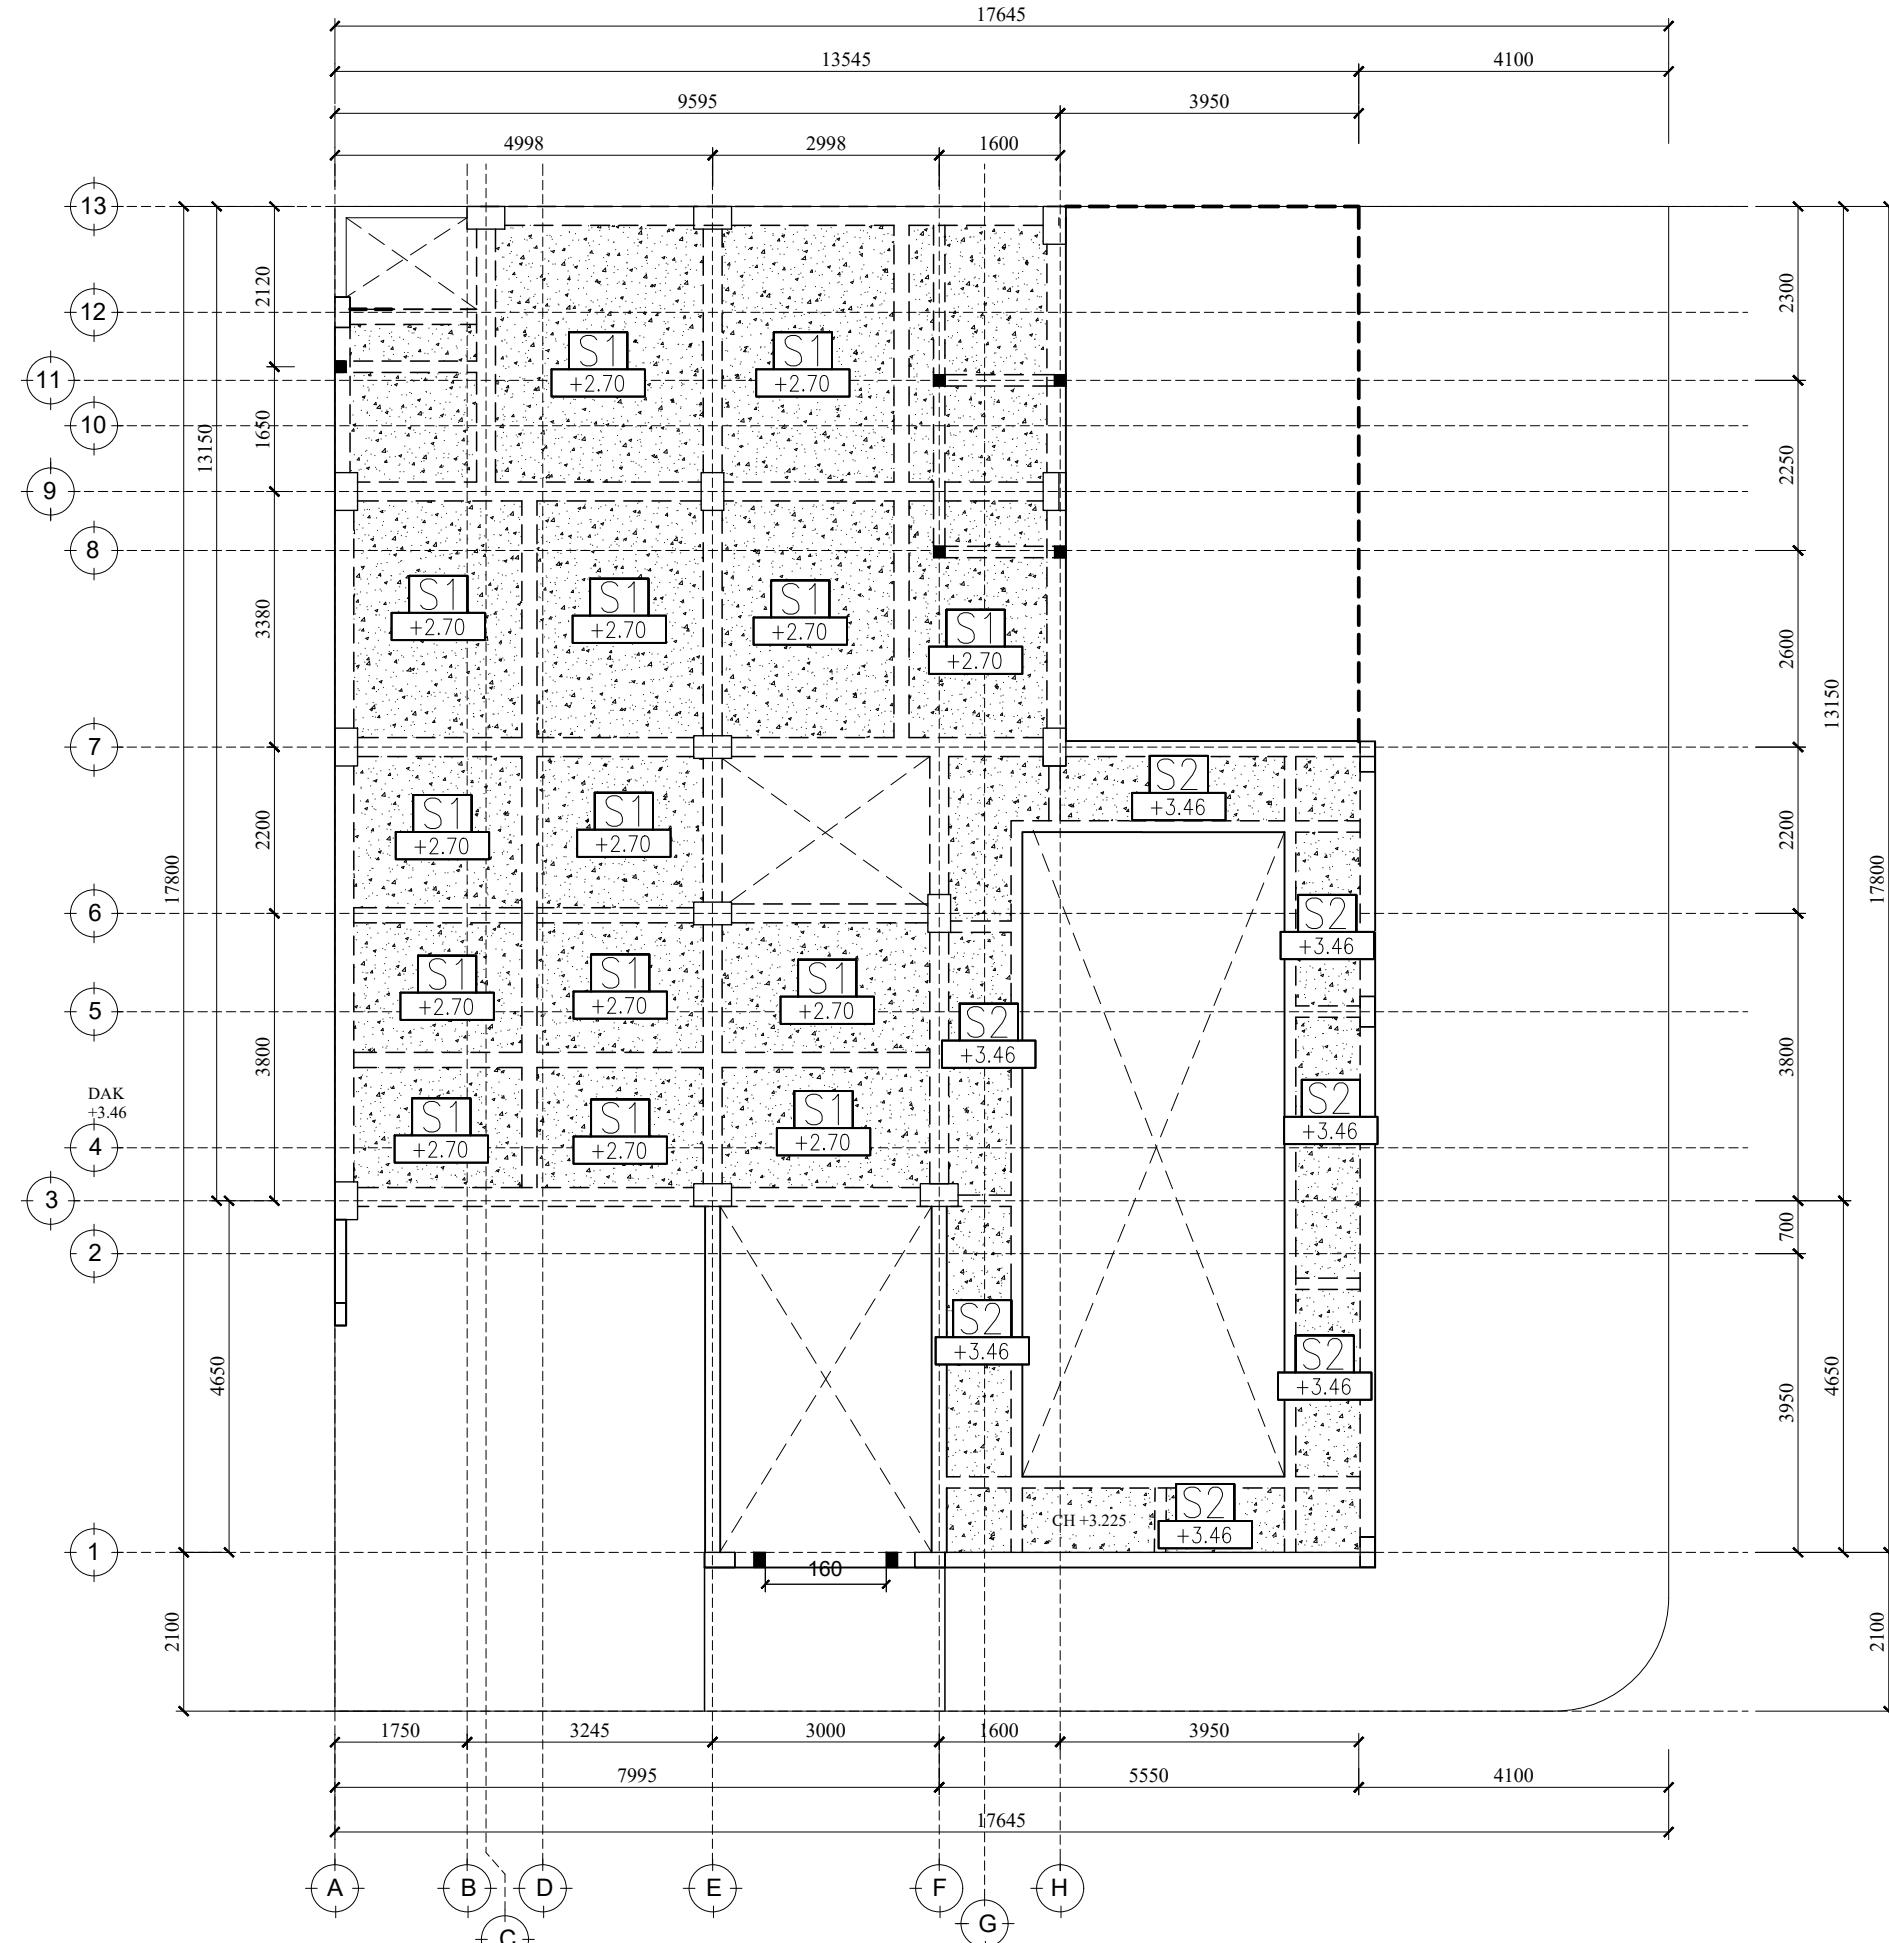

01 GROUND PLATFORM FLOOR PLAN
1:100