




NAMA PROYEK	RESIDENTIAL HOUSE AKASIA 2 / 59		
CATATAN :			
PEMBERI TUGAS			
ARSITEK			
DRAFTING			
REVISI			
TGL			
NO.			
JUDUL GAMBAR :			
SKALA :	DIGAMBAR	TGL.	
	DIPERIKSA	TGL.	
	DISETUJUI	TGL.	
DISETUJUI PEMB. TUGAS	TGL. -		
DIKELUARKAN UNTUK :			
NO. PROYEK	NO. GAMBAR :	KODE GAMBAR :	REVISI :

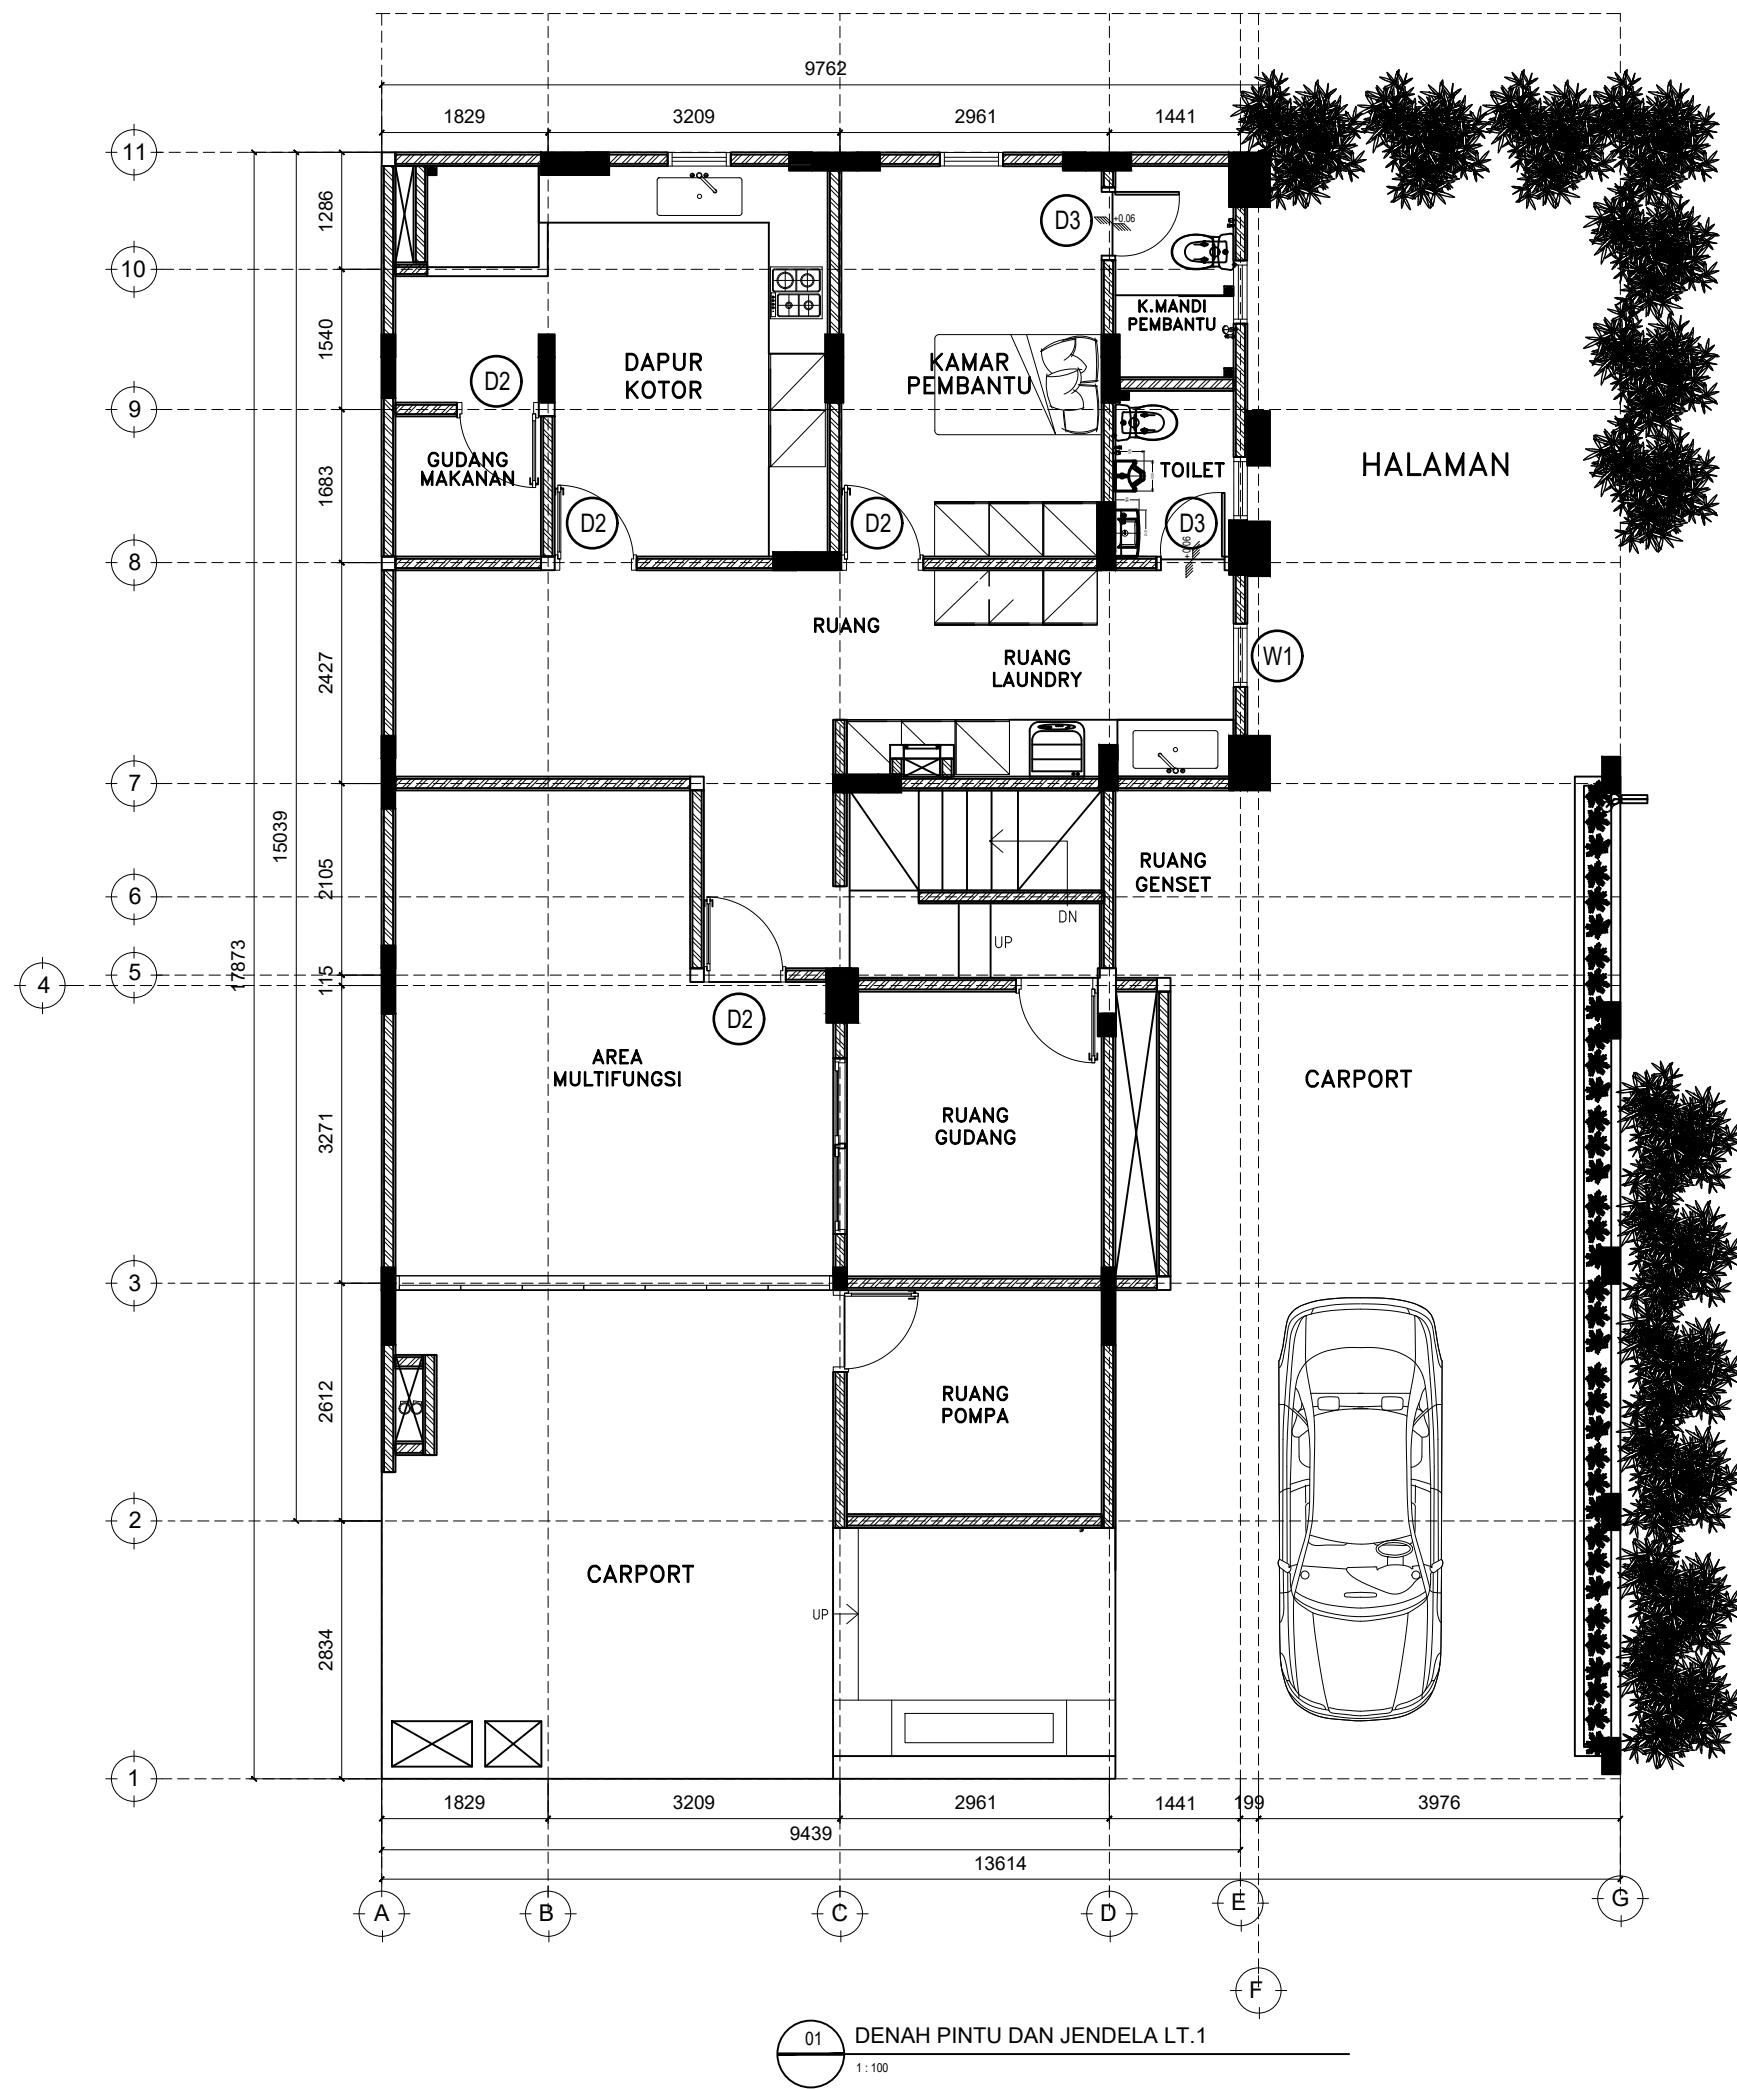

NAMA PROYEK	RESIDENTIAL HOUSE AKASIA 2 / 59		
CATATAN :			
PEMBERI TUGAS			
ARSITEK			
DRAFTING			
REVISI			
TOL			
NO.			
JUDUL GAMBAR :			
SKALA :	DIGAMBAR	TGL.	
	DIPERIKSA	TGL.	
	DISETUJUI	TGL.	
DIKELUARKAN UNTUK :			
NO. PROYEK	NO. GAMBAR :	KODE GAMBAR :	REVISI :

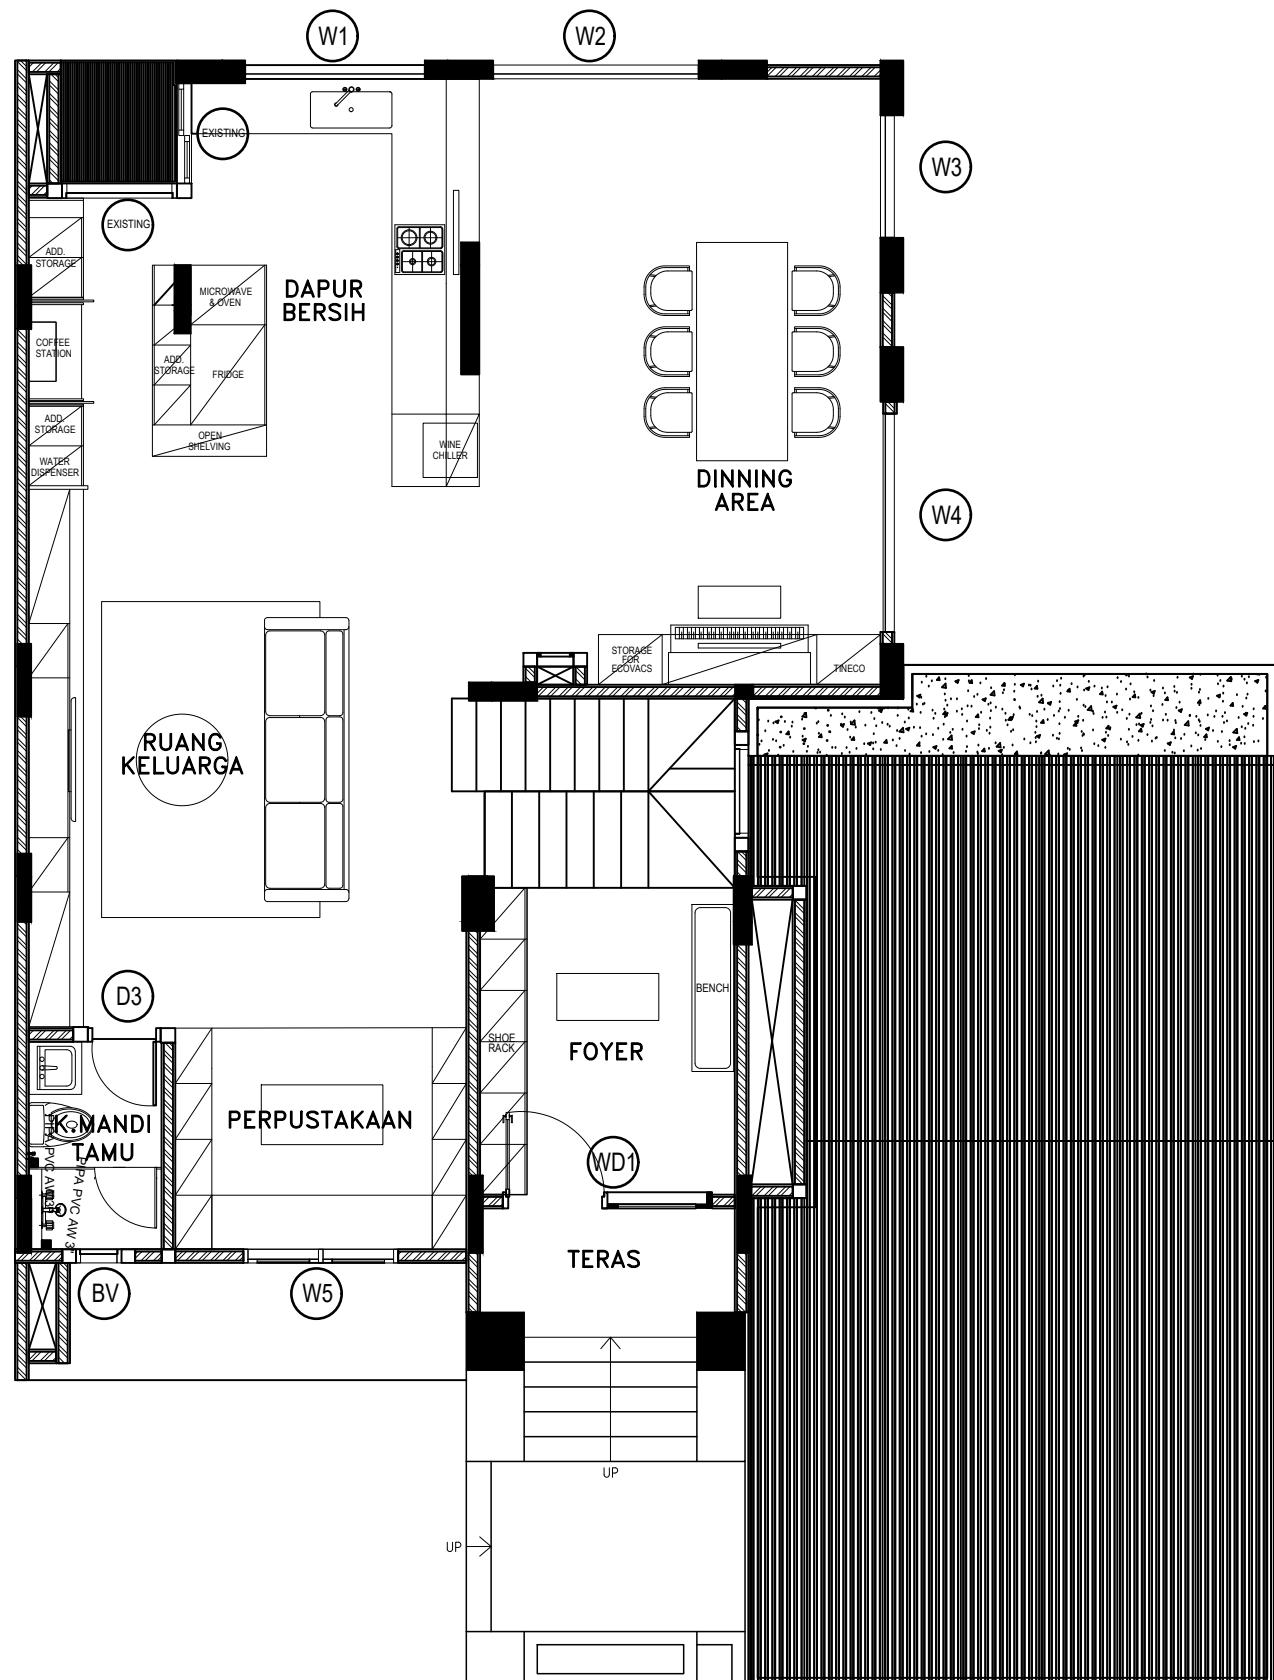

01 DENAH PINTU DAN JENDELA LT.2
1 : 100

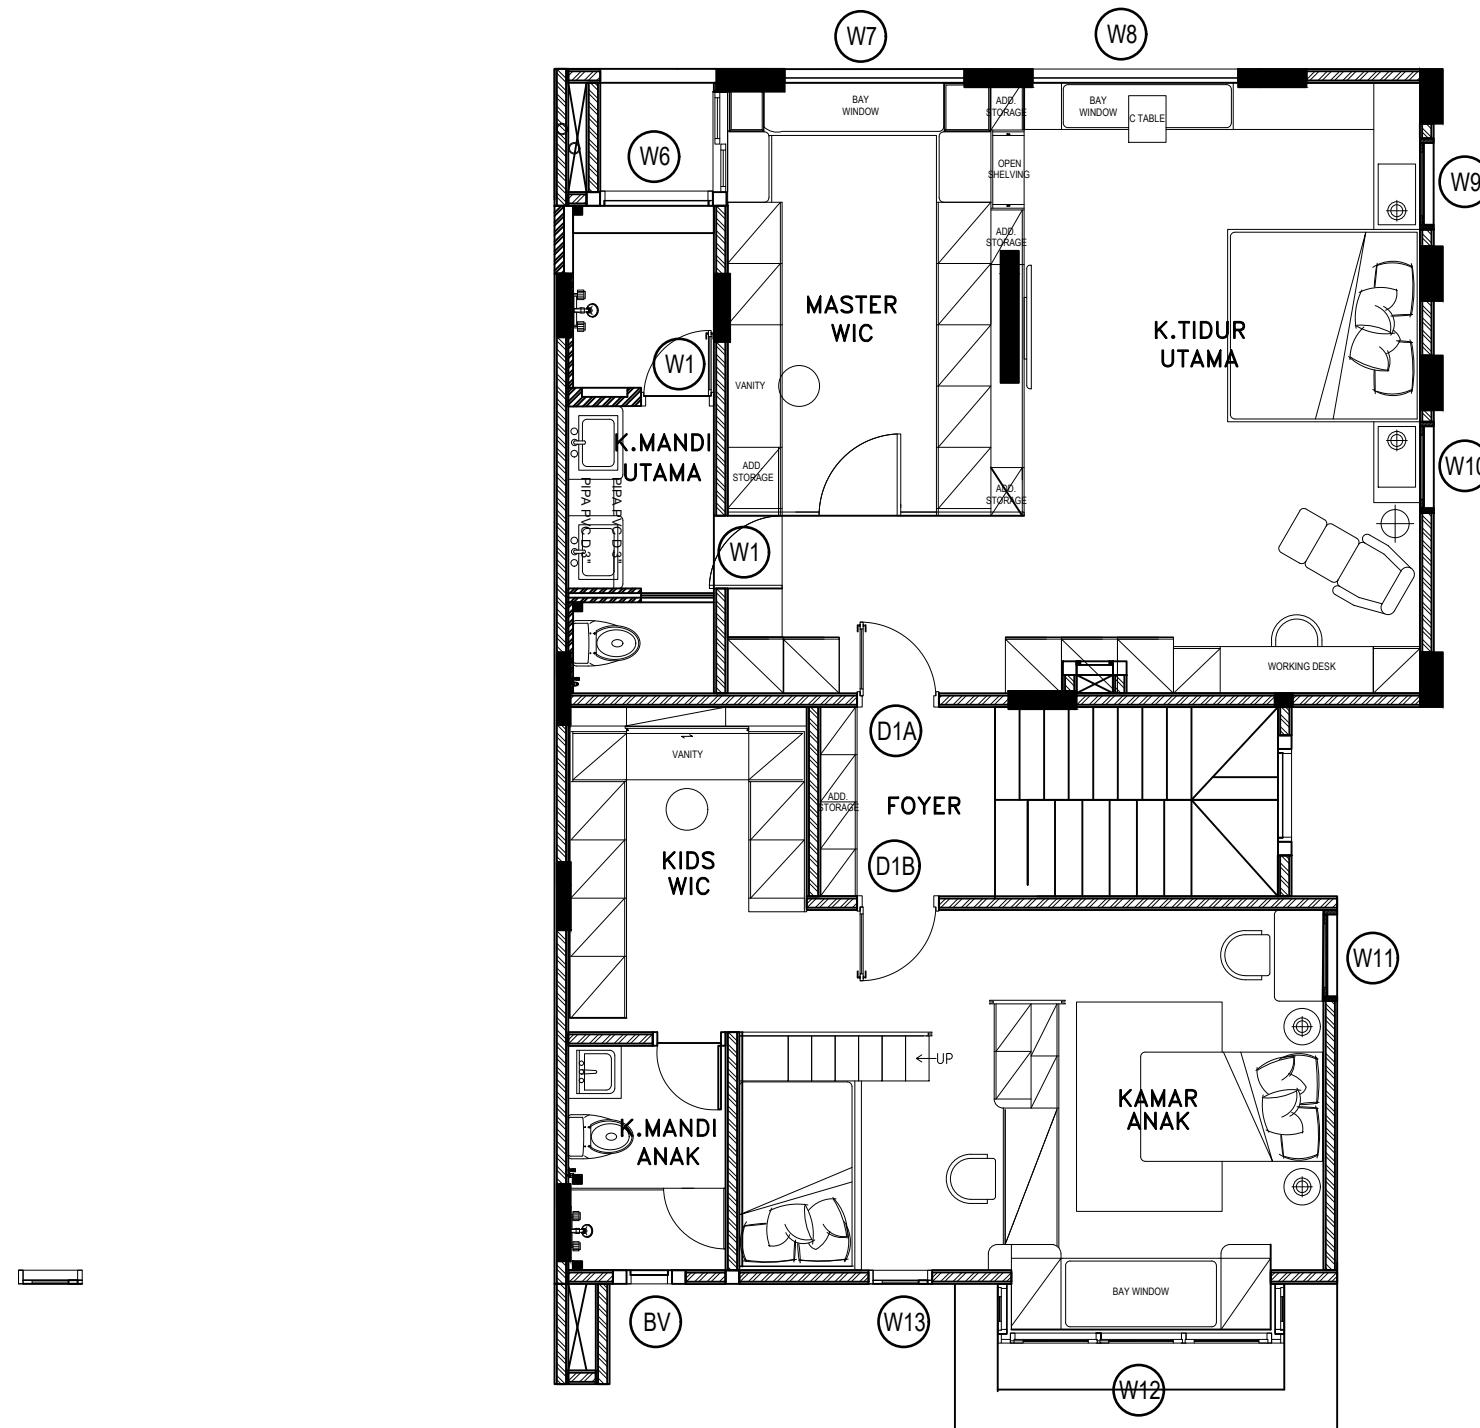

01 DENAH PINTU DAN JENDELA LT.3
1 : 100

CATATAN :

PEMBERI TUGAS

ARSITEK

DRAFTING

REVISI

JUDUL GAMBAR :

SKALA :

DIGAMBAR

TGL.

DIPERIKSA

TGL.

DISETUJUI

TGL.

DISETUJUI PEMB. TUGAS

TGL. -


DIKELUARKAN UNTUK :

NO. PROYEK



NO. GAMBAR :

KODE GAMBAR :



REVISI :

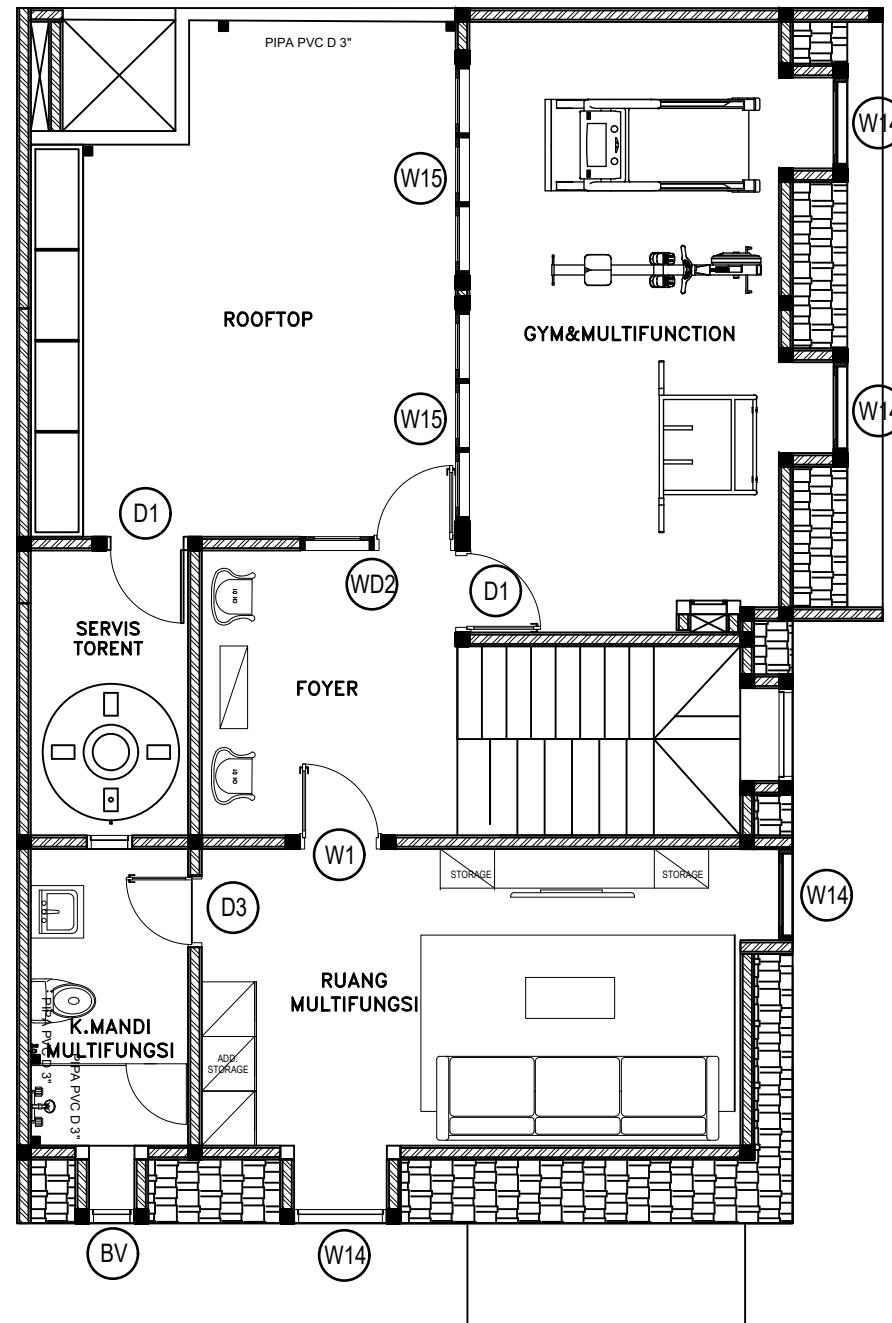



WD1 - 1x

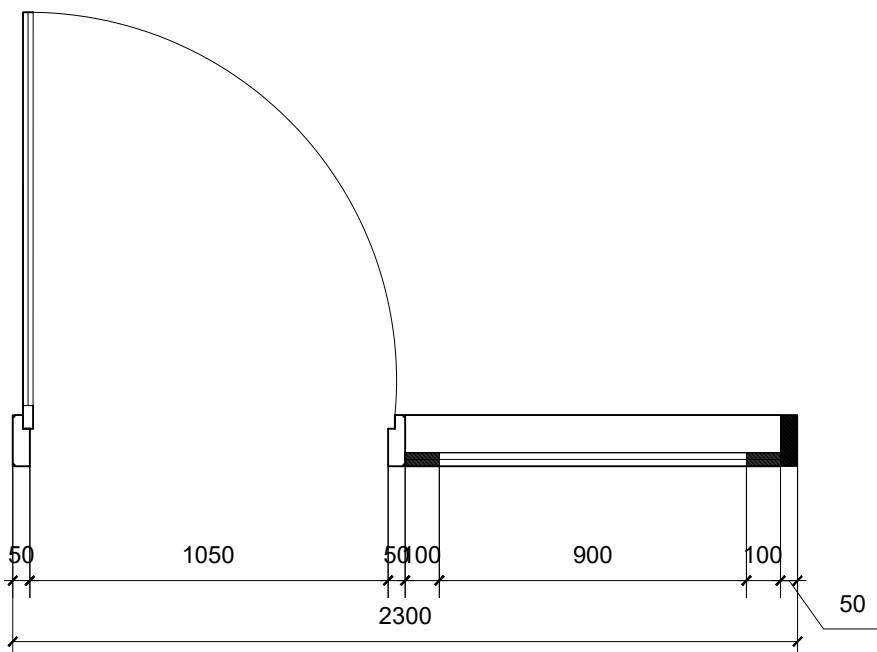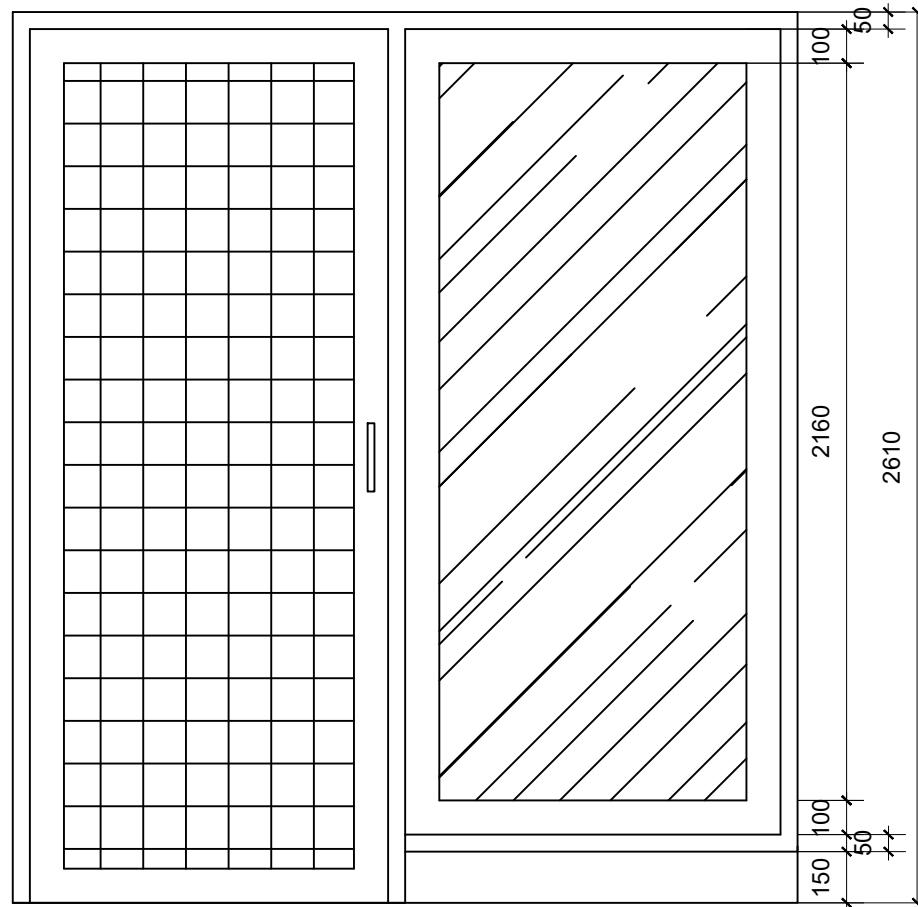

WD2 - 1x

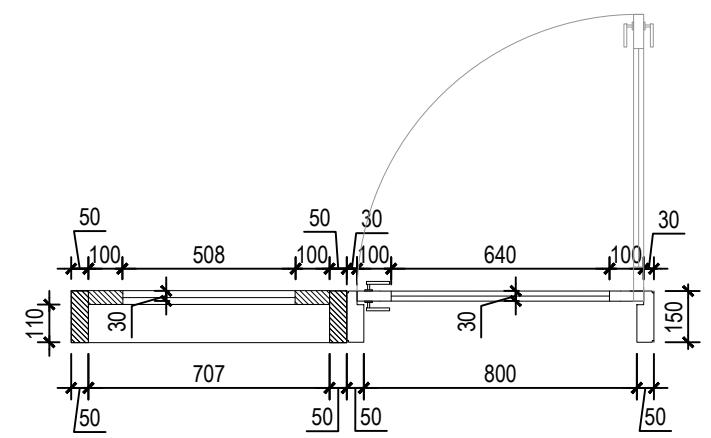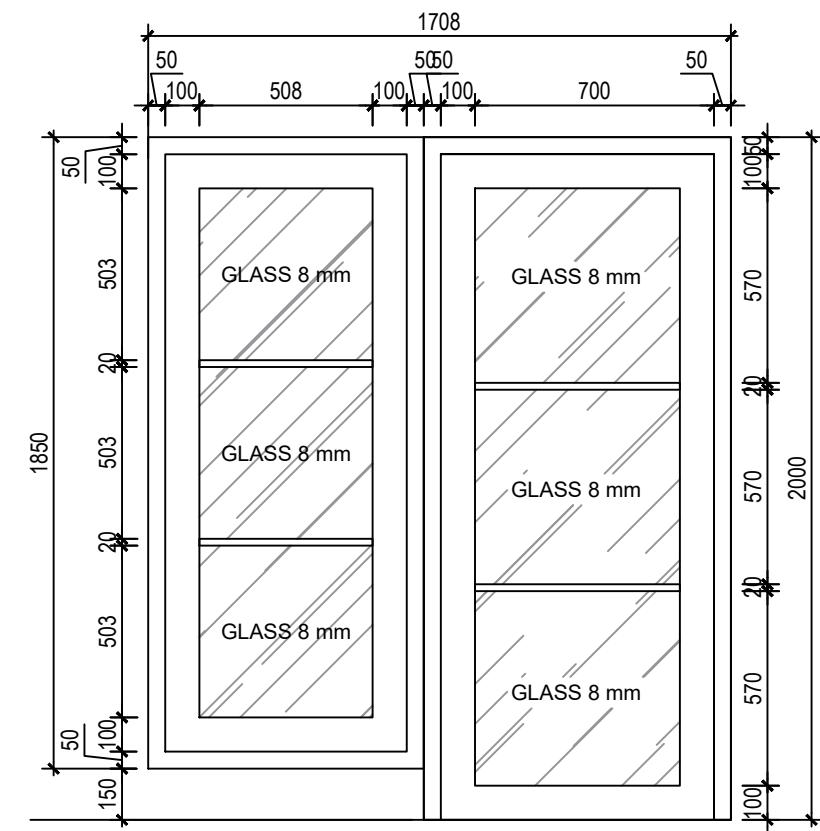

D1A

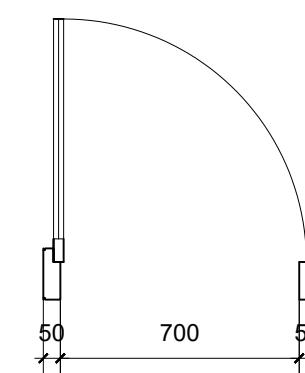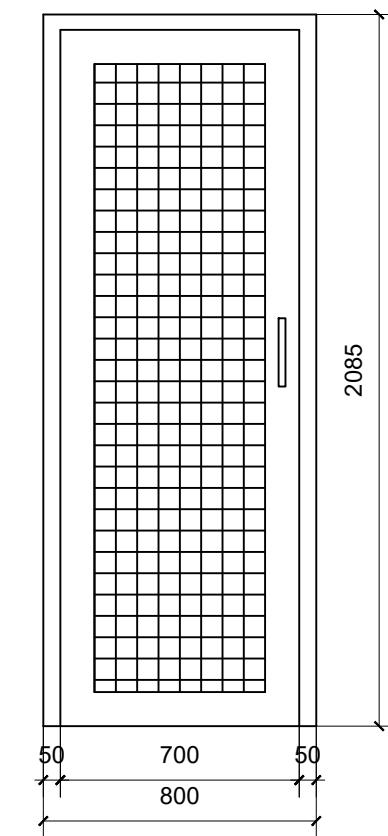NAMA PROYEK
RESIDENTIAL HOUSE AKASIA 2 / 59

CATATAN :

PEMBERI TUGAS

ARSITEK

DRAFTING

REVISI :
TGL :
NO. :
JUDUL GAMBAR :SKALA :
DIGAMBAR : TGL :
DIPERIKSA : TGL :
DISETUJUI : TGL :
DISETUJUI PEMB. TUGAS : TGL :
-

DIKELUARKAN UNTUK :

NO. PROYEK NO. GAMBAR : KODE GAMBAR : REVISI :
-

D1B**D2****D3**NAMA PROYEK
RESIDENTIAL HOUSE AKASIA 2 / 59

CATATAN :

PEMBERI TUGAS

ARSITEK







DRAFTING







REVISI	TGL

JUDUL GAMBAR :

SKALA :	DIGAMBAR	TGL.
	DIPERIKSA	TGL.
	DISETUJUI	TGL.
DIKELUARKAN UNTUK :		TGL. -


NO. PROYEK NO. GAMBAR : KODE GAMBAR : REVISI :

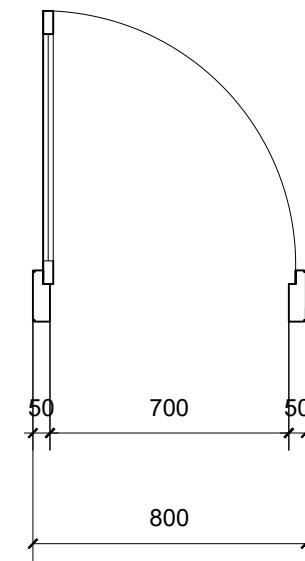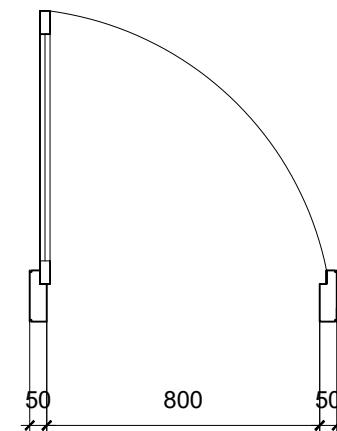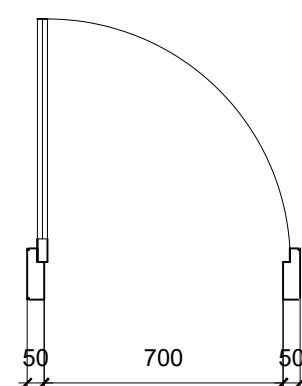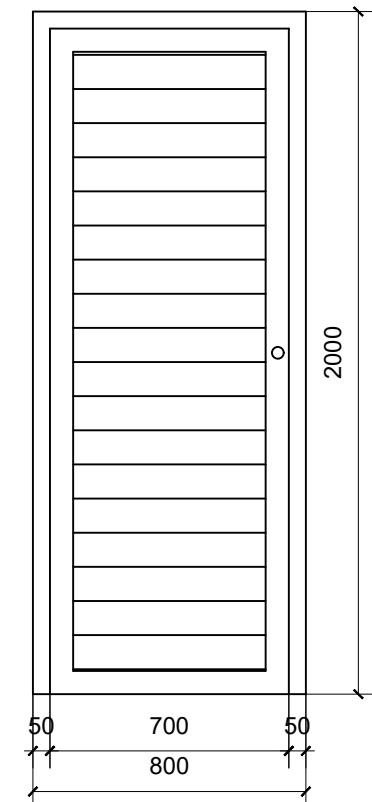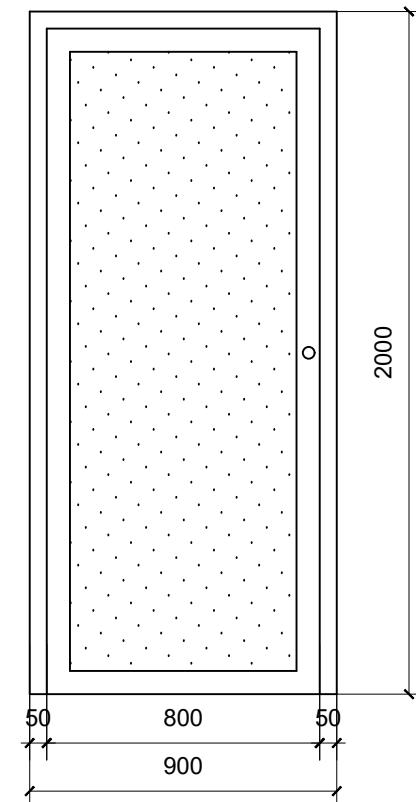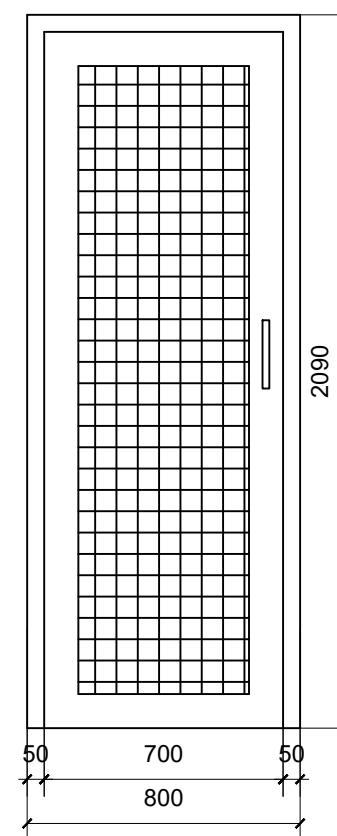

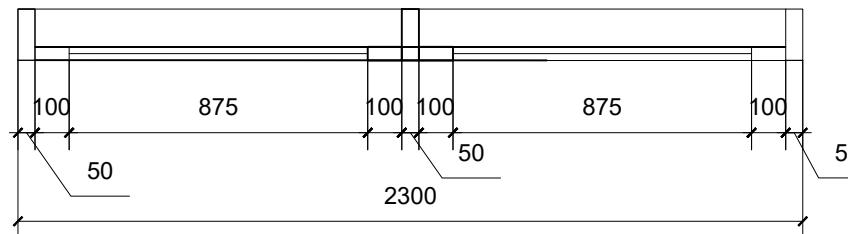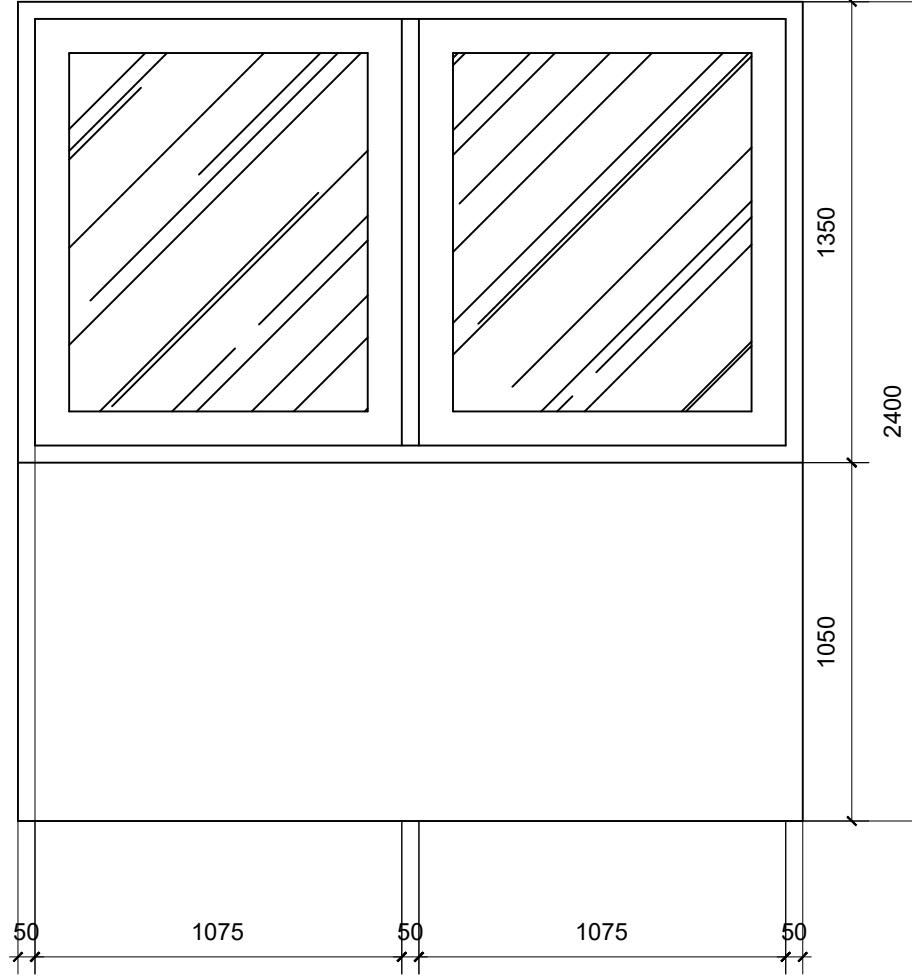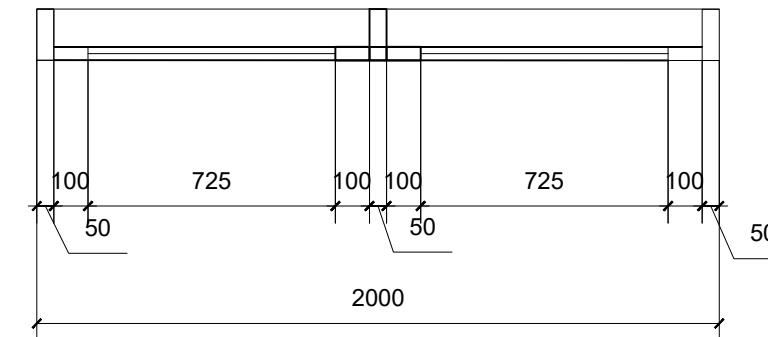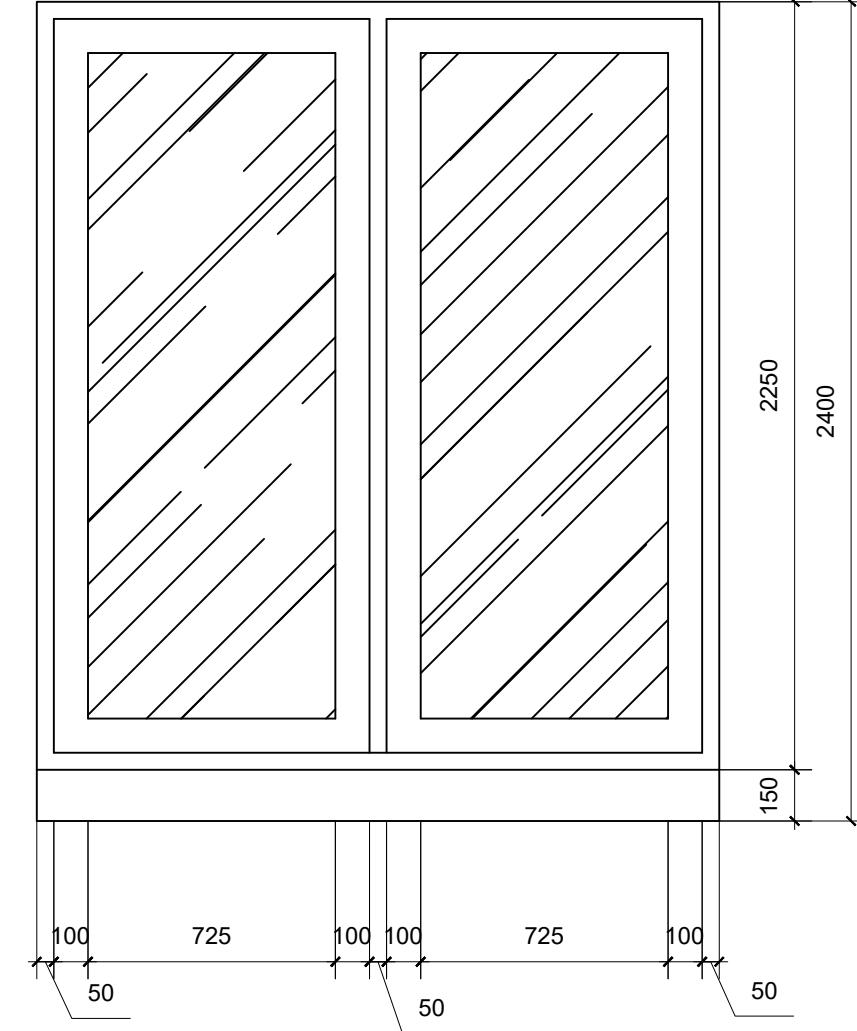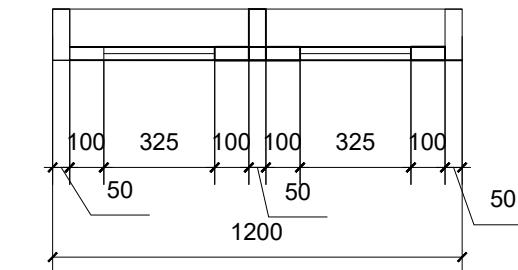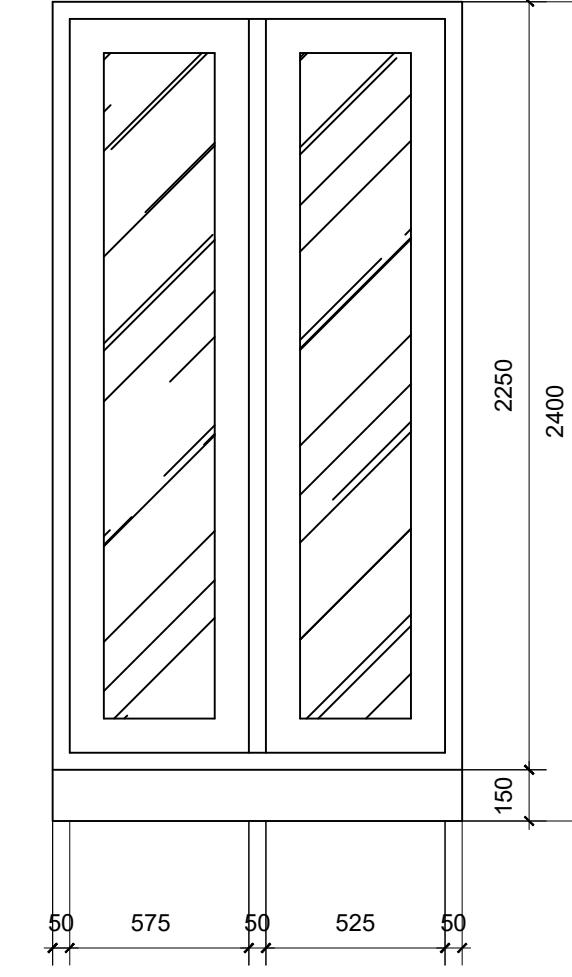
W1**W2****W3**

NAMA PROYEK		RESIDENTIAL HOUSE AKASIA 2 / 59		
CATATAN :				
PEMBERI TUGAS				
ARSITEK				
DRAFTING				
REVISI				
JUDUL GAMBAR :				
NO. TGL				
SKALA :		DIGAMBAR	TGL.	
DIPERIKSA			TGL.	
DISETUJUI			TGL.	
DISETUJUI PEMB. TUGAS		TGL.		-
DIKELUARKAN UNTUK :				
NO. PROYEK	NO. GAMBAR :	KODE GAMBAR :	REVISI :	


W4

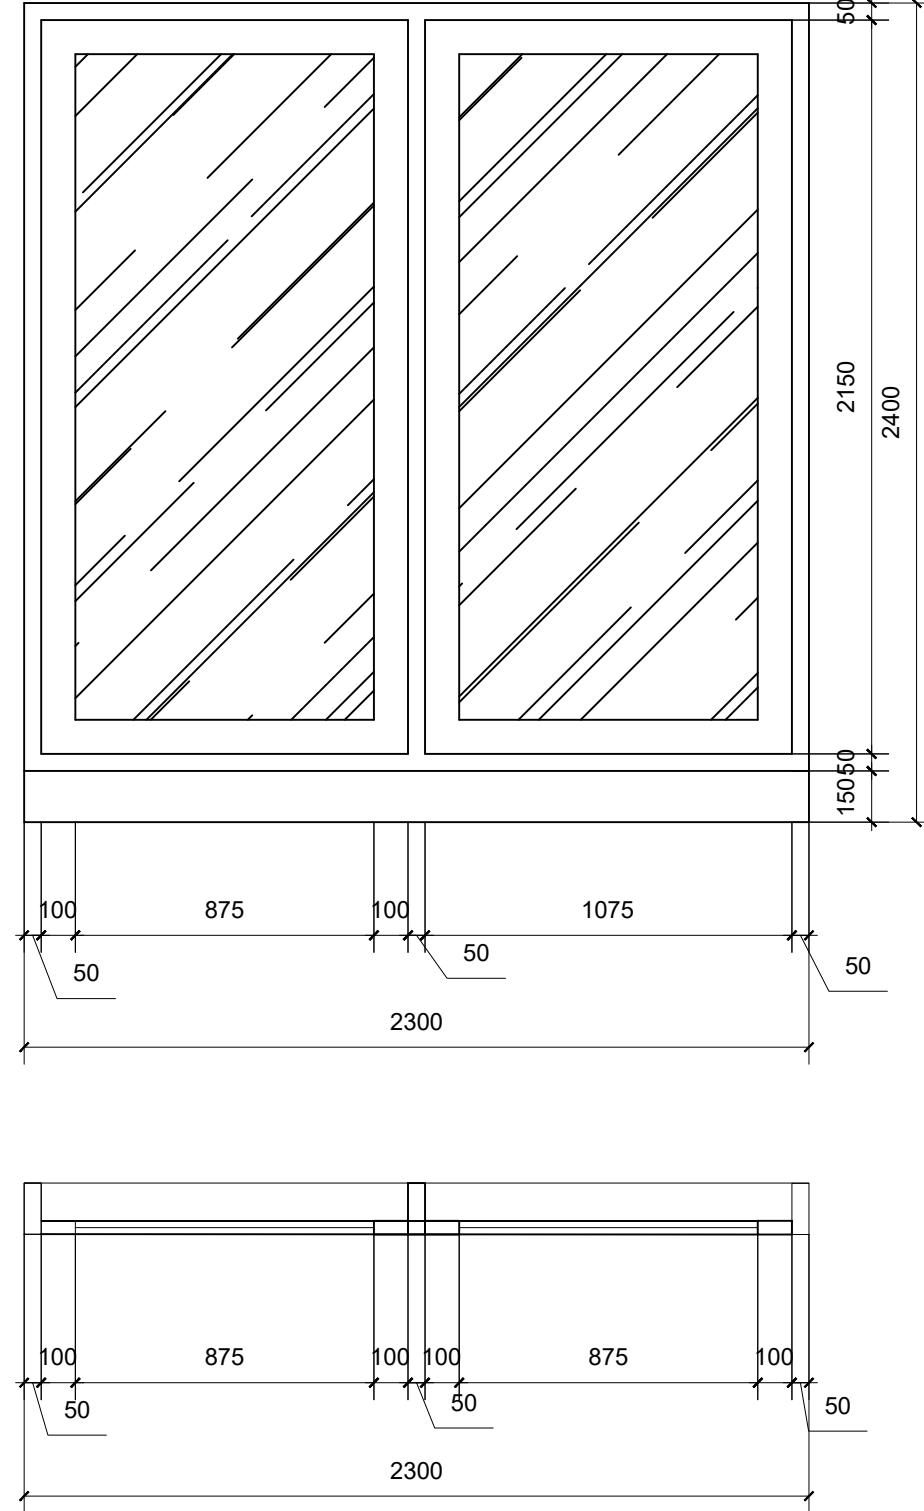

W5

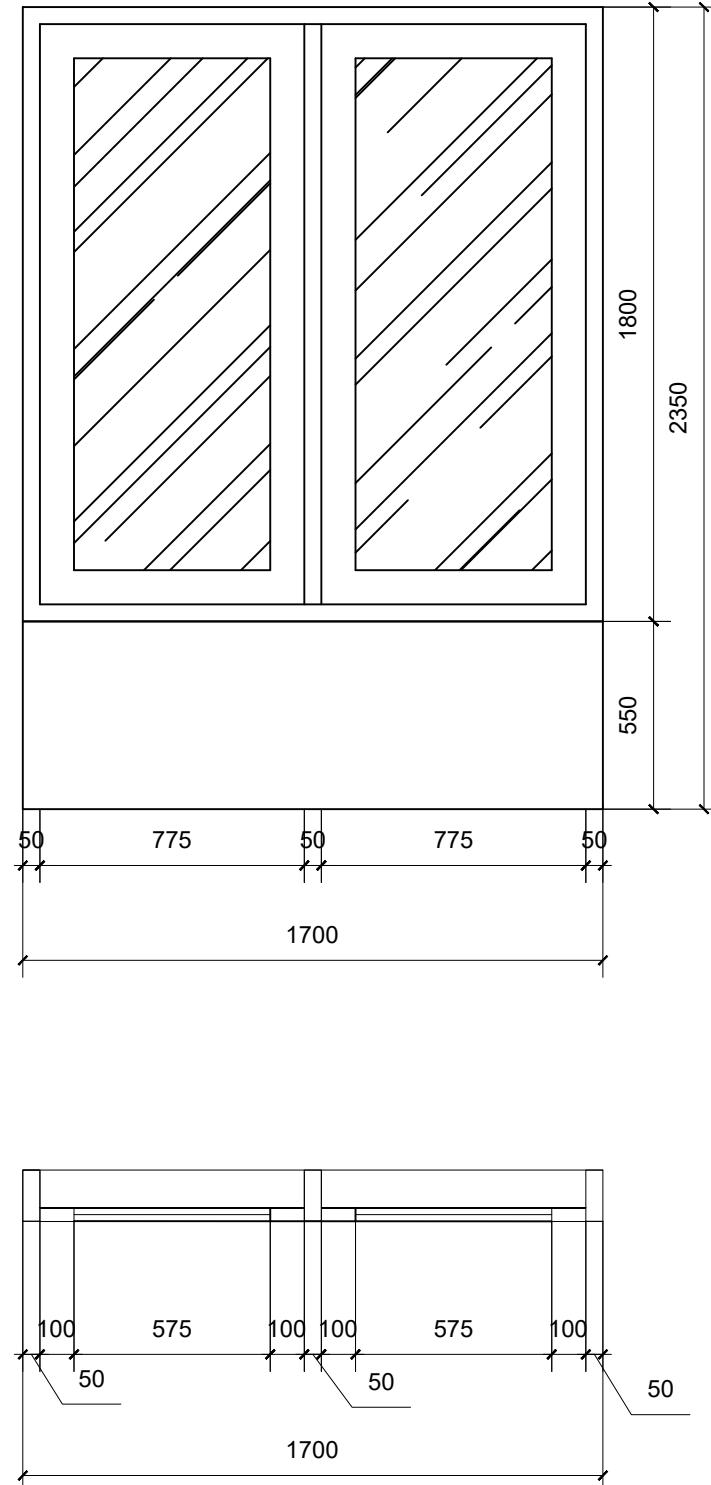

W6






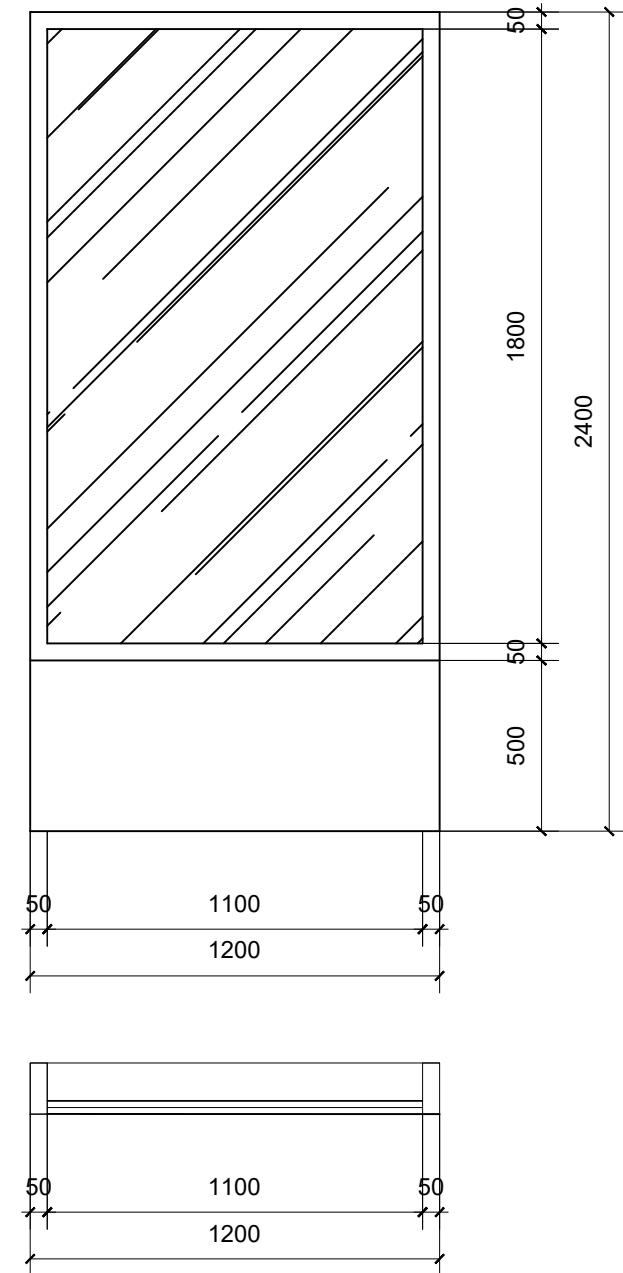


NAMA PROYEK		RESIDENTIAL HOUSE AKASIA 2 / 59		
CATATAN :				
PEMBERI TUGAS				
ARSITEK				
DRAFTING				
REVISI				
JUDUL GAMBAR :				
SKALA :		DIGAMBAR	TGL.	
DIPERIKSA			TGL.	
DISETUJUI			TGL.	
DISETUJUI PEMB. TUGAS			TGL. -	
DIKELUARKAN UNTUK :				
NO. PROYEK	NO. GAMBAR :	KODE GAMBAR :	REVISI :	

W7



W8

W9

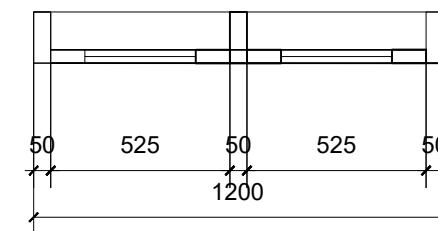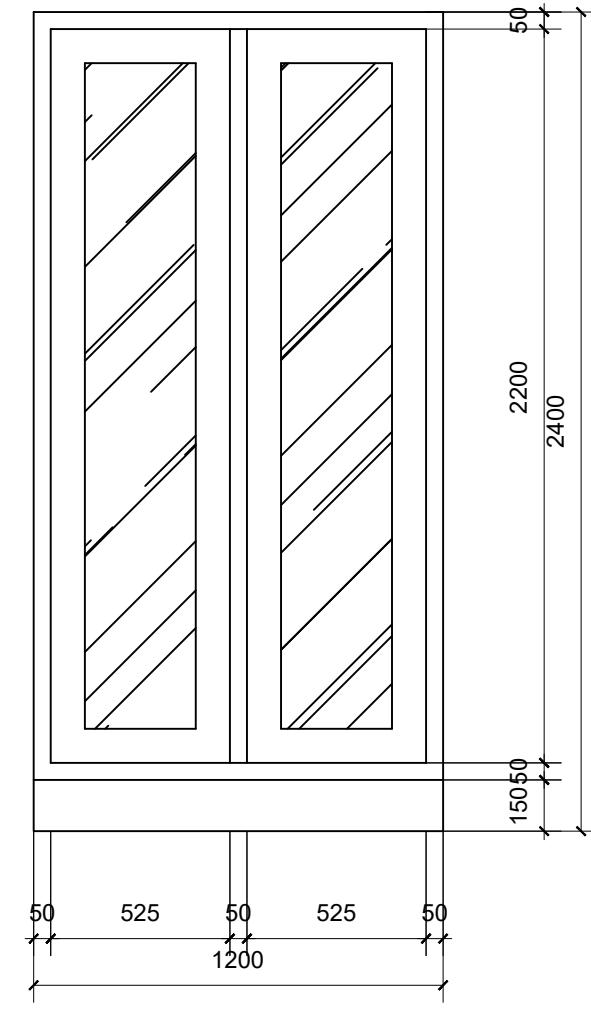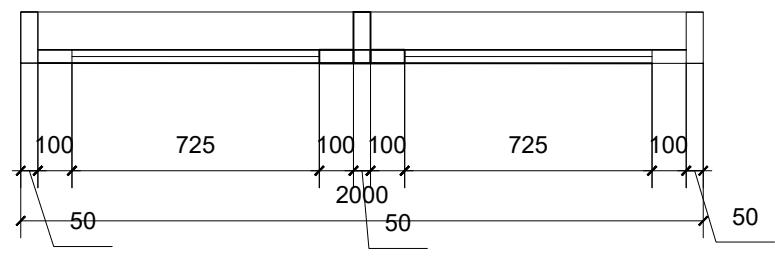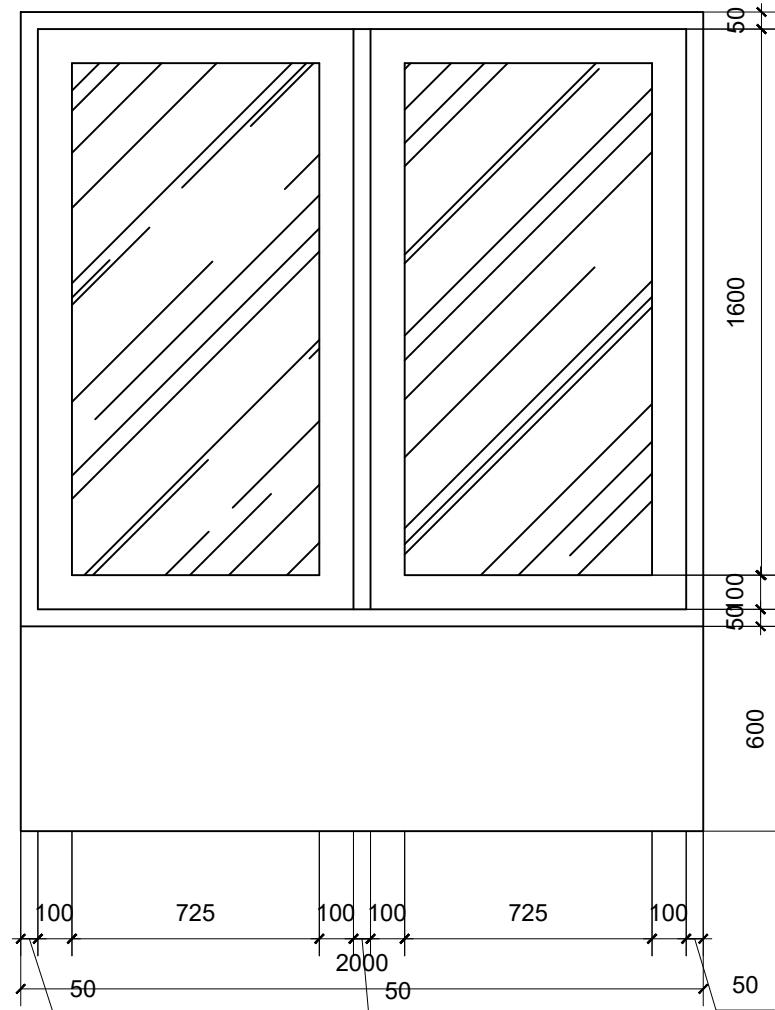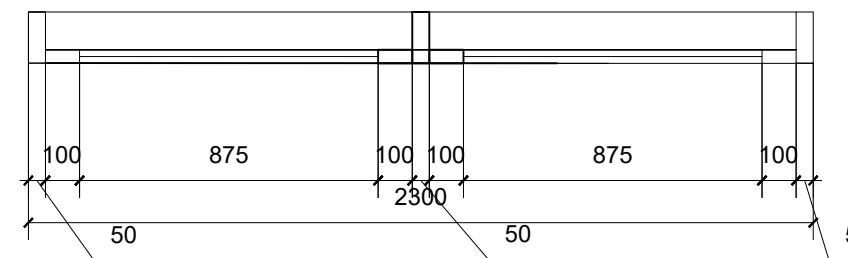
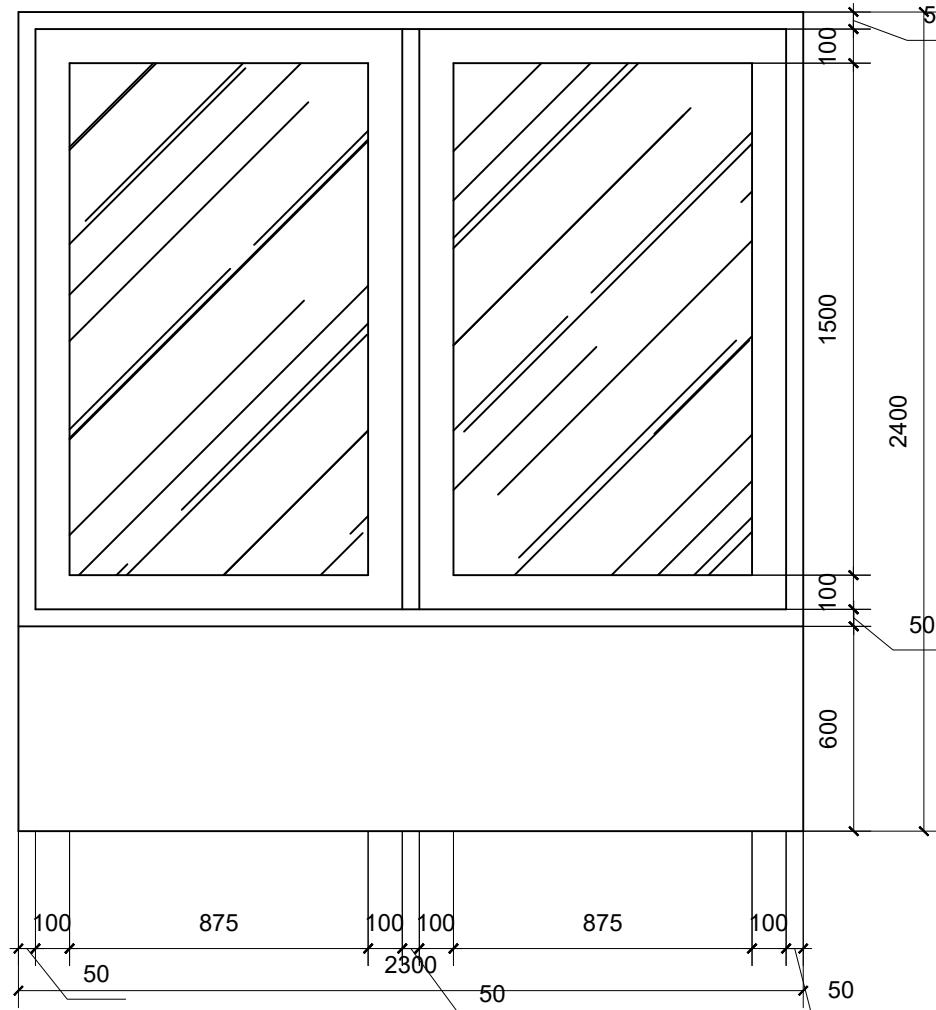


NAMA PROYEK		RESIDENTIAL HOUSE AKASIA 2 / 59	
CATATAN :			
PEMBERI TUGAS			
ARSITEK			
DRAFTING			
REVISI : TGL:			
NO. : TOL:			
JUDUL GAMBAR :			
SKALA :		DIGAMBAR	TGL.
DIPERIKSA			TGL.
DISETUJUI			TGL.
DISETUJUI PEMB. TUGAS		TGL. -	
DIKELUARKAN UNTUK :			
NO. PROYEK	NO. GAMBAR :	KODE GAMBAR :	REVISI :



W10

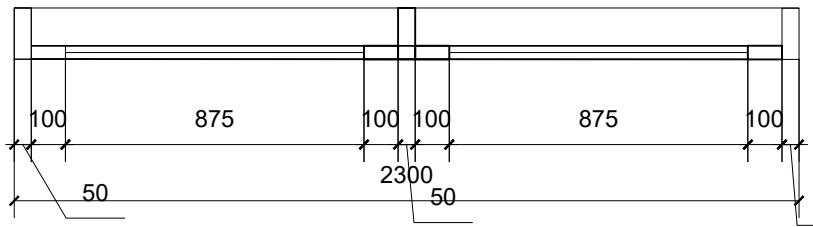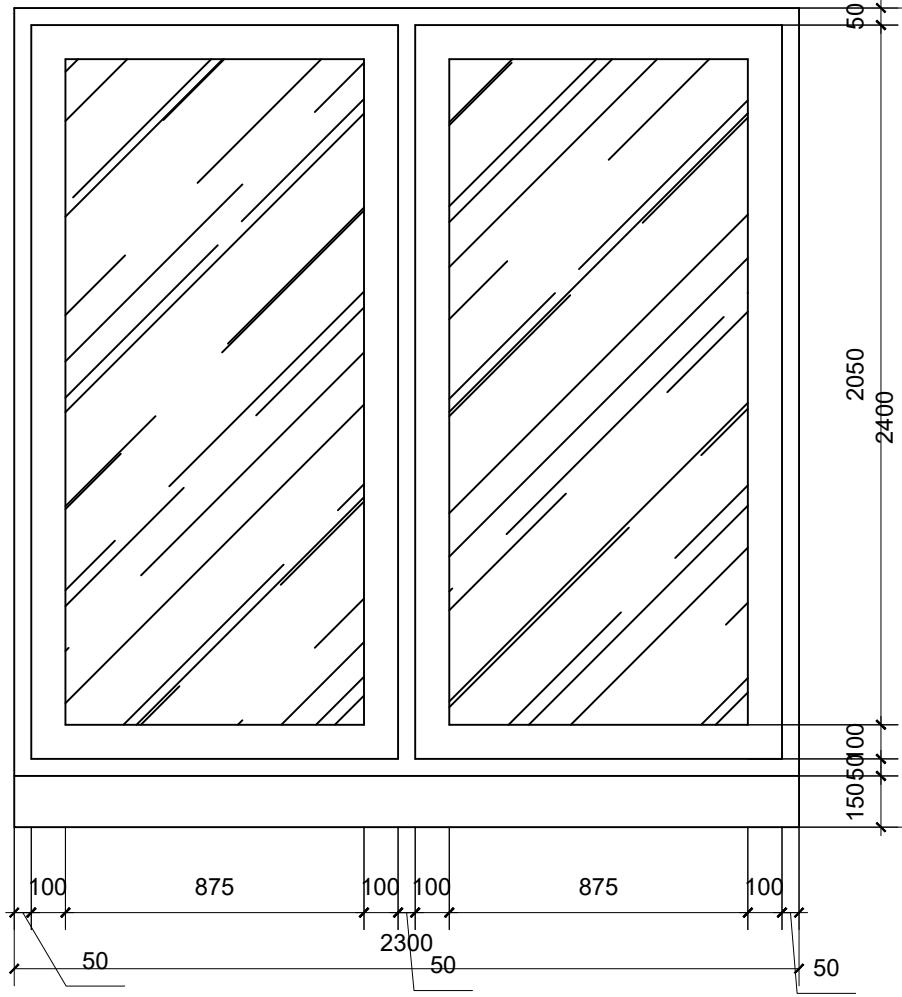

W11

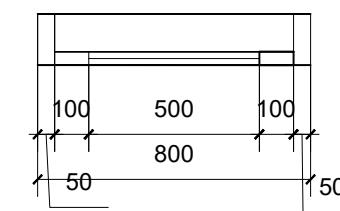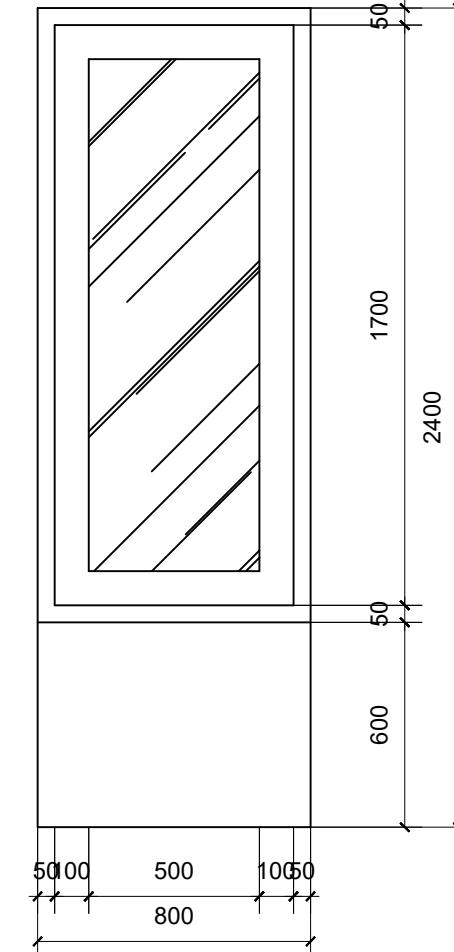


W12


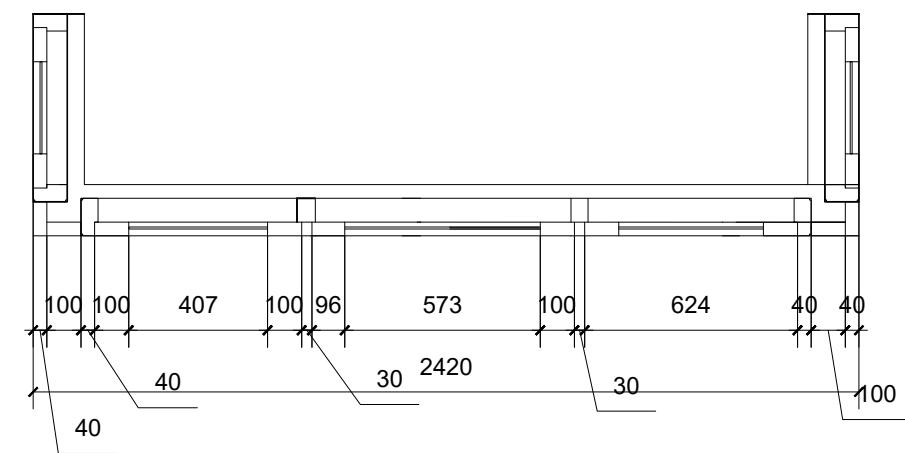
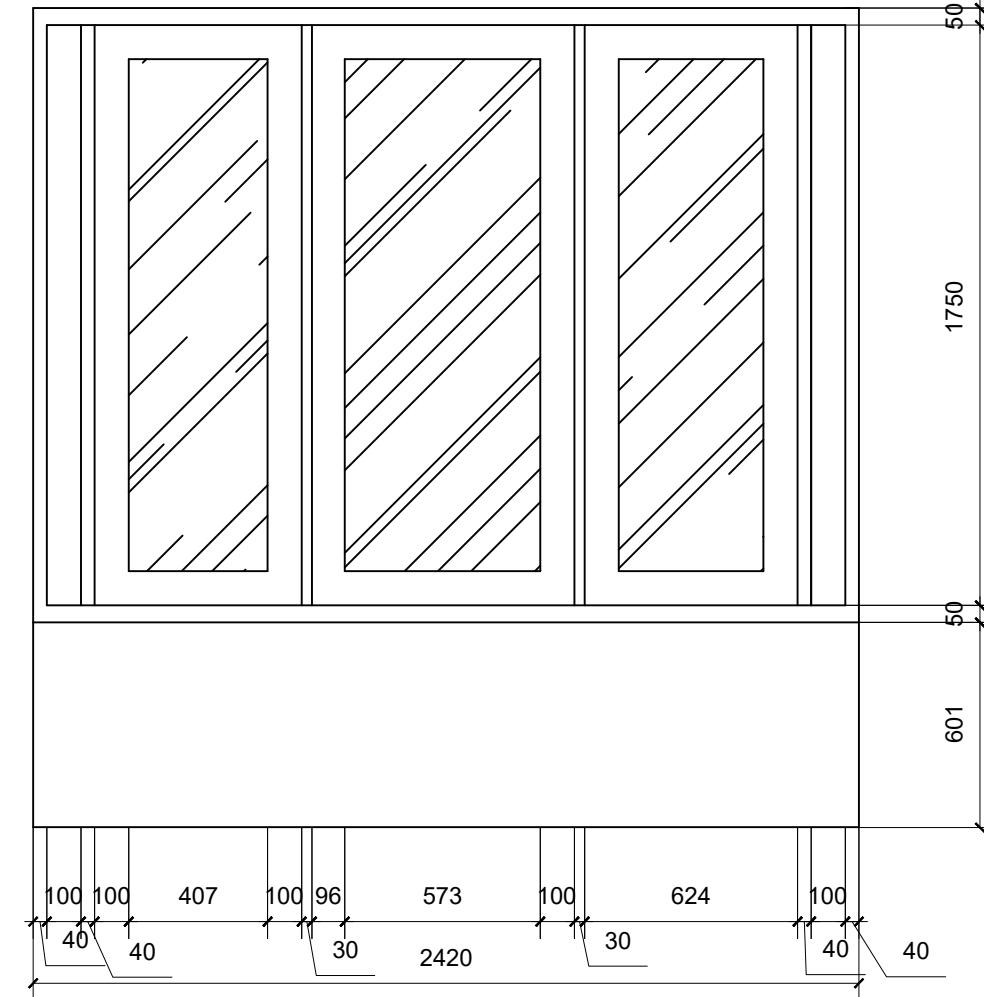


NAMA PROYEK		RESIDENTIAL HOUSE AKASIA 2 / 59	
CATATAN :			
PEMBERI TUGAS			
ARSITEK			
DRAFTING			
REVISI : TGL:			
NO. : TOL:			
JUDUL GAMBAR : NO.:			
SKALA :		DIGAMBAR	TGL.
DIPERIKSA			TGL.
DISETUJUI			TGL.
DISETUJUI PEMB. TUGAS		TGL. -	
DIKELUARKAN UNTUK :			
NO. PROYEK	NO. GAMBAR :	KODE GAMBAR :	REVISI :

W13

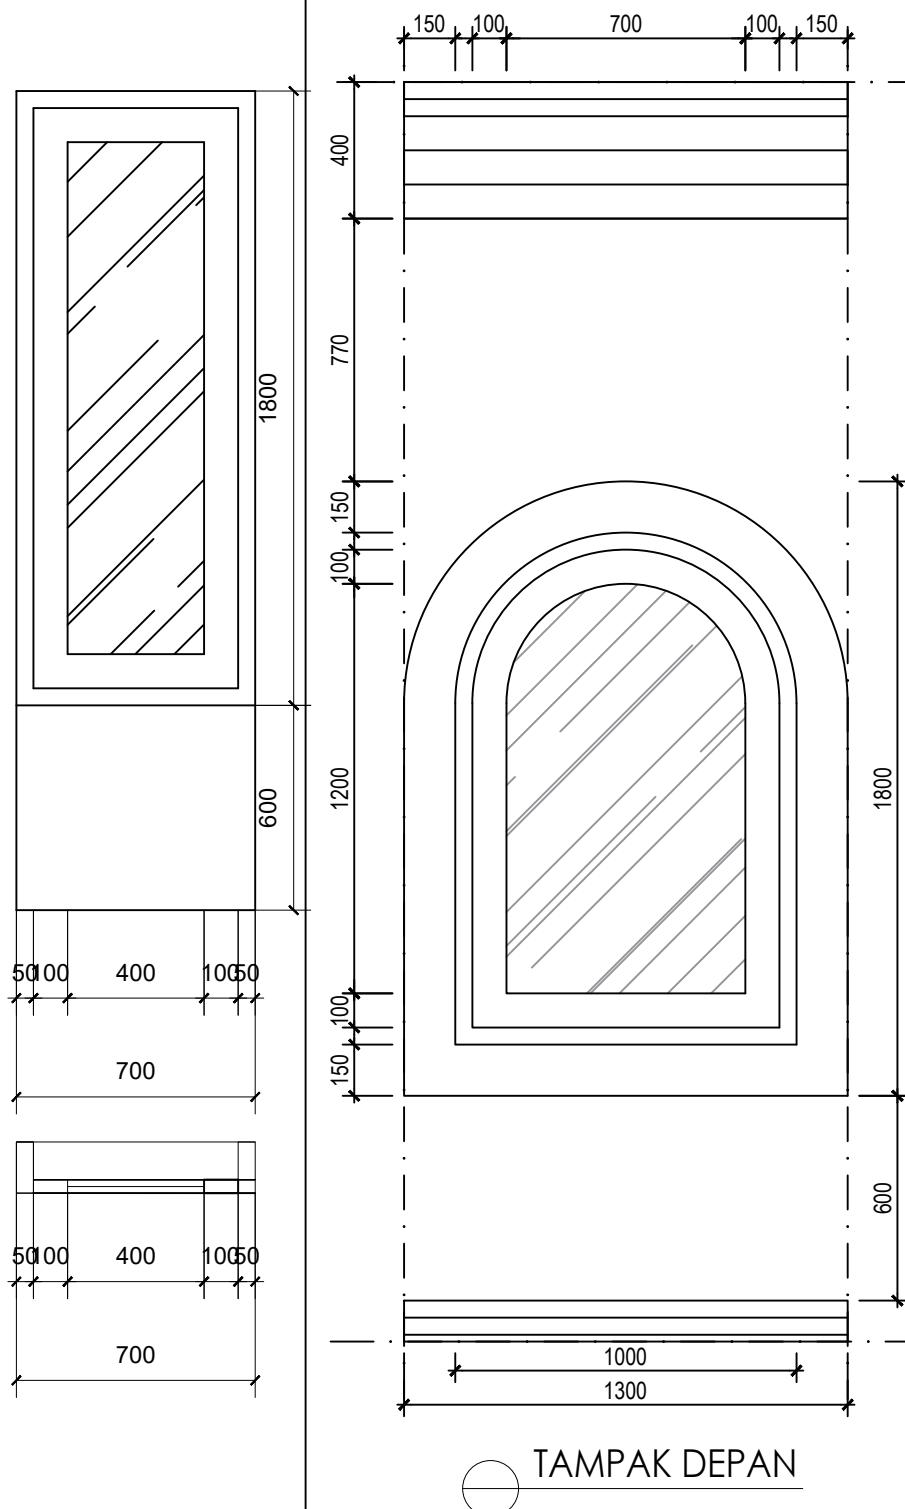



W14

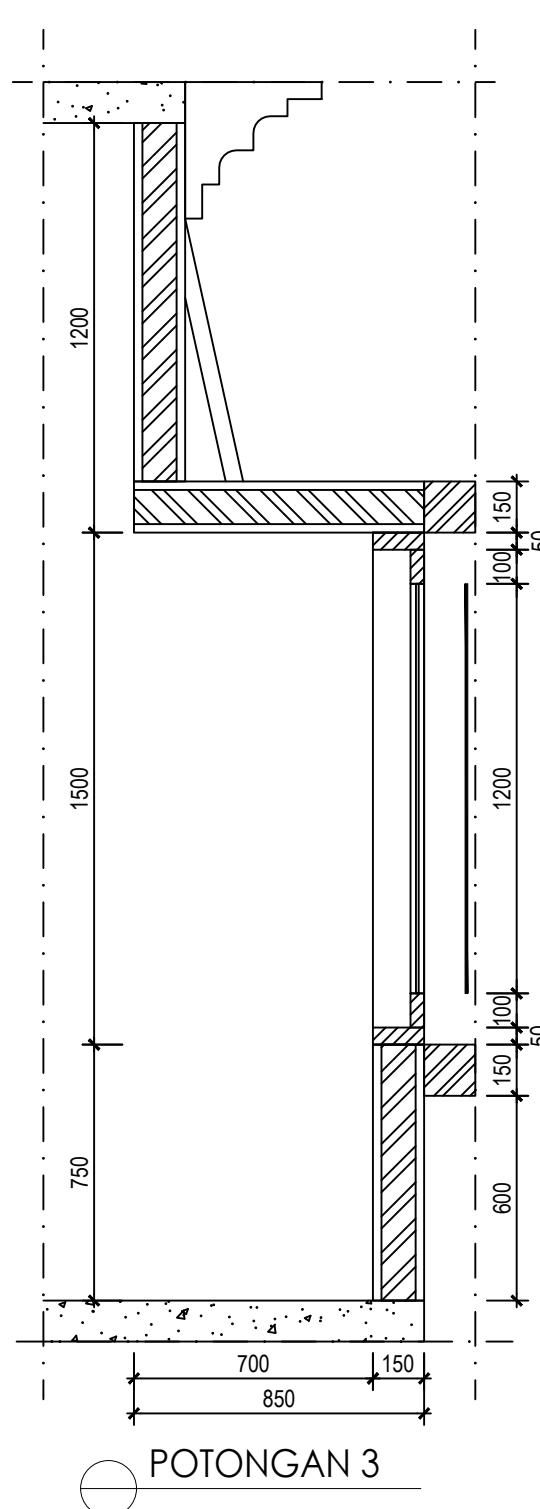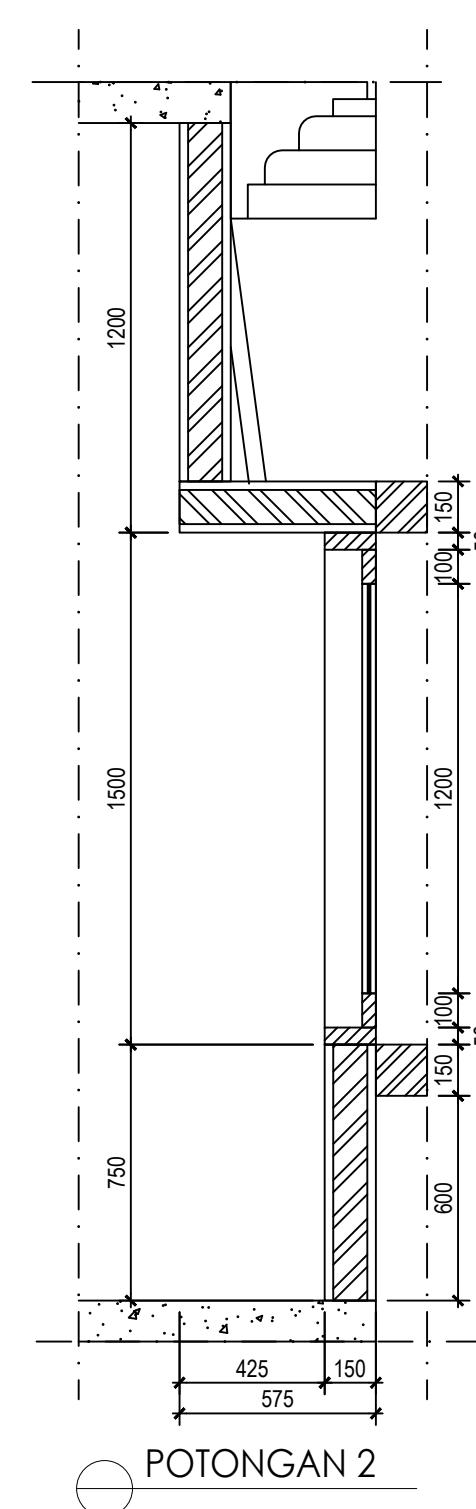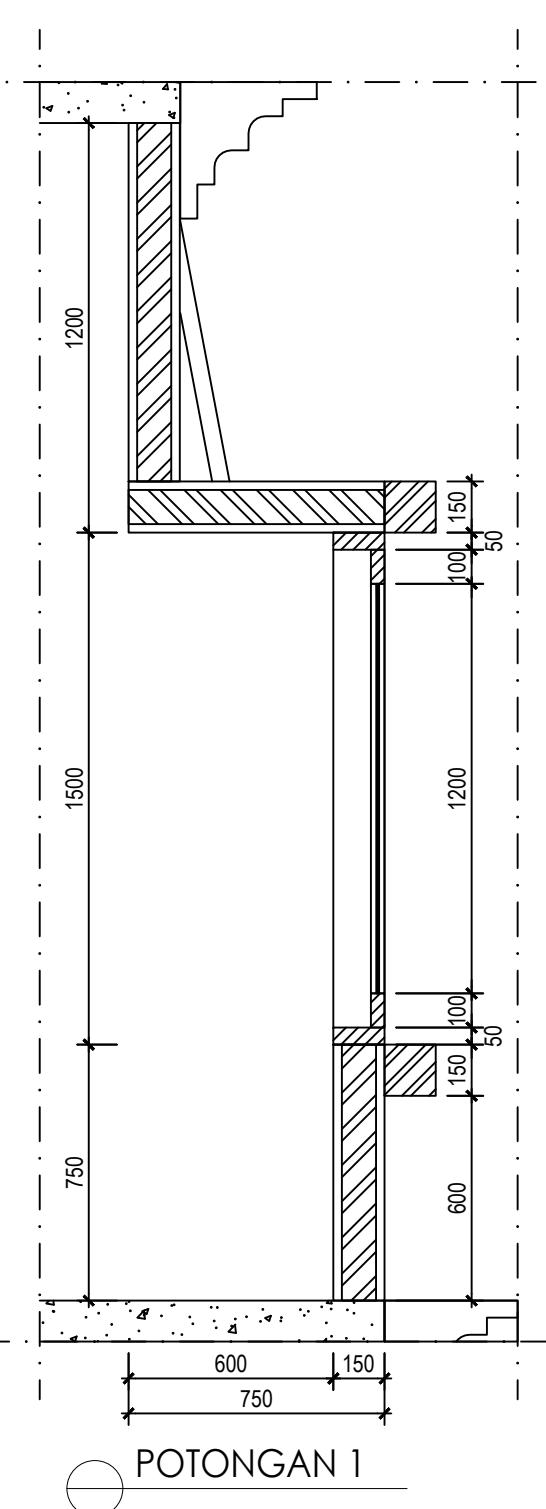

NAMA PROYEK		RESIDENTIAL HOUSE AKASIA 2 / 59	
CATATAN :			
PEMBERI TUGAS			
ARSITEK			
DRAFTING			
JUDUL GAMBAR :			
SKALA :	DIGAMBAR	TGL.	
	DIPERIKSA	TGL.	
	DISETUJUI	TGL.	
	DISETUJUI PEMB. TUGAS		TGL.
DIKELUARKAN UNTUK :			
NO. PROYEK	NO. GAMBAR :	KODE GAMBAR :	REVISI :

W15

BV

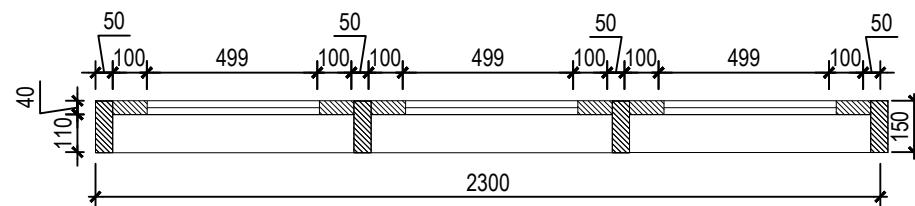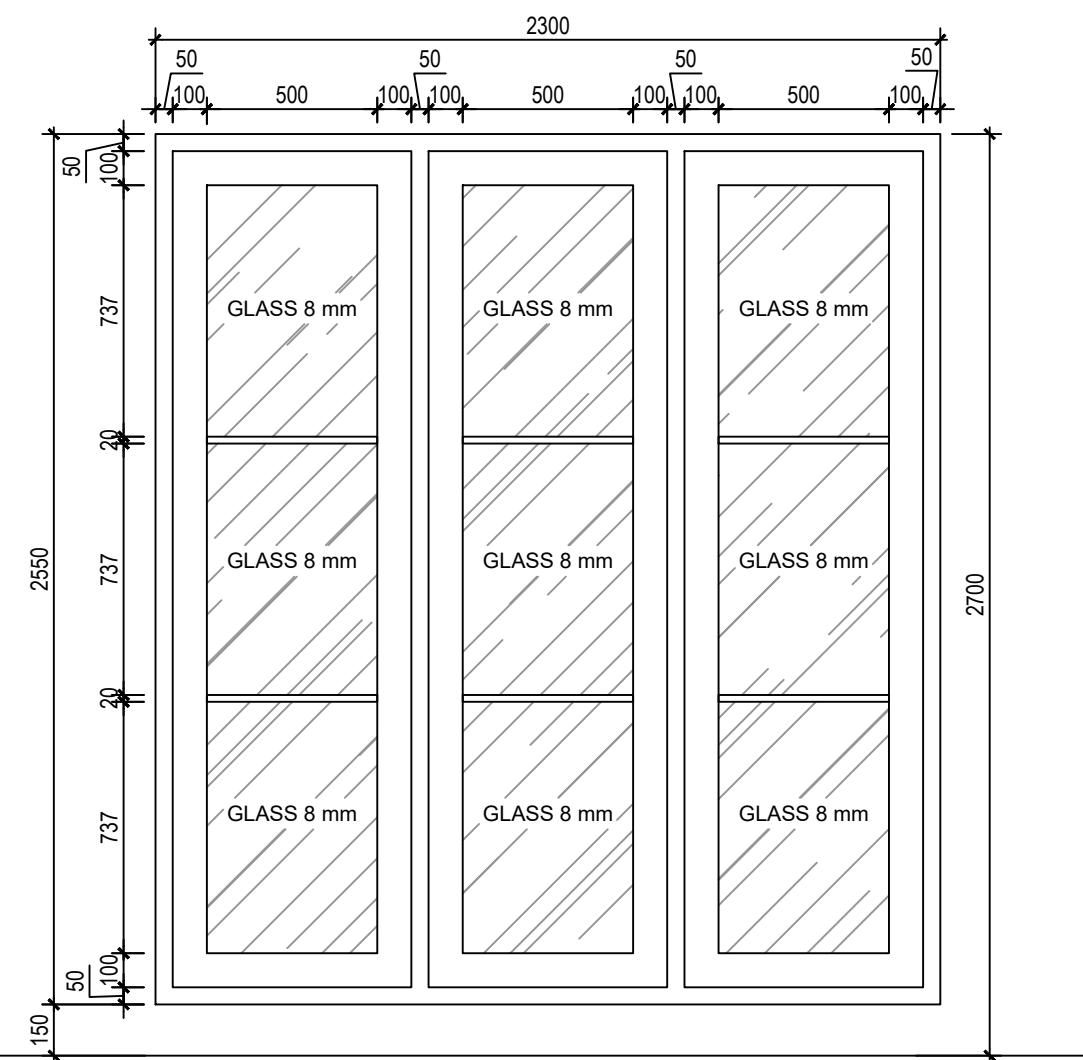

NAMA PROYEK		RESIDENTIAL HOUSE AKASIA 2 / 59		
CATATAN :				
PEMBERI TUGAS				
ARSITEK				
DRAFTING				
				TGL.
JUDUL GAMBAR :				
SKALA :		DIGAMBAR		TGL.
		DIPERIKSA		TGL.
		DISETUJUI		TGL.
DISETUJUI PEMB. TUGAS			TGL.	-
DIKELUARKAN UNTUK :				
NO. PROYEK	NO. GAMBAR :	KODE GAMBAR :	REVISI :	