


01 GROUND FLOOR PLAN

1 : 100

RESIDENTIAL HOUSE AKASIA 2 / 59

NAMA PROYEK		RESIDENTIAL HOUSE AKASIA 2 / 59			
CATATAN :		<p>Semua garis, retangan dan lingkaran semi lingkaran pada gambar ini dibungkus dan diperbaiki tanpa [In] terutama untuk yang telah ditutup dan tidak boleh diketahui berada di dalamnya.</p> <p>Kontraktor berwenang untuk memulihkan dimensi terhadap keadaan lapangan dan apabila ada ketidakcocokan dengan desain arsitektur.</p> <p>Gambar berdimensi tidak diperkenankan diskusi.</p> <p>Sebelum pekerjaan dilaksanakan, kontraktor berwenang untuk meminta persetujuan gambar kerja dan contoh buatan dari Arsitek.</p>			
PEMBERI TUGAS					
ARSITEK		ERIC HANDAYA, S.T I.A.I			
DRAFTING					
JUDUL GAMBAR :		1ST FLOOR PLAN			
SKALA :		DIGAMBAR	TGL.	REVISI	
1:100		DIPERIKSA	TGL.	NO. TOL	
DISETUJUI		TGL.	NO. REVISI		
DIKELUARKAN UNTUK :		FOR DESIGN DEVELOPMENT			
NO. PROYEK		NO. GAMBAR :	KODE GAMBAR :	REVISI :	
		02	AR-02		

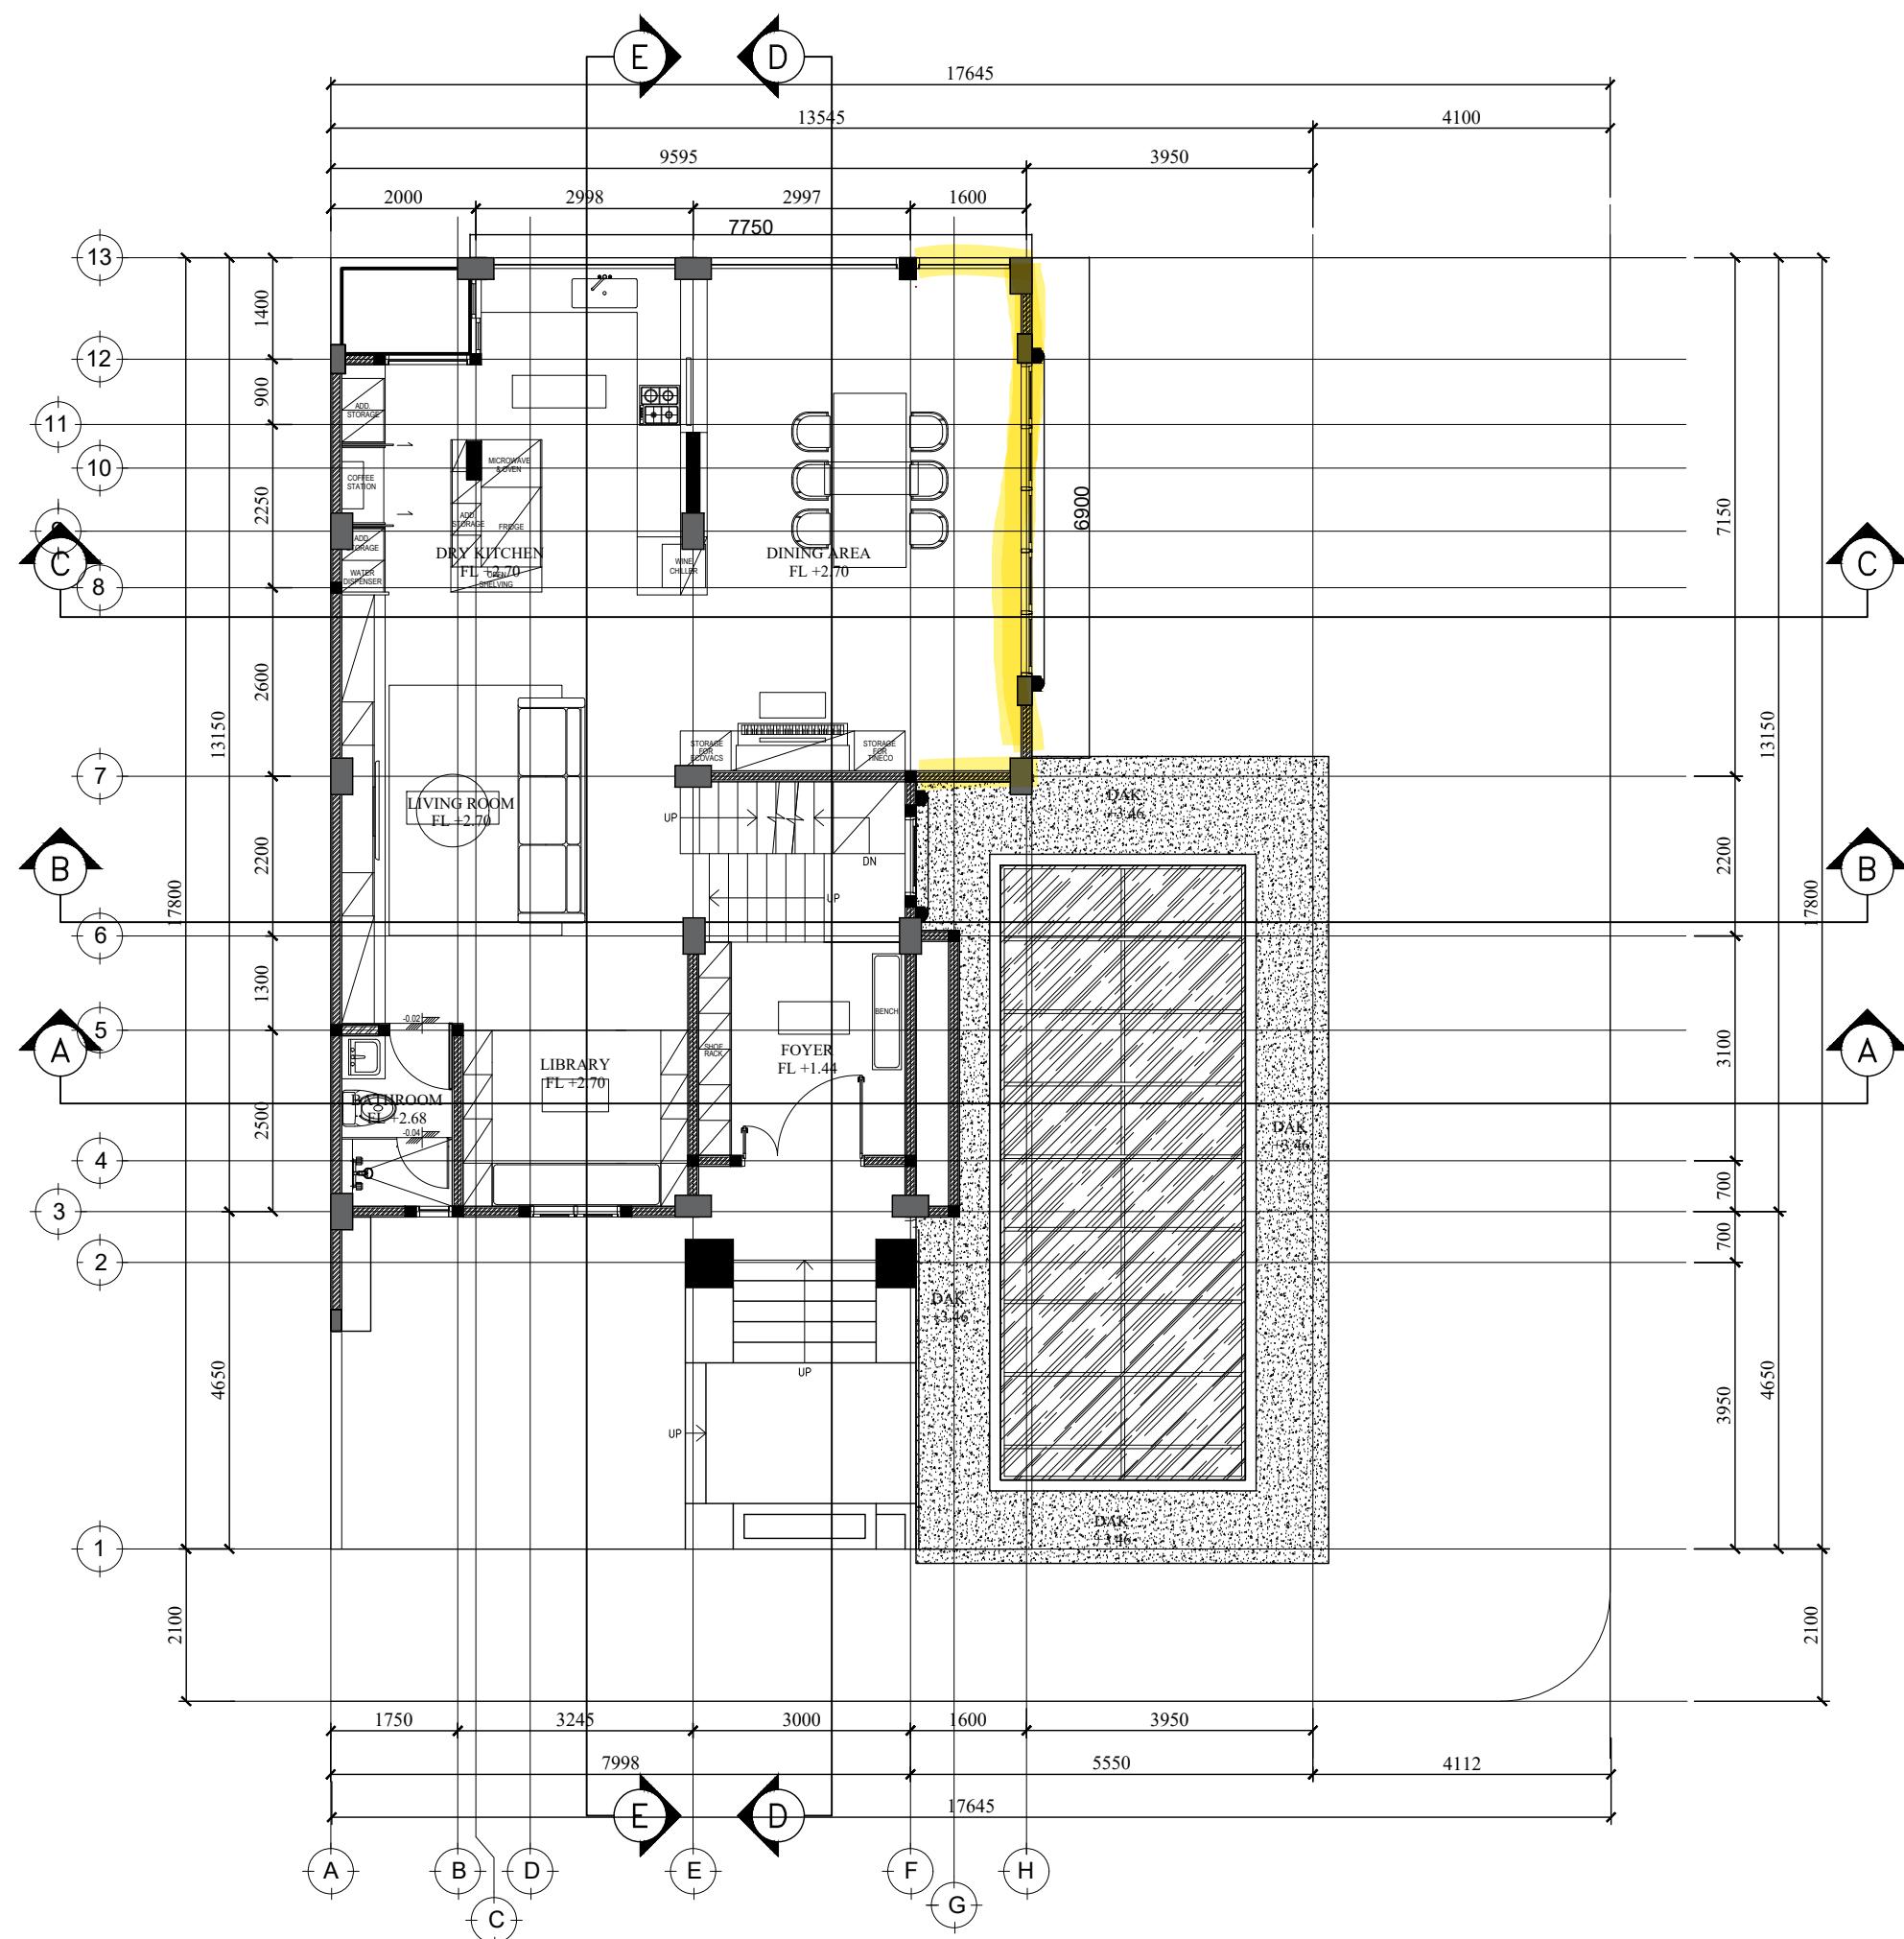

NAMA PROYEK	RESIDENTIAL HOUSE AKASIA 2 / 59					
CATATAN :						
Semua garis, retakan dan lingkaran semi lingkaran pada gambar ini dibungkus oleh Underlay yang terdiri dari garis dan lingkaran yang tidak dituliskan dan tidak boleh diperbaiki tanpa [In] terulis.						
Kontraktor berwenang untuk memulihkan dimensi terhadap keadaan lapangan dan apabila ada ketidaksesuaian dengan desain arsitektur.						
Gambar berdimensi tidak diperkenankan diakses.						
Sebelum pekerjaan dilaksanakan, kontraktor berwenang untuk meminta persetujuan gambar kerja dan contoh bahan dari Arsitek.						
PEMBERI TUGAS						
ARSITEK	ERIC HANDAYA, S.T I.A.I					
DRAFTING						
REVISI						
TGL						
NO.						
JUDUL GAMBAR :						
2ND FLOOR PLAN ROOFTOP FLOOR PLAN						
SKALA :	DIGAMBAR	TGL.				
1:100						
DIPERIKSA		TGL.				
DISETUJUI		TGL.				
DISETUVI PEMB. TUGAS		TGL.	-			
DIKELUARKAN UNTUK :	FOR DESIGN DEVELOPMENT					
NO. PROYEK	NO. GAMBAR :	KODE GAMBAR :	REVISI :			
	03	AR-03				

