


NAMA PROYEK		RESIDENTIAL HOUSE AKASIA 2 / 59					
CATATAN :		<p>Sama dengan rencana dan karya seni yang tertulis pada gambar ini dilindungi oleh Undang-undang Hak Cipta, serta hanya diperbolehkan untuk yang telah ditentukan dan tidak boleh diperbanyak tanpa ijin tertulis.</p> <p>Kontrak berlaku bila terdapat permasalahan dimensi terhadap keadaan lapangan dan apabila ada ketidaksesuaian harus disampaikan kepada Arsitek.</p> <p>Gambar berdimensi tidak diperkenankan diambil.</p> <p>Sebelum pengerjaan dimulai, kontraktor berkewajiban untuk meminta persetujuan gambar kerja dan contoh buah dari Arsitek.</p>					
PEMBERI TUGAS							
ARSITEK		ERIC HANDAYA, S.T I.A.I					
DRAFTING							
JUDUL GAMBAR :		2ND BEAM FLOOR PLAN					
SKALA :		1:100		DIGAMBAR		TGL.	
				DIPERIKSA		TGL.	
				DISETUJUI		TGL.	
DIKELUARKAN UNTUK :		FOR DESIGN DEVELOPMENT					
NO. PROYEK	NO. GAMBAR :	KODE GAMBAR :		REVISI :			
	74	STR-07					

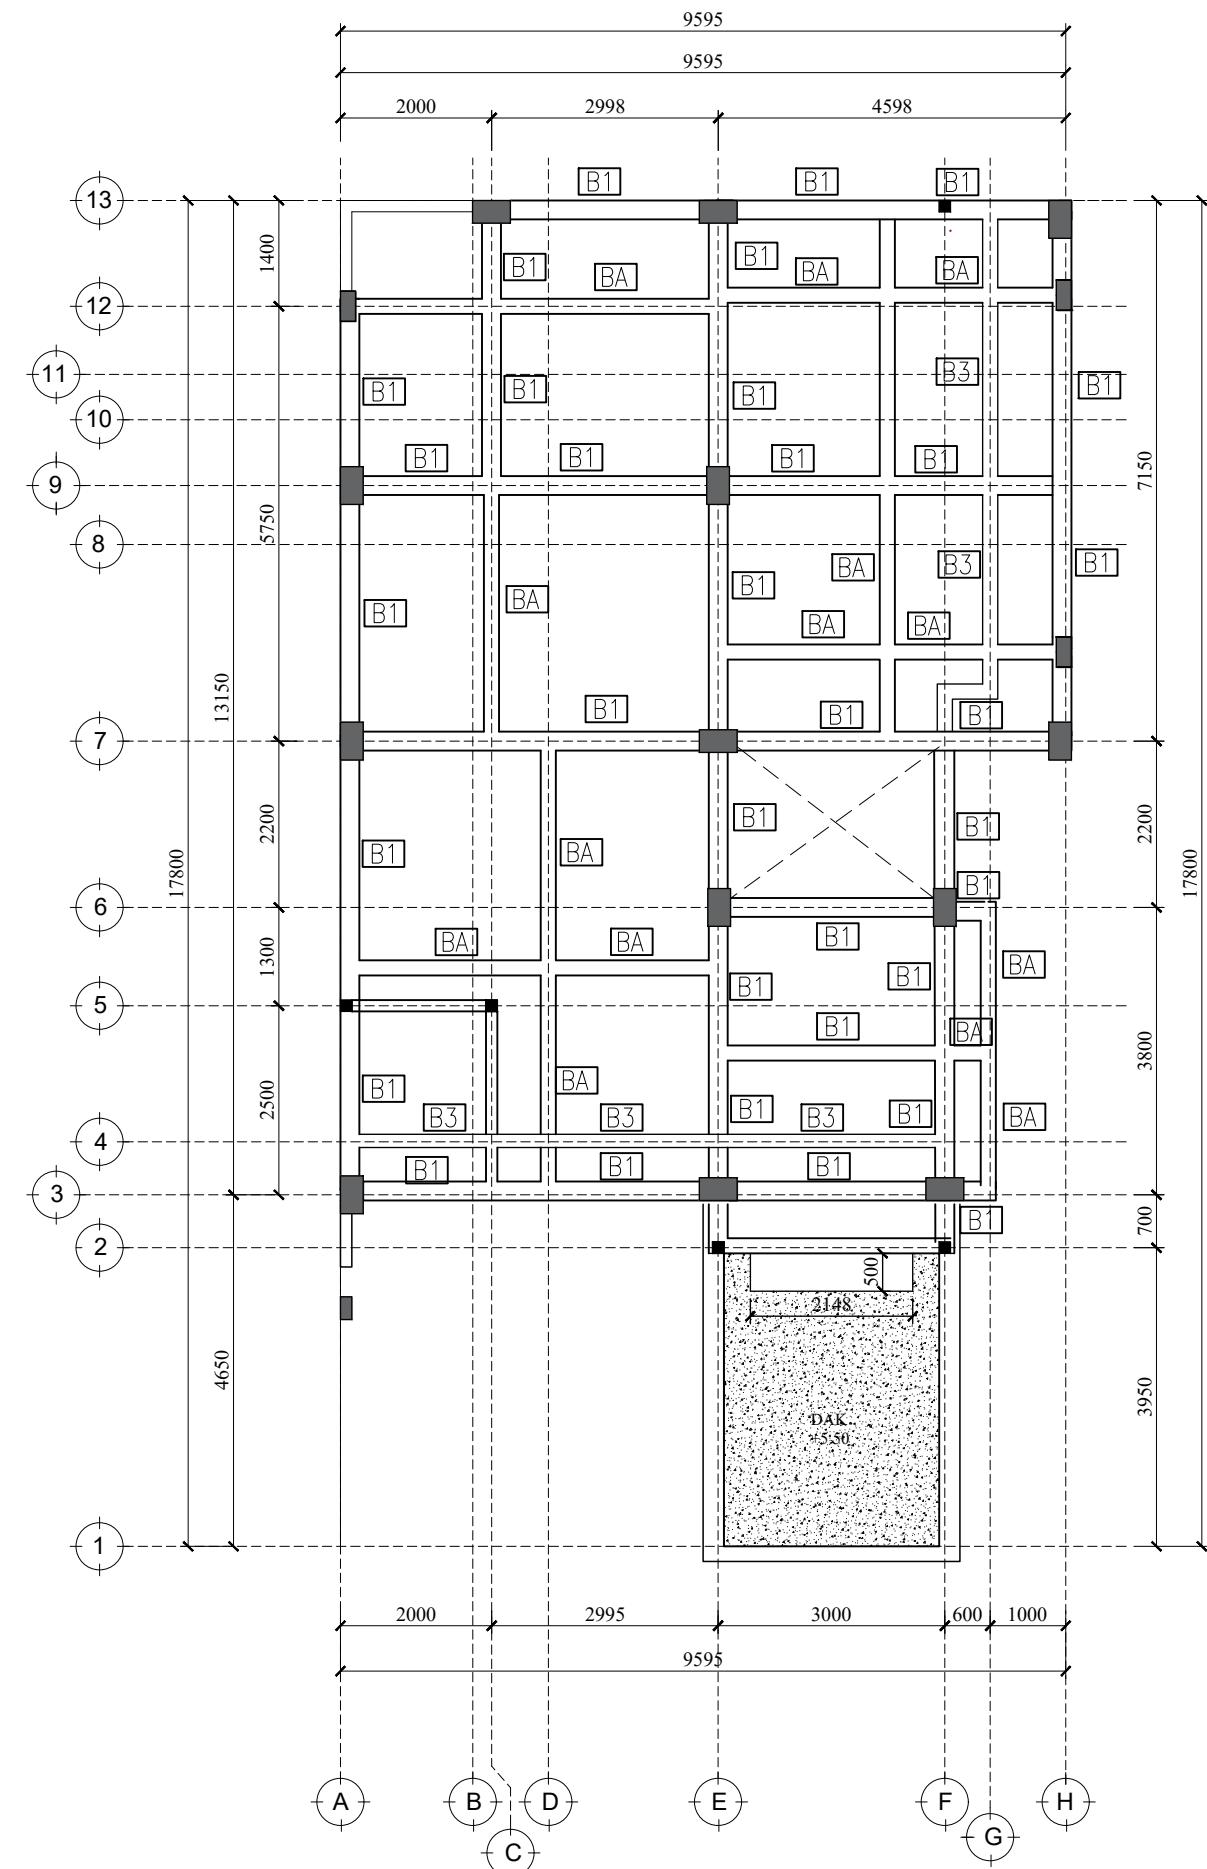

01 2ND BEAM FLOOR PLAN
1 : 100